



АЛЬФА-СТРОЙ
инженерные коммуникации

Общество с ограниченной ответственностью ГК «Альфа-Строй»
ОГРН 1157746689583 ИНН 7743112814 КПП 774301001

Адрес места нахождения: 125080, Москва город, муниципальный округ Сокол, Волоколамское шоссе, дом 1,
строение 1, помещение 1/8.

Почтовый адрес: 107023, г. Москва, Малая Семёновская ул., дом 30.

Заказчик: АНО «АДСТ»

ПРОЕКТНАЯ ДОКУМЕНТАЦИЯ

**Капитальный ремонт здания Государственного бюджетного
общеобразовательного учреждения города Москвы
"Школа №1492" по адресу: г. Москва, ул. Адмирала Лазарева, д. 62, к. 2**

**Раздел 3: Объемно-планировочные и архитектурные решения
Часть 2. Ведомость объемов работ**

(I этап)

203-25-АР.ВОР

Москва, 2026 г.



АЛЬФА-СТРОЙ
инженерные коммуникации

Общество с ограниченной ответственностью ГК «Альфа-Строй»
ОГРН 1157746689583 ИНН 7743112814 КПП 774301001

Адрес места нахождения: 125080, Москва город, муниципальный округ Сокол, Волоколамское шоссе, дом 1,
строение 1, помещение 1/8.

Почтовый адрес: 107023, г. Москва, Малая Семёновская ул., дом 30.

Заказчик: АНО «АДСТ»

ПРОЕКТНАЯ ДОКУМЕНТАЦИЯ

**Капитальный ремонт здания Государственного бюджетного
общеобразовательного учреждения города Москвы
"Школа №1492" по адресу: г. Москва, ул. Адмирала Лазарева, д. 62, к. 2**

**Раздел 3: Объемно-планировочные и архитектурные решения
Часть 2. Ведомость объемов работ
(I этап)**

203-25-АР.ВОР

Ген. директор

Главный инженер

Казаков М. Н.

Гаршин А. М.

Москва, 2026 г.

Оконный блок "REHAU DELIGHT", оконные рамы из ПВХ профиля (ГОСТ 30674-99), применить профиль оконных рам толщиной 70 мм, с двухкамерными стеклопакетами. Толщина стекла 4 мм. Внешнее стекло закаленное. Внутреннее стекло класса защиты СМ1, (не разрушающееся при расстреливании, противобулавном) выполняется в заводских условиях с предоставлением подтверждающего сертификата. Цвет профиля: антрацит, крашенный в массе или ламинация с двух сторон. Цвет: RAL7016 (антрацит глянций) Звукоизоляция конструкции 35 дБА. Приведенное сопротивление теплопередаче - 0,717 ($m^2 \cdot oC/Bt$). применяется покрытие с самоочищающимся покрытием по ГОСТ 33575, обеспечивающую безопасную эксплуатацию и периодическое обслуживание изделий (в т.ч. мытьё стеклом) (согласно ГОСТ 23166-2021 п.6.1.5). — Ручки оконные с полимерным покрытием — Базисная безопасность в нижней части флангулы на тростине или «сэндвич» для возможности устройств для открывания помещения. Необходимо применять детали базисной безопасности, обеспечивающие блокировку распашного отворачивания створки, но позволяющие ей функционировать в откидном положении без риска с обязательным выполнением функции блокировки распашного отворачивания; должны предусматривать запирание как на ключ (т.е. иметь механизм запирания), так и с помощью специального ключа (ручки) без применения замочного механизма (ГОСТ23166-2021); должны соответствовать замкам 1-го класса по ГОСТ 5089	
--	--

Оконный блок из Алюминиевого профиля (ГОСТ 21519-2022), алюминиевый теплоизоляционный Е30, стеклопакет, с двухкамерными стеклопакетами.Применить профиль оконных рам толщиной 70 мм, Окраска порошковая полимерная RAL 7016 (серо-голубой).

Внешние стекла заклеенные. Толщина стекло 6 мм. Внутреннее стекло

класса защиты CM1, (не разрушающееся при раскрекивании, взломе, взломостойкое)

выполняется в заводских условиях с предоставлением подтверждающего сертификата,

соответствующего конструкции 35 дБА.

Коэффициент сопротивления теплопередаче - 0,69 Вт/м²С

применить стекла с самоочищающимся покрытием по ГОСТ 33575, обеспечивающую безопасную эксплуатацию и периодическое обслуживание изделий (согласно ГОСТ 23166-2021 п. 6.1.5).

Technical drawing of a rectangular frame. The overall dimensions are 2300 (width) by 2650 (height). The frame is divided into five rectangular sections by thick black lines. The top section is divided into three equal parts, each 770 wide. The bottom section is divided into two equal parts, each 1150 wide. The height of the top section is 1900, and the height of the bottom section is 750. The drawing is labeled "Ok-5.3 (CM-1) (T1)" at the top center.

Взам. инв. №	_____
--------------	-------

Подп. и дата

205-25-AP


Капитальный ремонт здания Государственное бюджетное общеобразовательное учреждение города Москвы
"Школа № 1492, расположенного по адресу: ул. Адмирала Лазарева, д. 62, к. 2

Изм.	Кол.уч	Лист	№ док	Подпись	Дата	школа № 1432, расположенного по адресу : ул. Адмирала Назирова, в. 62, к. 2			
Разраб.	Китов			Китов	02.26	Объемно-планировочные и архитектурные решения	Стадия	Лист	Листов
							П		

Спецификация Витражных блоков						Спецификация элементов заполнения дверных проемов витражей												
Марка	Наименование	Высота, мм	Длина, мм	Кол-во шт.	Площадь	Описание	Марка покрывающей пленки	Размеры светового проема	Площадь, м²	Количество по этажам						Кол-во всего	Описание	
							Н	Л		Подвал	1 этаж	2 этаж	3 этаж	4 этаж	Крыша			
1. Наружные витражи						Наружные витражные конструкции типа Craft wall с двухкамерными стеклопакетами. Профиль 70 мм. Теплый алюминиевый профиль, окрашен порошковой краской цвет RAL C 7016 Остекление: двухкамерный стеклопакет с терморамкой черного цвета и заполнением аргоном . Внешние стекла-закаленные внутренние стекла-класс защиты SM4. Внешние стекла не должны отличаться по оттенку от стекол в окнах и наружных дверях. Звукоизоляция конструкции 35 дБА. Коэффициент сопротивления теплопередаче -0,833 Вт/м2/°C.	1 Дверные блоки наружные алюминиевые в составе витражных конструкций										Дверь двупольная из алюминиевого профиля толщиной 70мм с порошковой окраской, RAL 7016 текстура муар, утепленная. Полотно двери должно быть в одной плоскости с коробкой с двух сторон; -Остекление - стеклопакет 32мм (наружное стекло закаленное 6мм, с терморамкой черного цвета и заполнением аргоном толщиной 18мм, внутреннее-триплекс из двух стекол толщиной 4мм с двумя пленками 0,76мм), 6зак.-18и-4зак. 4зак. 2. внутреннее стекло класса защиты SM4 по ГОСТ 30826-2014; с бронированной пленкой толщиной 600 микрон, наклеенной на внутренний слой стекла в заводских условиях. Внешние стекла не должны отличаться по оттенку от стекол в окнах и наружных дверях. -Порог-стационарный плоский до 14мм; -Ручки-система "антипаника" на пассивную створку двери (без возможности фиксации створок в дверной коробке), на активной створке - прямая на всю высоту двери с обеих сторон (поручень Ø32-35мм и толщиной стенки не менее 3мм; крепления толщиной 5мм) из нержавеющей стали AISI304; -Доводчик на обе створки со скользящей тягой и регулируемым усилием EN 2-4, цвет RAL7016, предусмотреть координаторы с последовательным закрыванием дверных створок; -Петли накладные цвет RAL 7016; -Замок-электромеханический с установкой в верхний профиль доборного полотна; - Электромагнитная защелка для основной створки: нормально - открытая. Косой ригель для электромагнитной защелки, цвет RAL 7016; - Цилиндр под замок: ключ (наружная сторона)-барашек (внутренняя сторона),цвет RAL 7016; Звукоизоляция конструкции 35 дБА. Приведенное сопротивление теплопередаче -0,752 Вт/м2/°C. ширина светового проема 1400 мм, ширина светового проема активной створки не менее 900 мм, при открывании на 90° -СКУД (материал корпуса - пластик в наружном исполнении)	
B-1.1	в стенах актового зала (№ 244)	4200	1700	2	7,1		без открывания										2	двупольная, активная створка- правая,
B-1.2	в стенах универсального помещения (№ 234)	4200	1700	4	7,1		Верхние и нижние фрамуги - глухие, в середине створка с откидным открыванием, с механизмом дистанционного открывания и запирания откидной створки для проветривания из комнаты инструктора (№ 214) и с механизмом автоматического открывания и запирания по сигналу противодымной вентиляции. Створка оборудована москитной сеткой.										4	двупольная, активная створка- левая,
B-2.1	Зенитные фонари универсальном спортзалом (№ 211)	1700	9100	12	15,5		Откидное окно ALT W72 с механизмом дистанционного открывания и запирания откидной створки для проветривания из комнаты инструктора (№214).											
B-2.2		1230	2350	12	1,4		без открывания											
B-2.3	Зенитные фонари в помещениях: 402,422, 414,415, 424.	1750	3060	8	5,4		без открывания											
B-3.1	наружные тамбуры (№101,124) в многофункциональном информационном библиотечном центре с зоной для индивидуальных занятий (№ 430) и референс-сервисом	2770	2130	4	5,9		профиль окрашен порошковой краской цвет RAL C 7016 муар. Стекла противоударные, с бронированной пленкой толщиной 600 микрон, наклеенной на внутренний слой стекла в заводских условиях. Коэффициент сопротивления теплопередаче-0,752 Вт/м2/°C.											
B-3.2		2770	12330	2	34,1		Противоударное с бронированной пленкой толщиной 600 микрон, наклеенной на внутренний слой стекла в заводских условиях. Имеется откидное окно на 90 градусов в вертикальном положении с механизмом автоматического открывания по сигналу противодымной вентиляции. Нижнее заполнение витража на высоту 2200 мм выполнено стемалитом RAL C 7016.											
B-4		5800	9660	2	50,1		Противоударное с бронированной пленкой толщиной 600 микрон, наклеенной на внутренний слой стекла в заводских условиях. Имеется откидное окно на 90 градусов в вертикальном положении с механизмом автоматического открывания по сигналу противодымной вентиляции. Нижнее заполнение витража на высоту 1100 мм выполнено стемалитом RAL C 7016.											
B-4.1		5800	9660	2	50,1		Противоударное с бронированной пленкой толщиной 600 микрон, наклеенной на внутренний слой стекла в заводских условиях. Имеется откидное окно на 90 градусов в вертикальном положении с механизмом автоматического открывания по сигналу противодымной вентиляции. Нижнее заполнение витража на высоту 1100 мм выполнено стемалитом RAL C 7016.											
B-5		2370*	12960	1	30,6	Противоударное с бронированной пленкой толщиной 600 микрон, наклеенной на внутренний слой стекла в заводских условиях. Заполнение витража выполнено стемалитом RAL C 7016.												
B-5.1		2370*	12960	1	30,6	Противоударное с бронированной пленкой толщиной 600 микрон, наклеенной на внутренний слой стекла в заводских условиях. Заполнение витража на высоту 1100 мм выполнено стемалитом RAL C 7016.												
B-6		4940*	12960	2	64	Противоударное с бронированной пленкой толщиной 600 микрон, наклеенной на внутренний слой стекла в заводских условиях. Заполнение витража на высоту 1100 мм выполнено стемалитом RAL C 7016.												
2.Внутренние витражи						2 Дверные блоки внутренние алюминиевые в составе витражных конструкций										Дверь противопожарная EIW 30 (типа Craftwall). Дверной блок алюминиевый остекленный с телескопической алюминиевой коробкой и алюминиевыми доборами. -Площадь остекления дверного полотна должна составлять: не менее 70% от площади всего дверного полотна. -Размер наличника дверной коробки по петлевой стороне: не менее 55х9 мм, с обратной стороны88х9 мм. -Алюминиевый профиль с эндотермическим расширением и терморазрывом -Цвет: RAL 7016 - Толщина профиля дверного полотна: 64 +-2 мм, цвет RAL 7016. Полотно двери должно быть в одной плоскости с коробкой с двух сторон; Заполнение дверного полотна: стекло-триплекс с двух сторон с закаленными стеклами 4мм, (4зак.4зак.2) класс защиты CM4 Фурнитура - Доводчики со скользящей тягой с регулируемым усилием EN 1-4(на обе створки и синхронизацией для двусторчатых), встроенным фиксатором в открытом положении и встроенным ограничителем угла открывания дверного полотна, цвет RAL7016; - Петли роликовые регулируемые, цвет RAL 7016; - Ручка - прямая на всю высоту двери с обеих сторон (поручень Ø32-35мм и толщиной стенки не менее 3мм; крепления толщиной 5мм) из нержавеющей стали AISI304 - Замок: механический роликовый замок с цилиндровым механизмом, цвет RAL7016; - Звукоизоляция : не менее 32 дБ Количество циклов открывания двери и фурнитуры: не менее 500 000 * внешнее стекло должно быть аналогично по оттенку стеклу, которое устанавливается в окнах и в витражах		
							Дв-28л	2100	1200	2,52	-	1	-	-	-	-	1	двупольная, активная створка- левая, ширина светового проема 1200 мм, ширина светового проема активной створки не менее 900 мм, при открывании на 90°. -без порога
							Дв-29л	2100	1200	2,52	-	-	-	-	1	-	1	двупольная, активная створка- левая, ширина светового проема 1200 мм, ширина светового проема активной створки не менее 900 мм, при открывании на 90°. -без порога
							Дв-30л	2100	900	1,89	-	-	-	1	-	-	1	однополюсная, левого открывания, ширина светового проема не менее 900 мм, при открывании на 90°. -без порога
							Дв-31л	2100	900	1,89	-	1	-	-	-	-	1	однополюсная, левого открывания, ширина светового проема не менее 900 мм, при открывании на 90°. -оклейка бронированной пленкой толщиной 600 микрон, на внутренний слой стекла в заводских условиях -СКУД (материал корпуса - пластик) -без порога
B-7	кабинет с рабочим пространством для учителей (№ 108)	3010	4200	1	12,6	EIW 30 Остекление до отм. +2,650 от у.ч.пола этажа, выше отм.+2,650 глухое заполнение по месту после прокладки инженерных коммуникаций				2,52	-	2	-	-	-	-	2	двупольная, активная створка- правая, ширина светового проема 1200 мм, ширина светового проема активной створки не менее 900 мм, при открывании на 90°. - С выпадающим порогом
B-8	комната охраны (№ 106)	2110	3600	1	10,4	EIW 30 Заполнение – стекло оклеенное бронированной пленкой 600 мкм на внутренний слой стекла в заводских условиях. Выполнить распашное окно 800х800мм. на отм. +900 от у.ч.л. Остекление до отм. +2,650 от у.ч.пола этажа, выше отм.+2,650 глухое заполнение по месту после прокладки инженерных коммуникаций				2,52	-	2	-	-	-	-	2	двупольная, активная створка-левая, ширина светового проема 1200 мм, ширина светового проема активной створки не менее 900 мм, при открывании на 90°. - С выпадающим порогом
B-9.1	гардероб для обучающихся (№ 116)	3010	5800	2	17,5	EIW 30 . Остекление до отм. +2,650 от у.ч.пола этажа, выше отм.+2,650 глухое заполнение по месту после прокладки инженерных коммуникаций												
B-10	кабинет для индивидуальных занятий (№ 315)	3010	5000	1	15,1	EIW 30 Остекление до отм. +2,650 от у.ч.пола этажа, выше отм.+2,650 глухое заполнение по месту после прокладки инженерных коммуникаций												
B-11	адм. кабинет (№ 308) кабинет для инд. занятий (№309)	1230	1700	4	2,1	EIW 45												
B-13	инф. библиотечный центр (№ 430)	3010	6050	1	18,2	EIW 30 Остекление до отм. +2,650 от у.ч.пола этажа, выше отм.+2,650 глухое заполнение по месту после прокладки инженерных коммуникаций												


						205-25-AP			
						Капитальный ремонт здания Государственного бюджетного общеобразовательного учреждения города Москвы "Школа № 1492, расположенного по адресу: ул. Академическая, д. 62, к. 2			
Изм.	Кол-во	Лист	Метр	Подпись	Дата				
Разраб.		Копия		<i>Киселёв</i>	02.24	Объемно-планировочные и архитектурные решения			
						Сводная	Лист	Листов	
						П			
Н. контр.	Казанков			<i>Киселёв</i>	02.24	Спецификация витражных блоков			
						Общество с ограниченной ответственностью "СК-4"			

Наружные витражные блоки

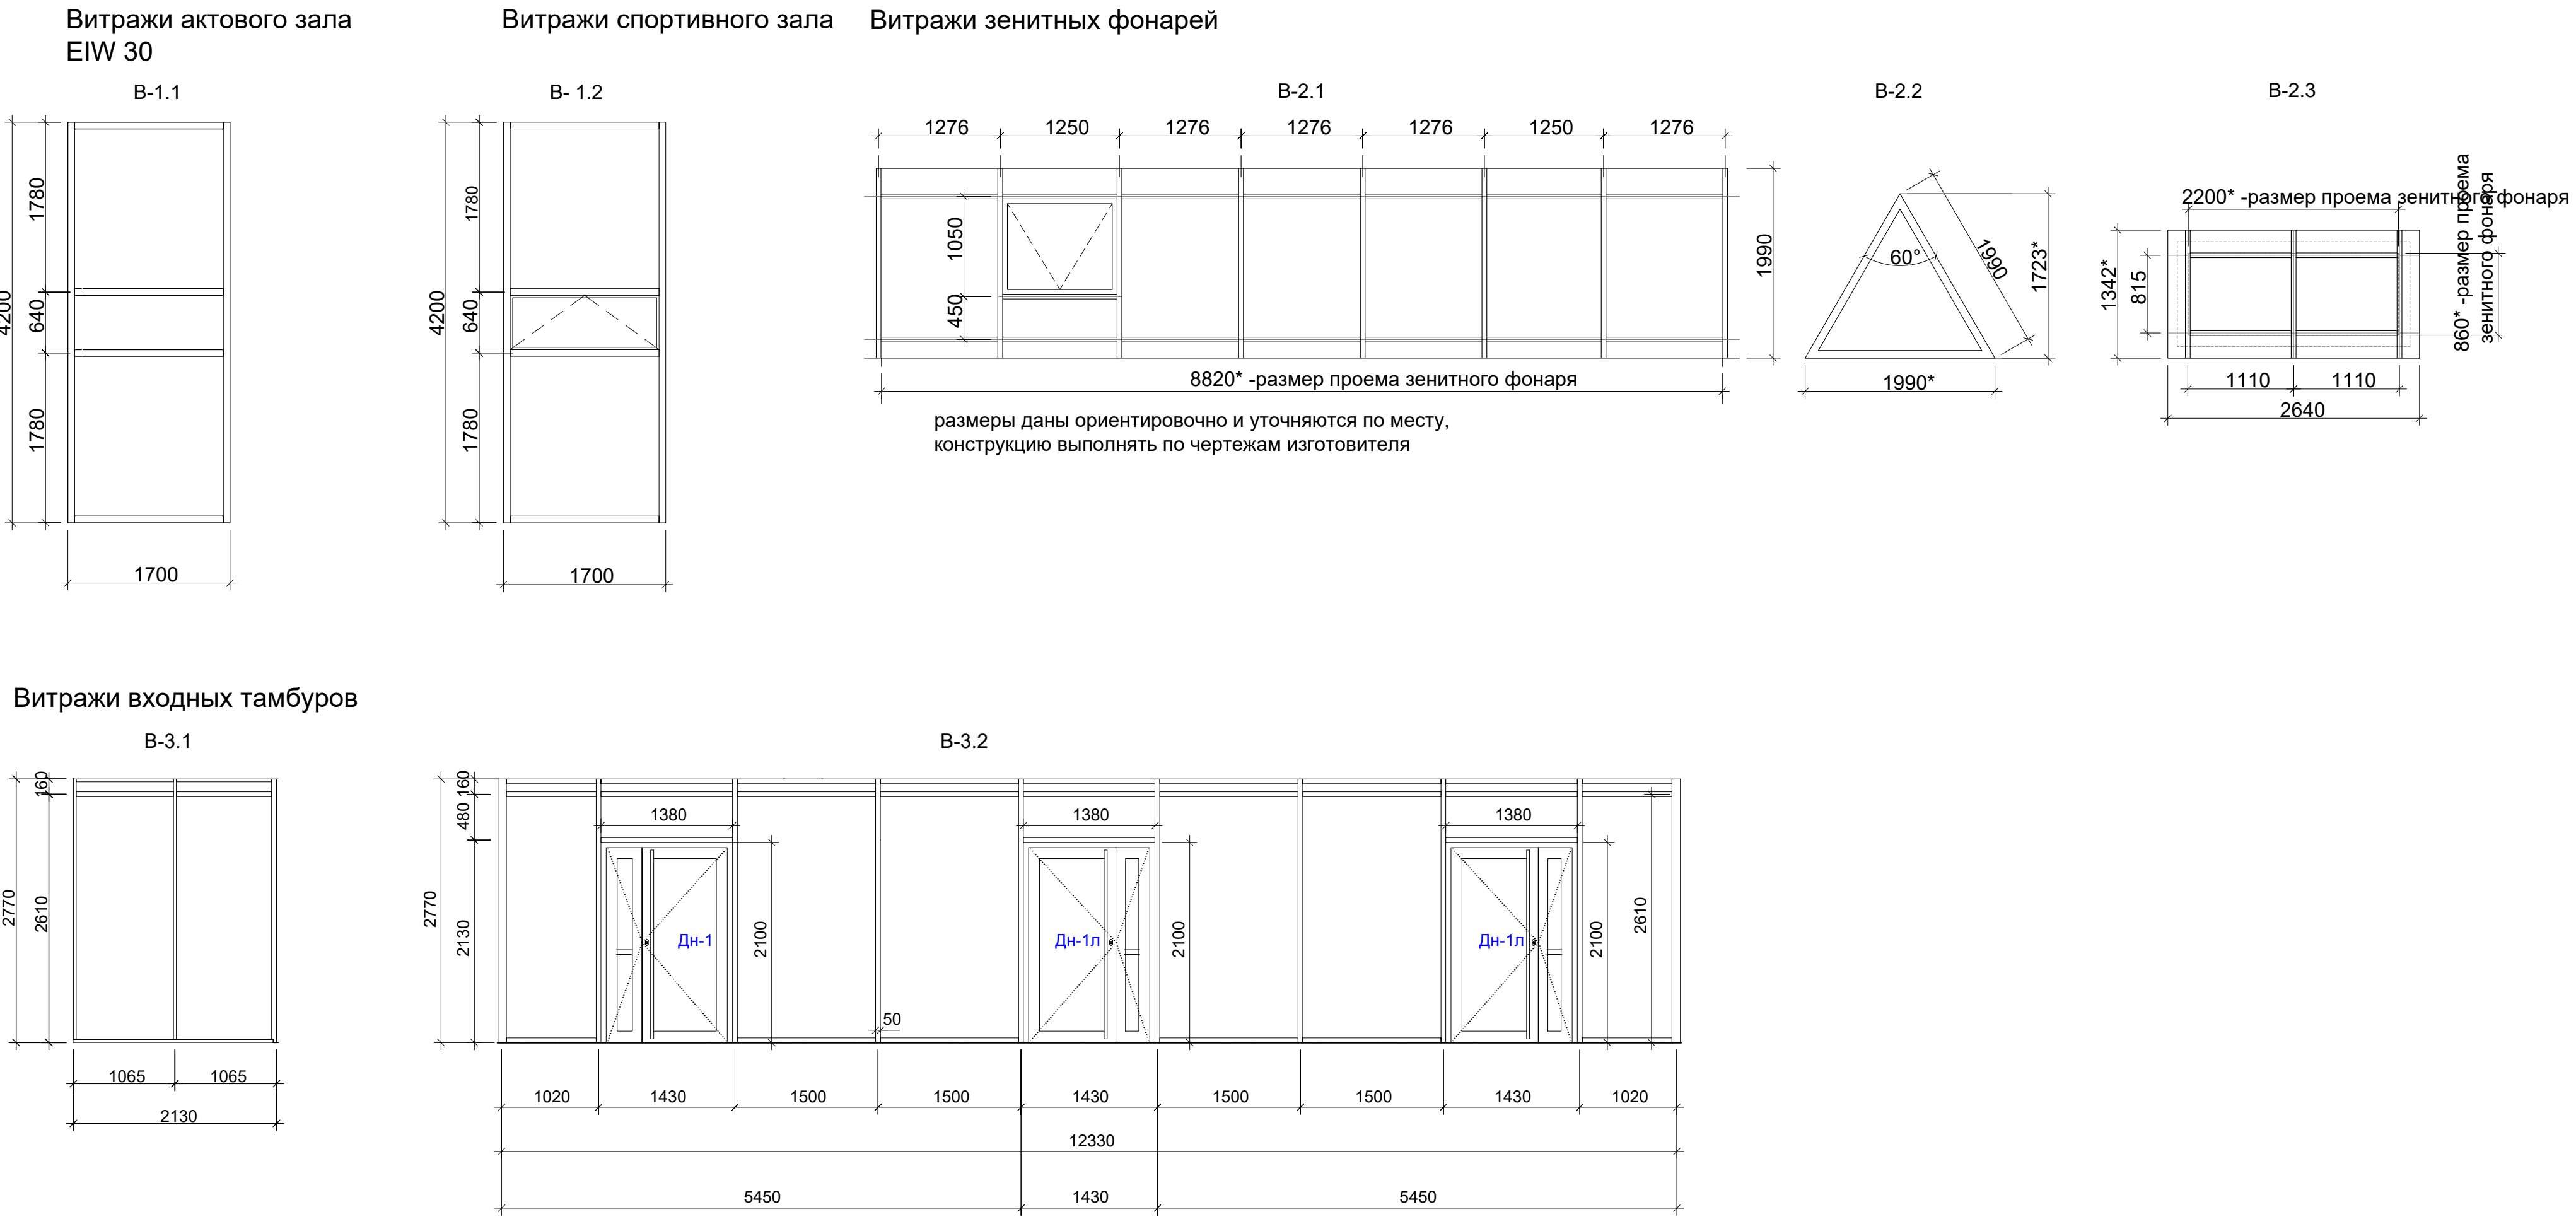


Витражи рекреации и информационного центра 4-го этажа

В-6

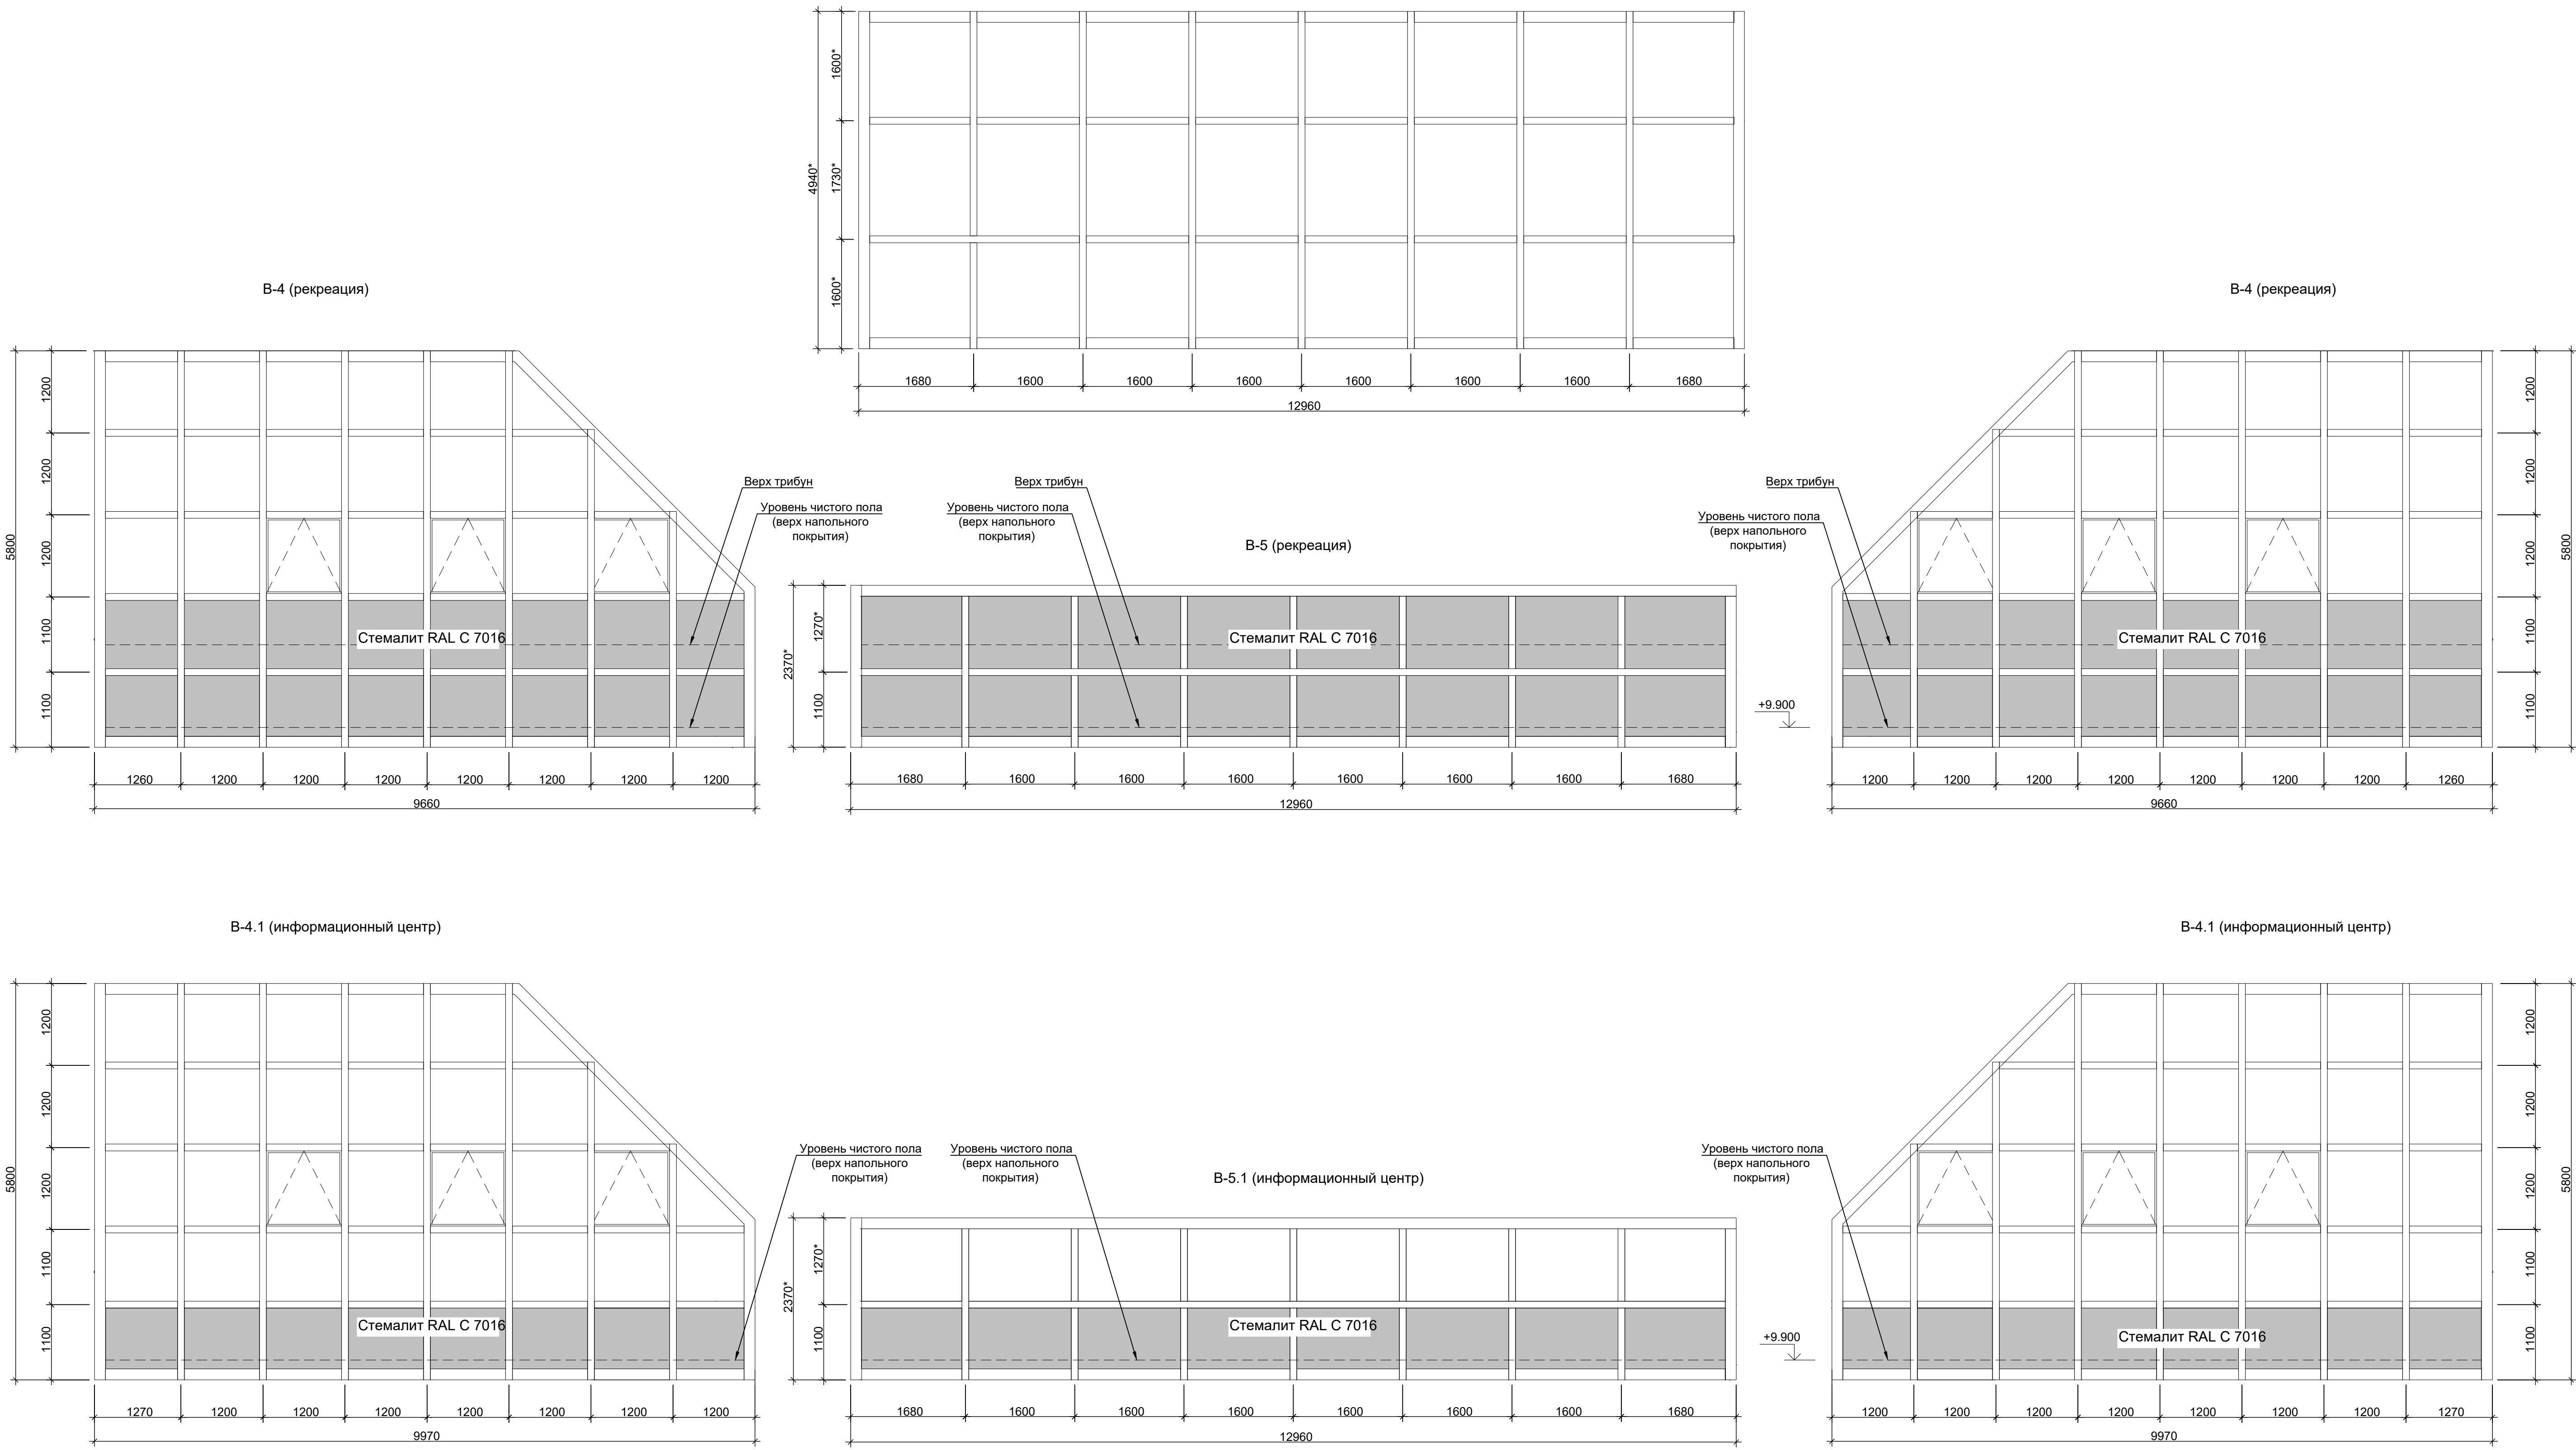

Внутренние витражные блоки

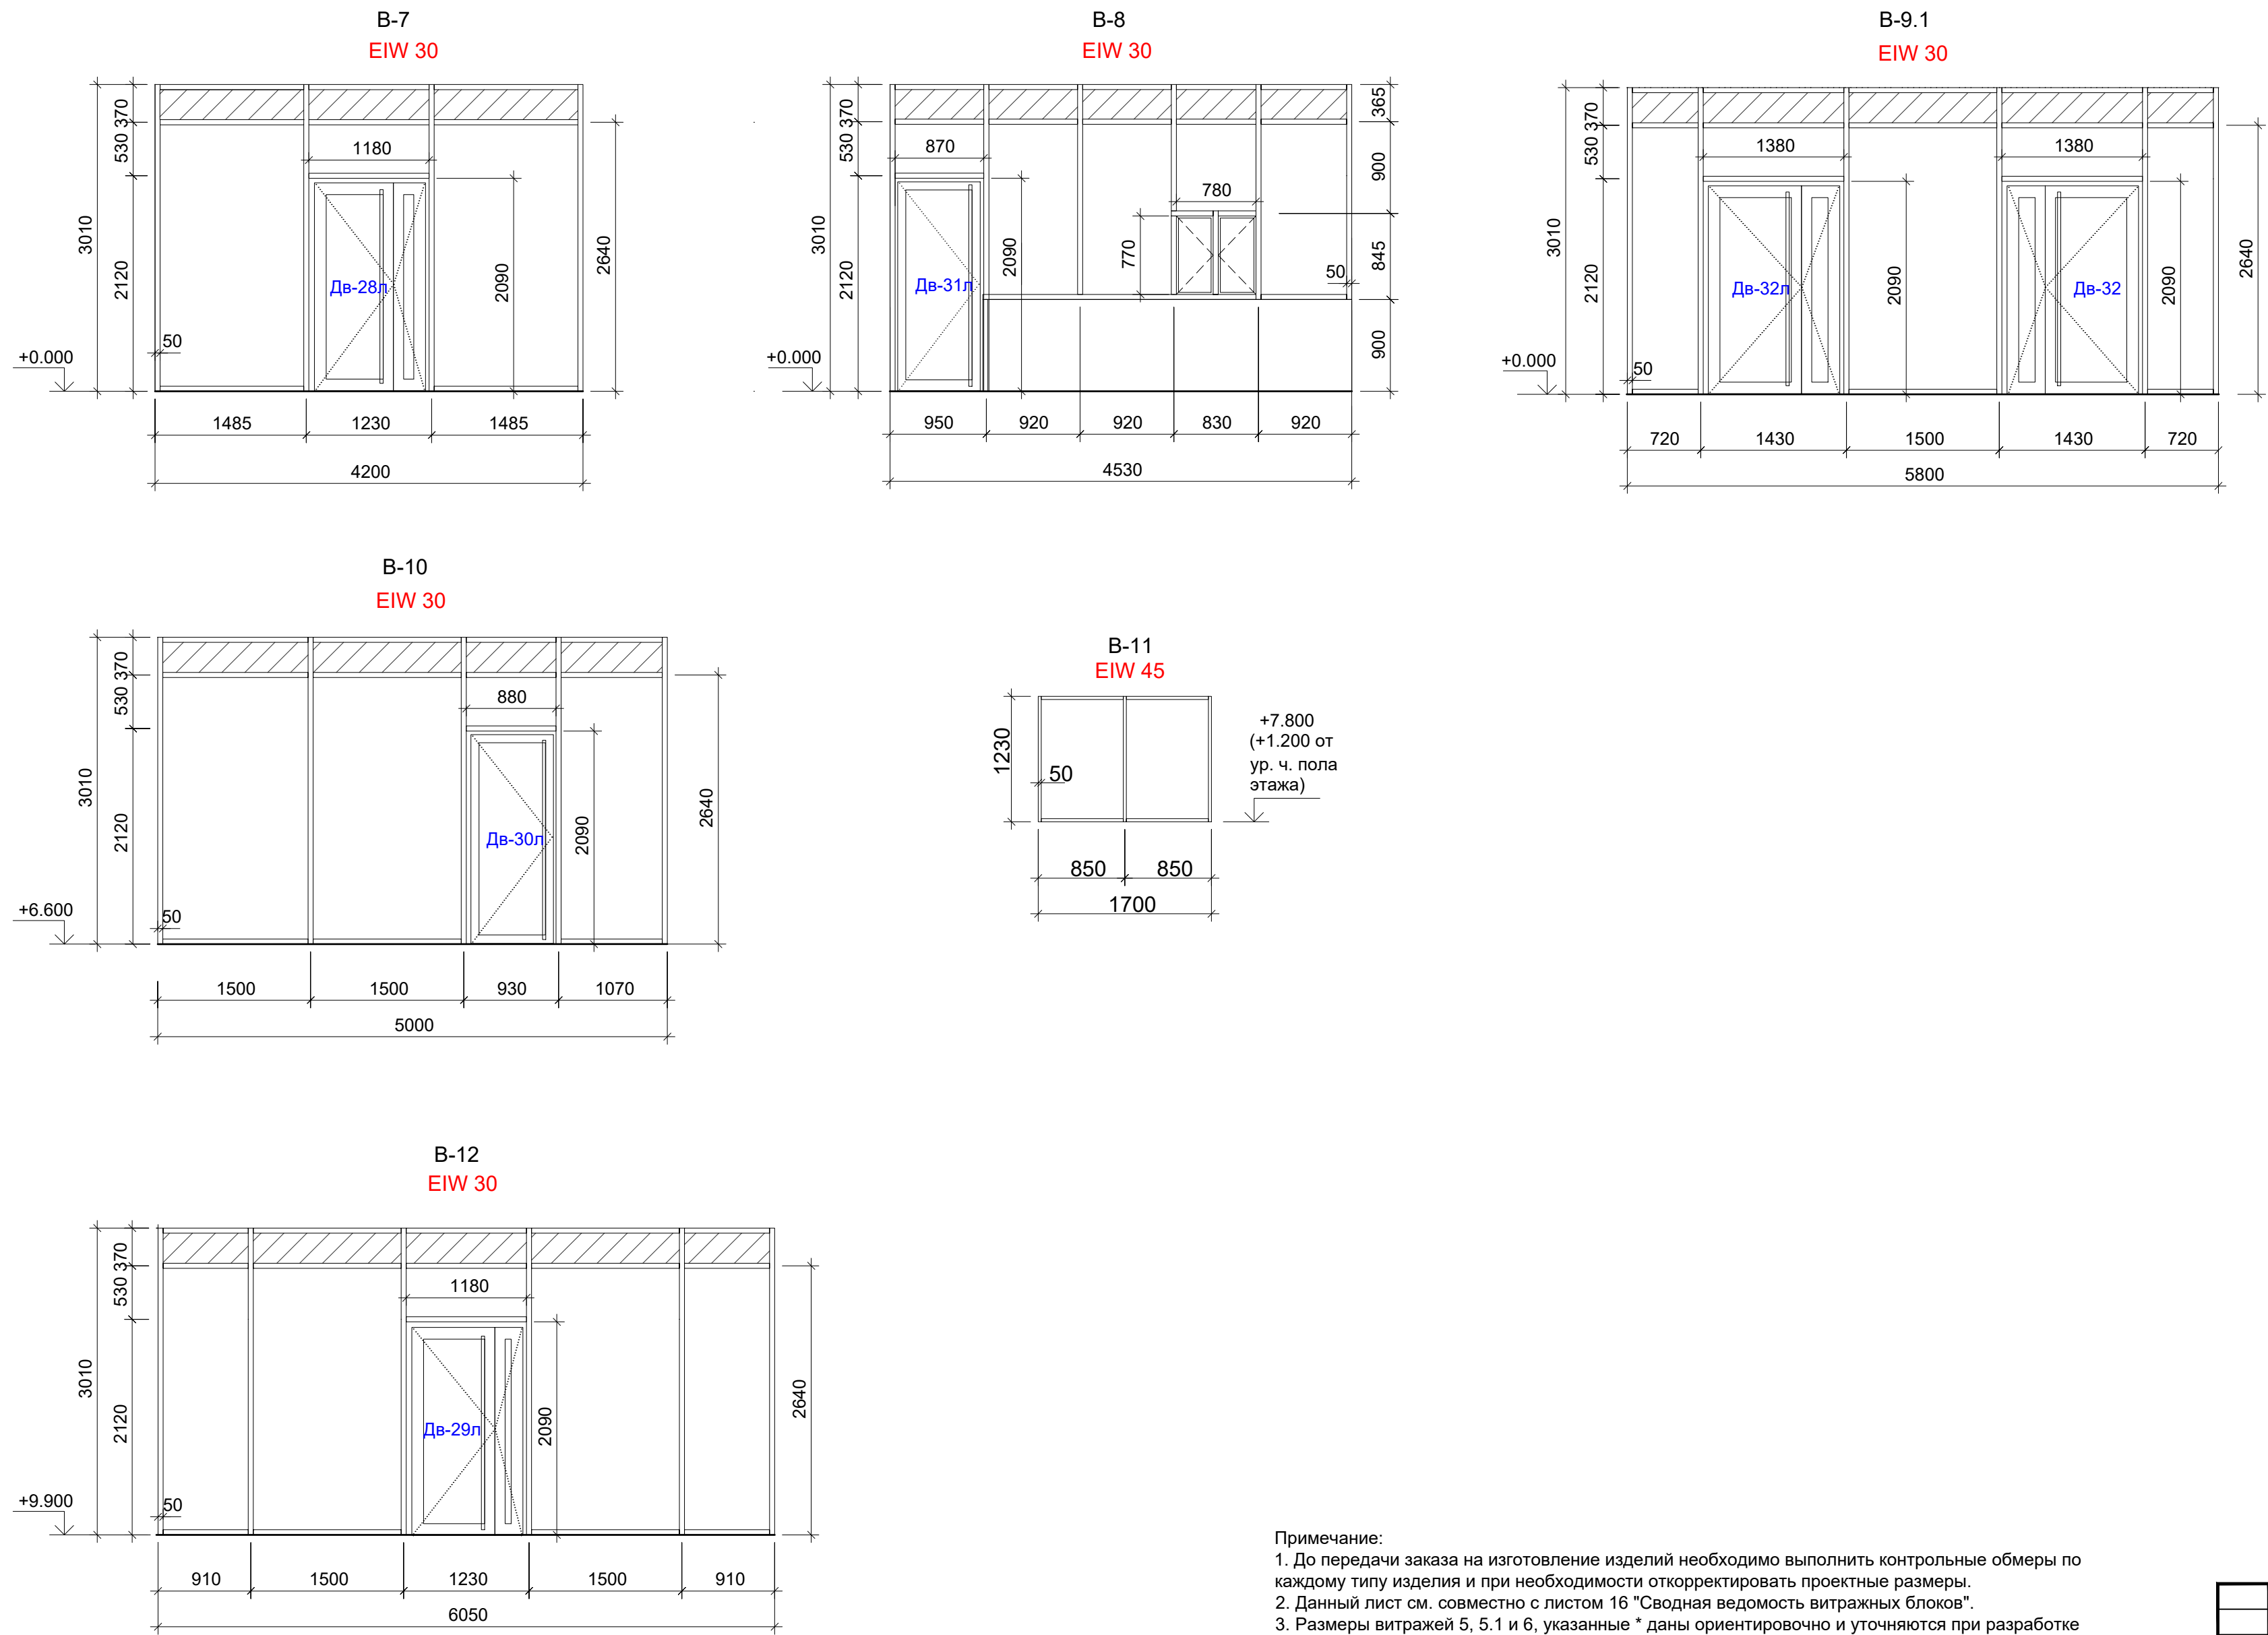

Примечания:
1. До передачи заказа на изготовление изделий необходимо выполнять контрольные обмеры по каждому типу изделия и при необходимости корректировать проектные размеры.
2. Данный лист см. совместно с листом 16 "Сводная ведомость витражных блоков".
3. Размеры витражей 5, 5.1 и 6, указанные даны ориентировочно и уточняются при разработке витражной конструкции - горизонтальные импосты должны совпадать с горизонтальными импостами витражей 4 и 4.1

Марка	Обозначение	Номер Помещения	Схема	Описание	Кол-во на этаже, п.м.								Кол-во п.м.	Площадь м²
					Подвал	1 этаж	2 этаж	3 этаж	4 этаж	5 этаж	6 этаж	7 этаж		
ПД-1	ГОСТ 1396-2019	104, 106, 125, 127, 136, 137, 138, 139, 140	2050	Подоконник из керамогранита 1200x400 мм Kerama Marazzi Монфорте белый матовый 14010R	0,00	23,00	0,00	0,00	0,00	23,00	10,12			
ПД-2	ГОСТ 32274-2021	115, 143, 207, 208, 237, 238, 306, 323, 324, 406, 407, 434		Подоконная доска из березовой фанеры (толщ. не менее 24 мм), в противопожарной обработке КМ1 (КМ0 для путей эвакуации). Фасад: МДФ (толщ. 12 мм), высотой не менее 595 мм, в противопожарной обработке КМ1 (КМ0 для путей эвакуации), окрашен матовой эмалью с обеих сторон. Каркас: фанера толщиной не менее 15 мм, окраска матовым лаком с двух сторон.	0,00	16,70	16,10	15,10	18,40	87,30	53,16			
ПД-2.1	ГОСТ 32274-2021	108, 109, 121, 122, 146, 147, 203, 204, 211, 212, 234, 235, 240, 241, 242, 303, 304, 313, 314, 315, 320, 312, 329, 330, 403, 404, 408, 409, 432, 436		Подоконная доска из березовой фанеры (толщ. не менее 24 мм), в противопожарной обработке КМ1 (КМ0 для путей эвакуации). Фасад: МДФ (толщ. 12 мм), высотой не менее 595 мм, в противопожарной обработке КМ1 (КМ0 для путей эвакуации), окрашен матовой эмалью с обеих сторон. Каркас: фанера толщиной не менее 15 мм, окраска матовым лаком с двух сторон.	0,00	15,91	17,35	82,90	81,50	297,94	149,27			
ПД-3	ГОСТ 1396-2019	201, 213, 232, 243, 301, 316, 319, 331, 401, 412, 421, 431		Подоконник керамогранитный 600x600x9 Про Лаймстоун серый светлый натуральный Kerama Marazzi D0641020R	0,00	0,00	5,95	15,70	7,80	30,15	9,81			
ПД-4		231, 244		Оштукатуривание и окрашивание	0,00	0,00	10,20	0,00	0,00	10,20	3,42			
Общий итог					0,00	105,61	119,60	114,70	107,70	448,59	225,78			

Марка	Обозначение	Номер Помещения	Схема	Описание	Кол-во на этаже, п.м.					Кол-во п.м.	Площадь, м²	Примечание
					Подвал	1 этаж	2 этаж	3 этаж	4 этаж			
ПДМ-1	ГОСТ 32274-2021	126, 202, 233, 302, 318		Горизонтальная поверхность верхнего яруса из березовой фанеры толщ. 24 мм, в противопожарной обработке КМ1 (КМО для путей эвакуации).	0,00	17,58	1,66	1,66	0,00	40,97	37,55	
ПДМ-2	ГОСТ 32274-2021	126, 202, 233, 302, 318, 402, 422		Горизонтальная поверхность верхнего яруса из березовой фанеры толщ. 24 мм, в противопожарной обработке КМ1 (КМО для путей эвакуации).	0,00	5,85	1,68	1,68	17,58	46,83	23,42	
ПДМ-3	ГОСТ 32274-2021	402,422		Горизонтальная поверхность верхнего яруса из березовой фанеры толщ. 24 мм, в противопожарной обработке КМ1 (КМО для путей эвакуации).	0,00	0,00	0,00	0,00	17,77	17,77	13,72	
Общий итог					0,00	23,43	23,34	23,34	35,35	105,57	74,68	








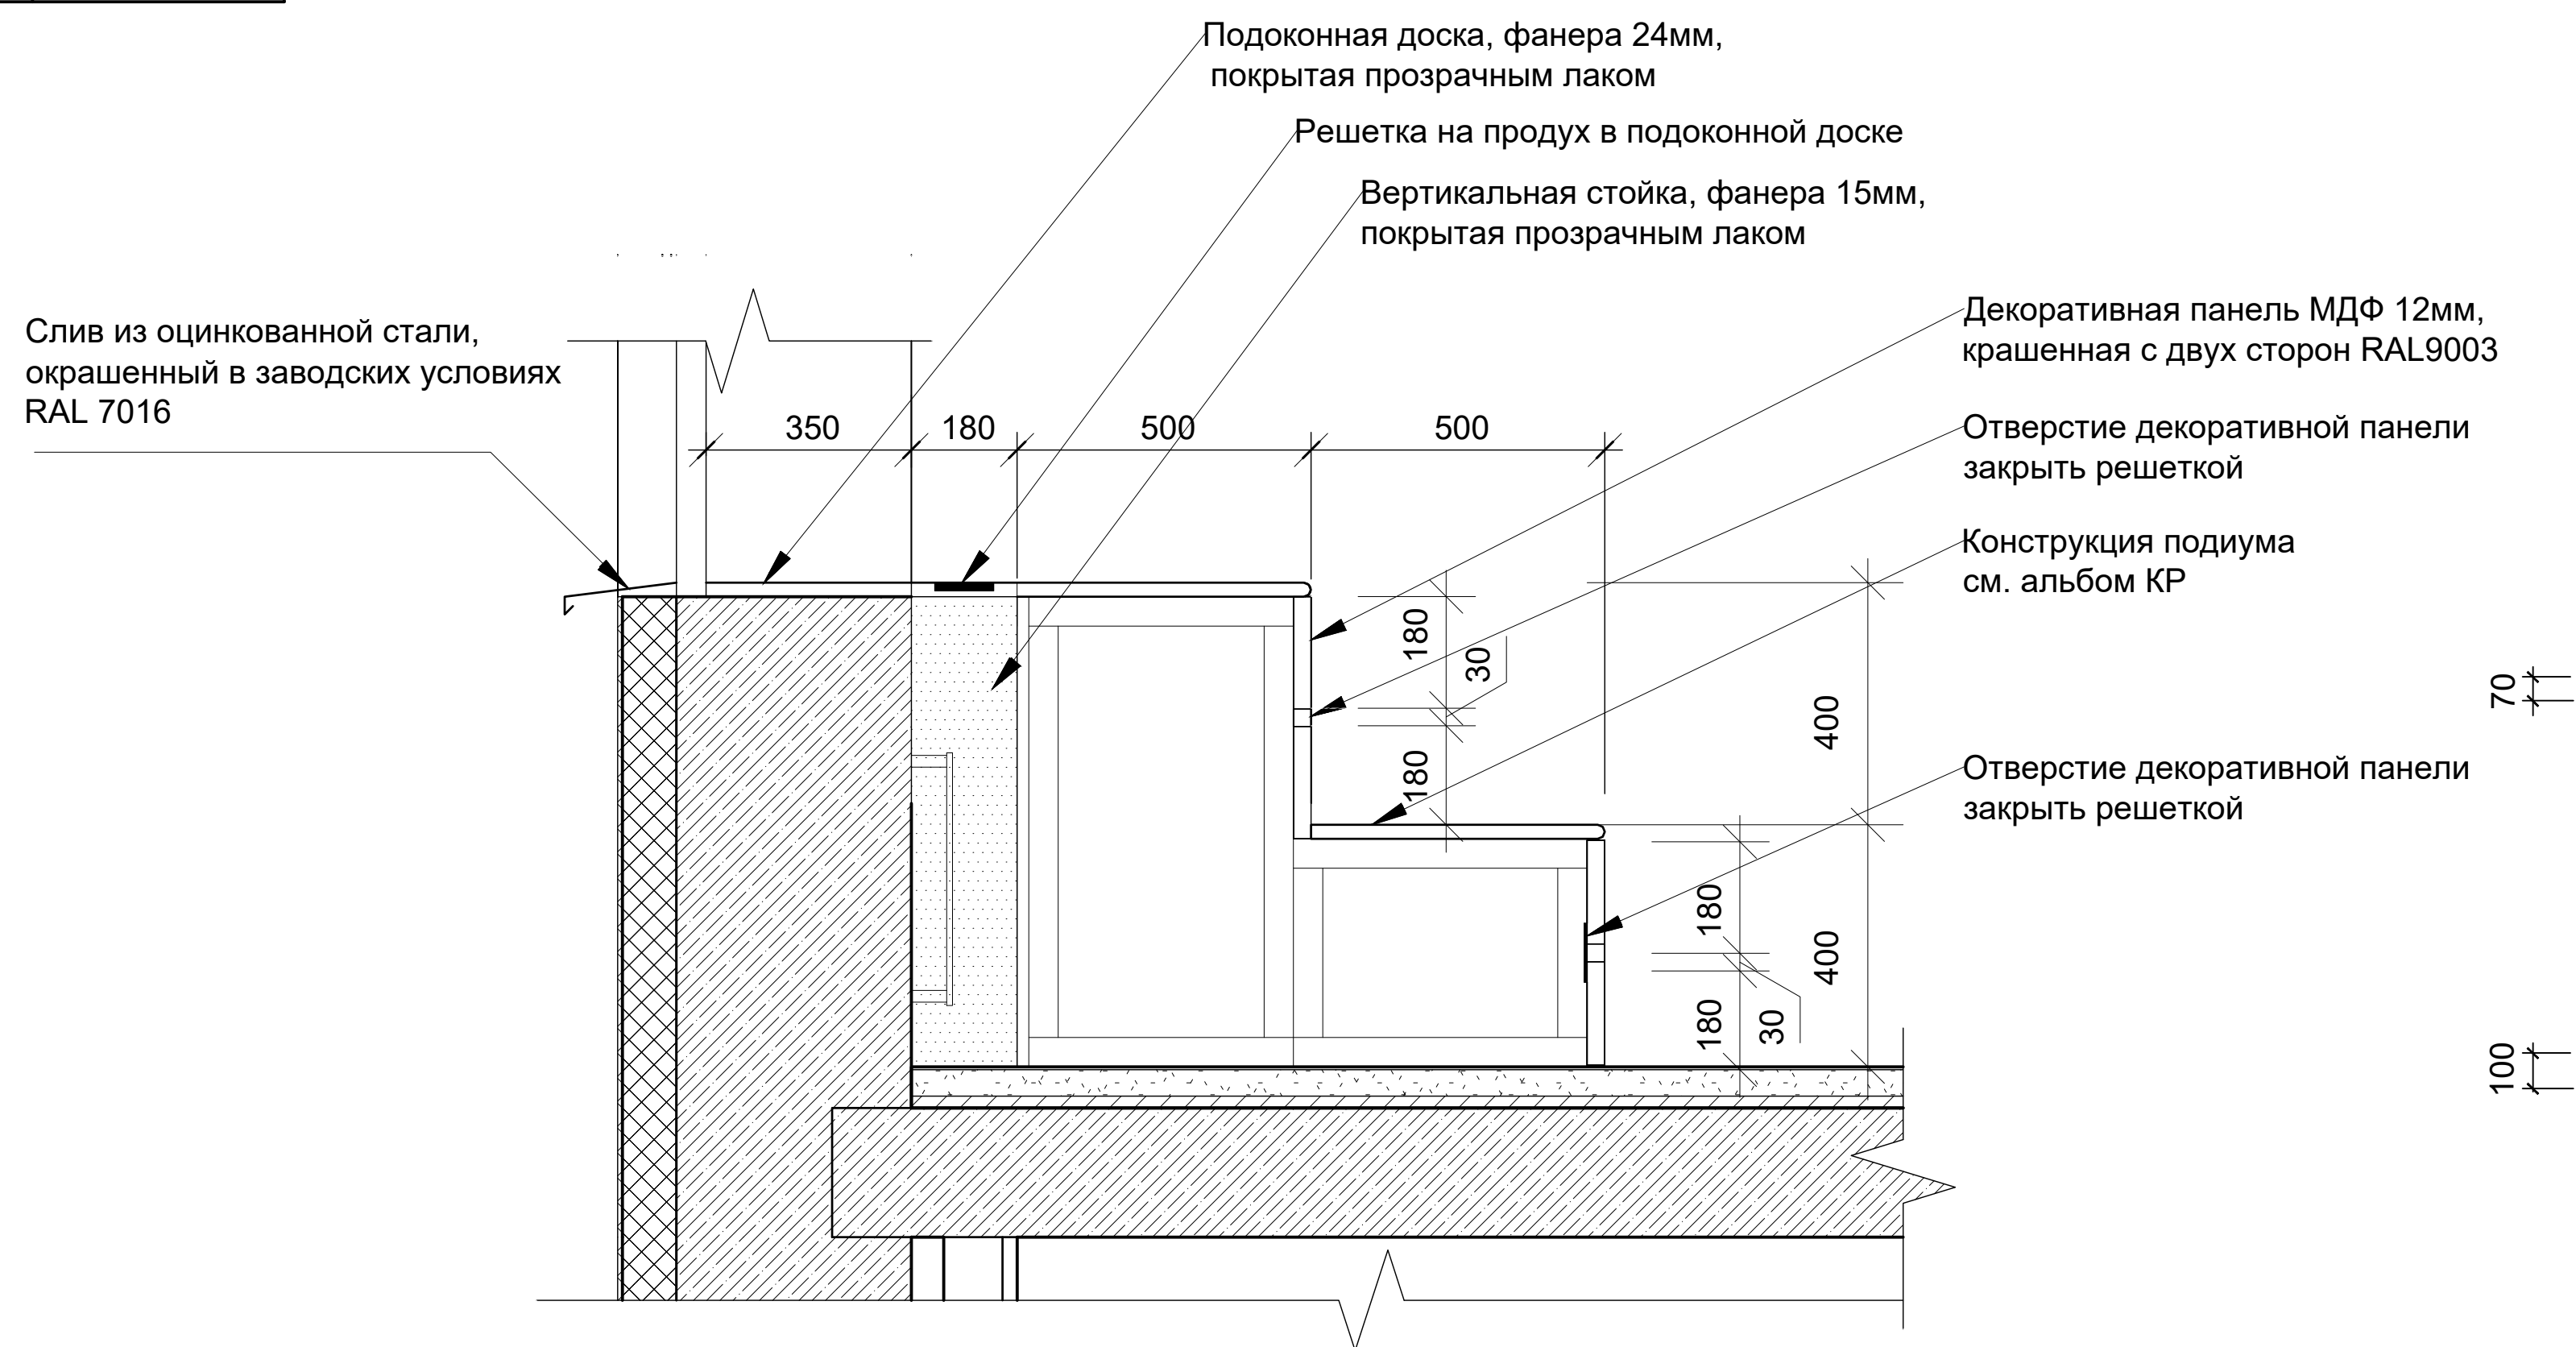
[illegible]


Схема крепления перегородок из пенобетонных блоков

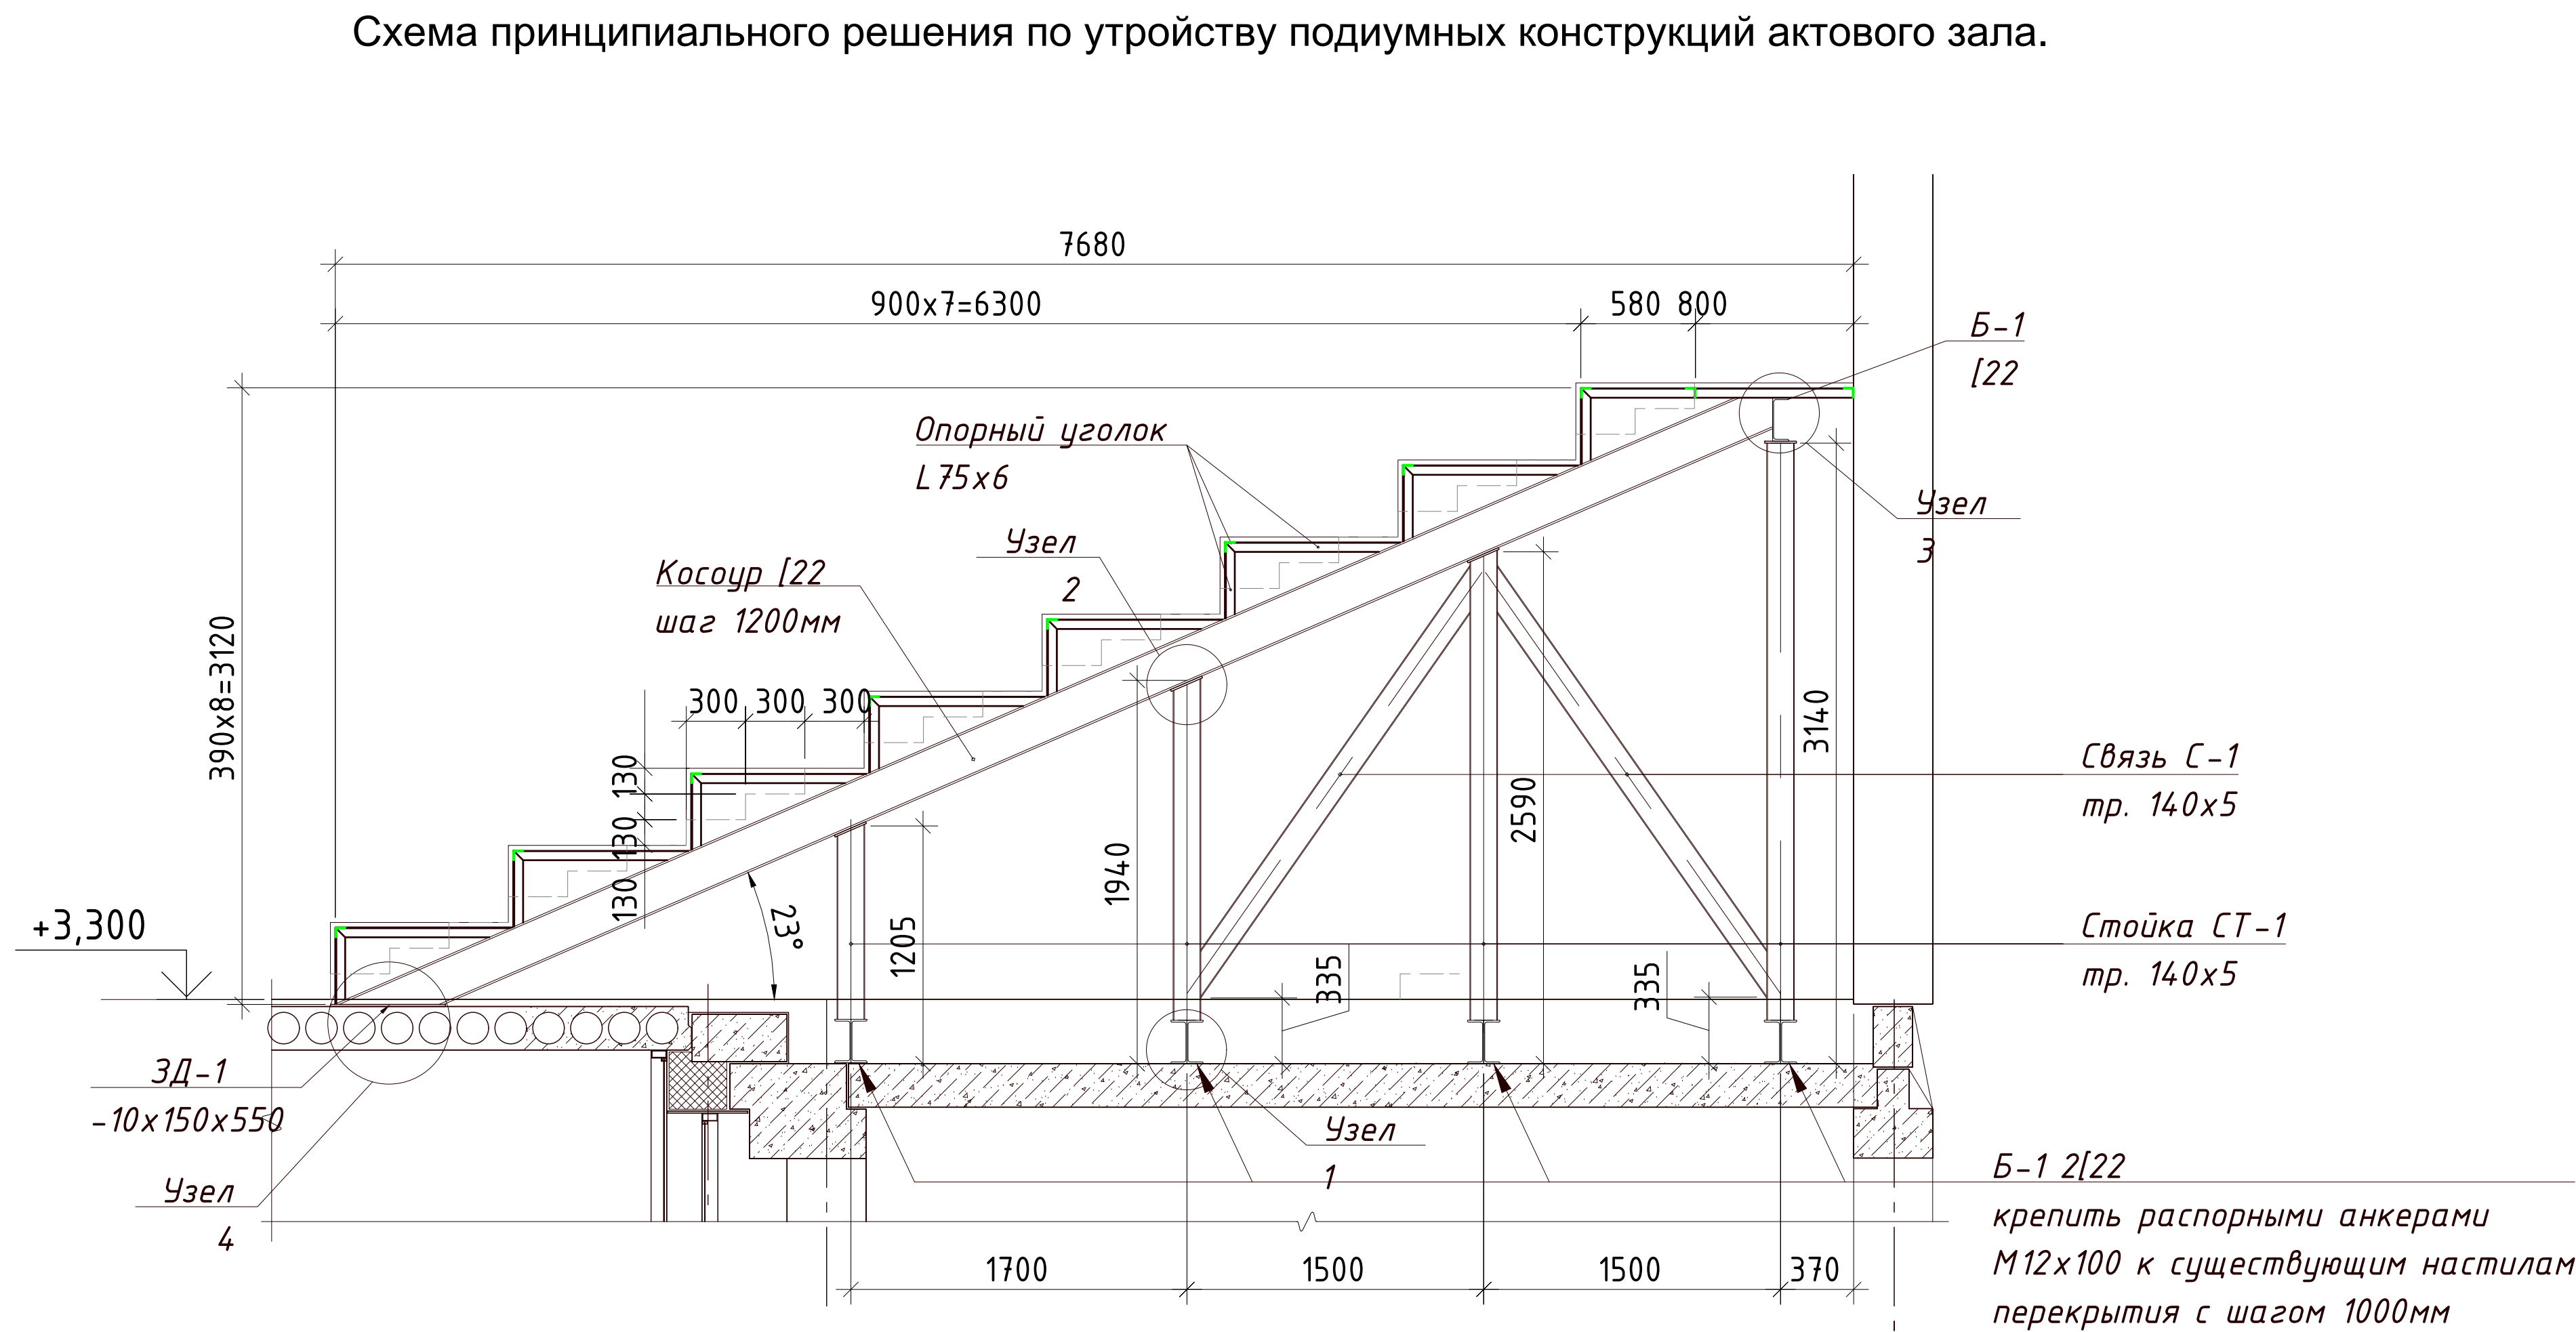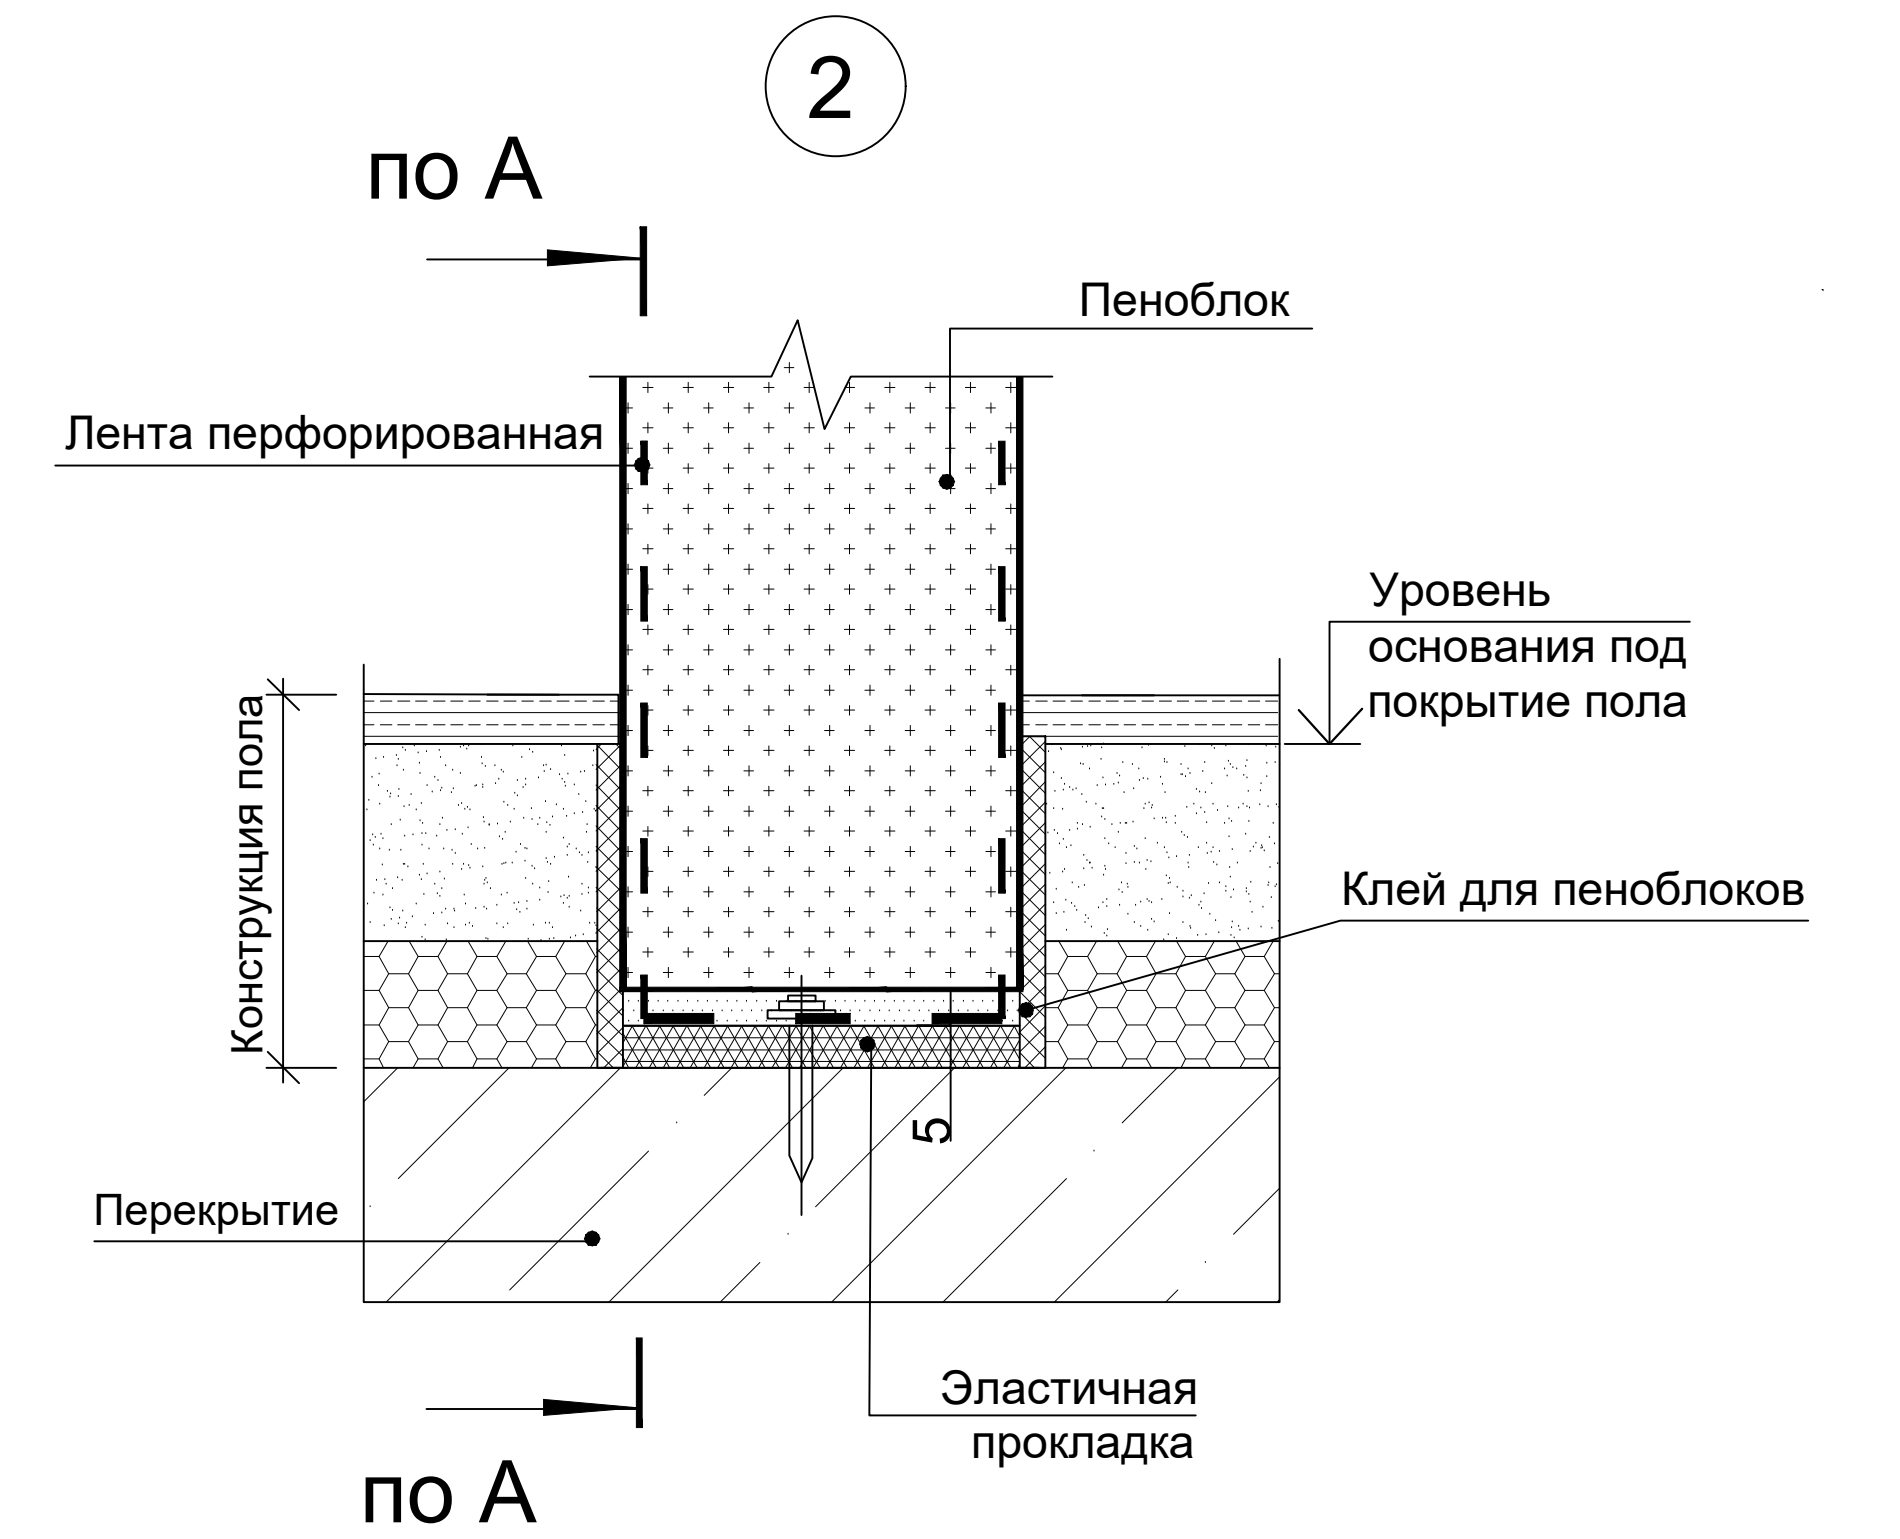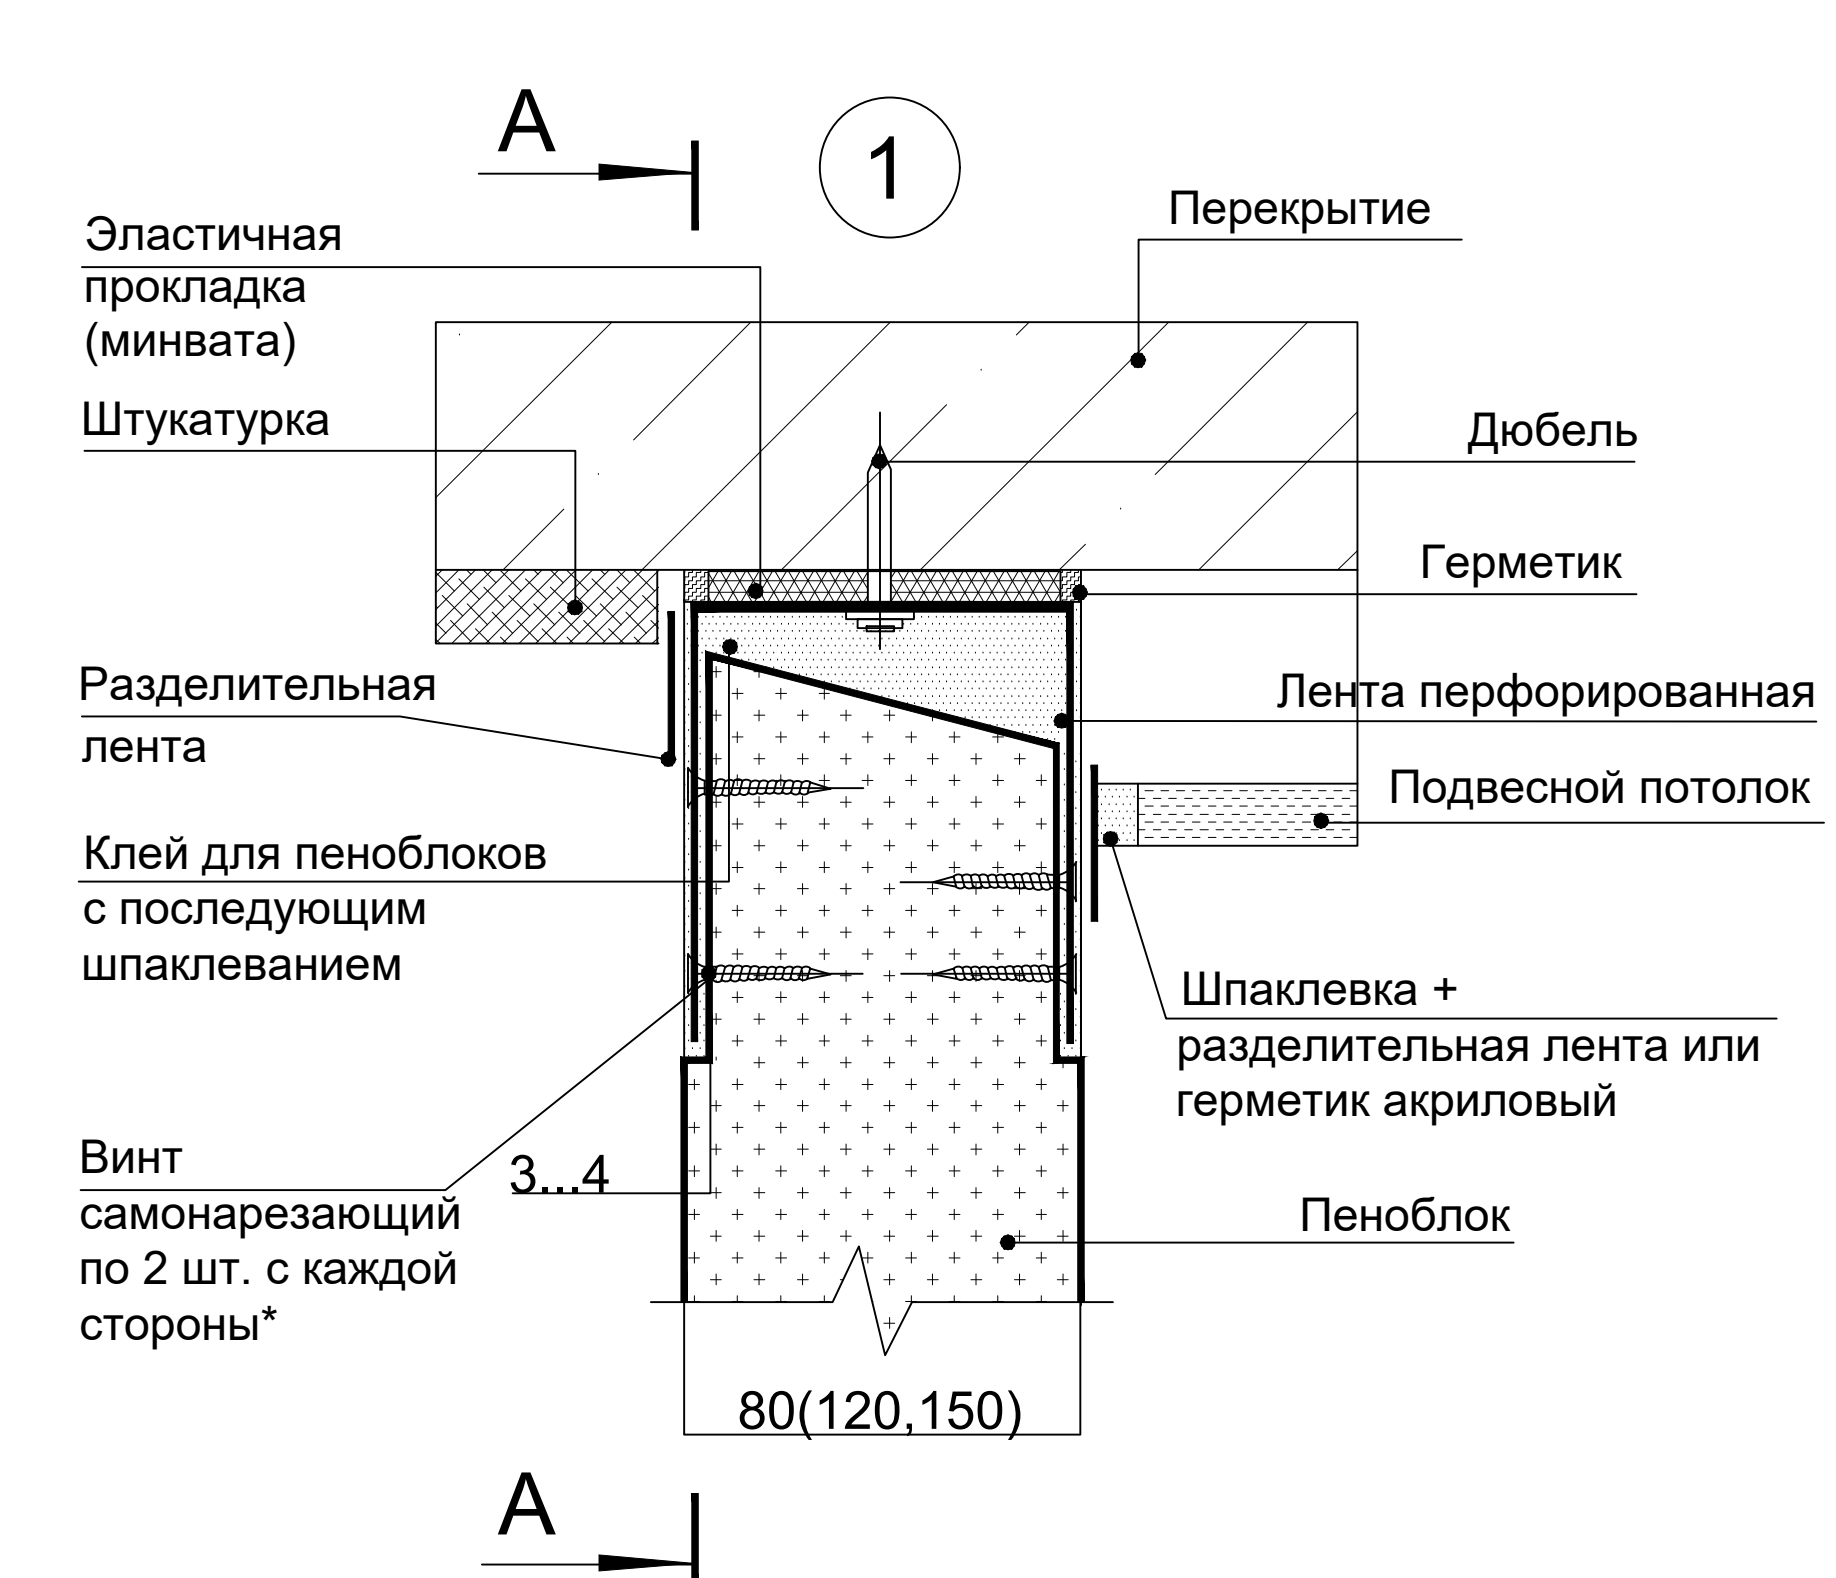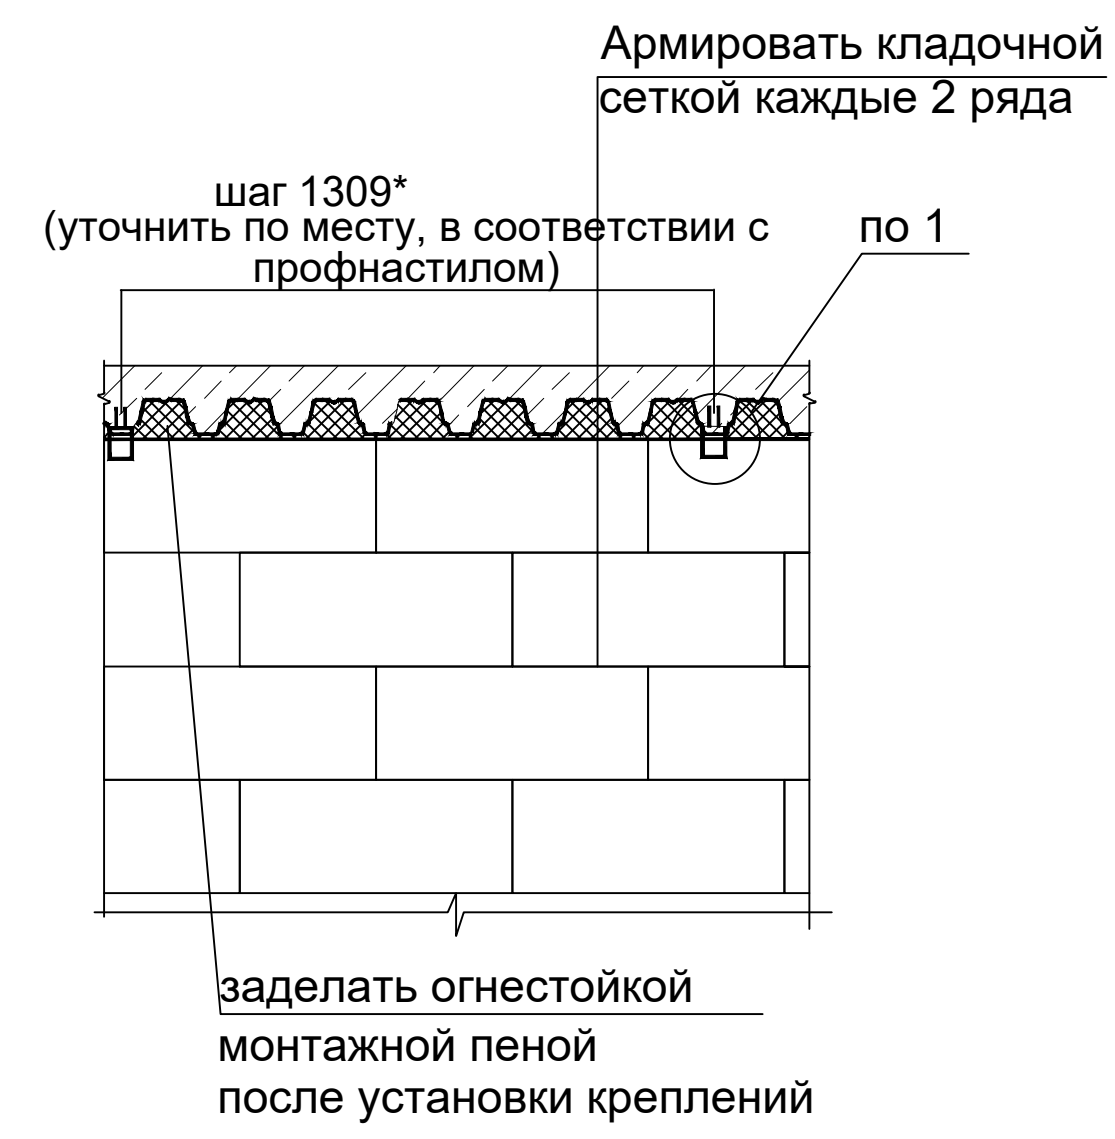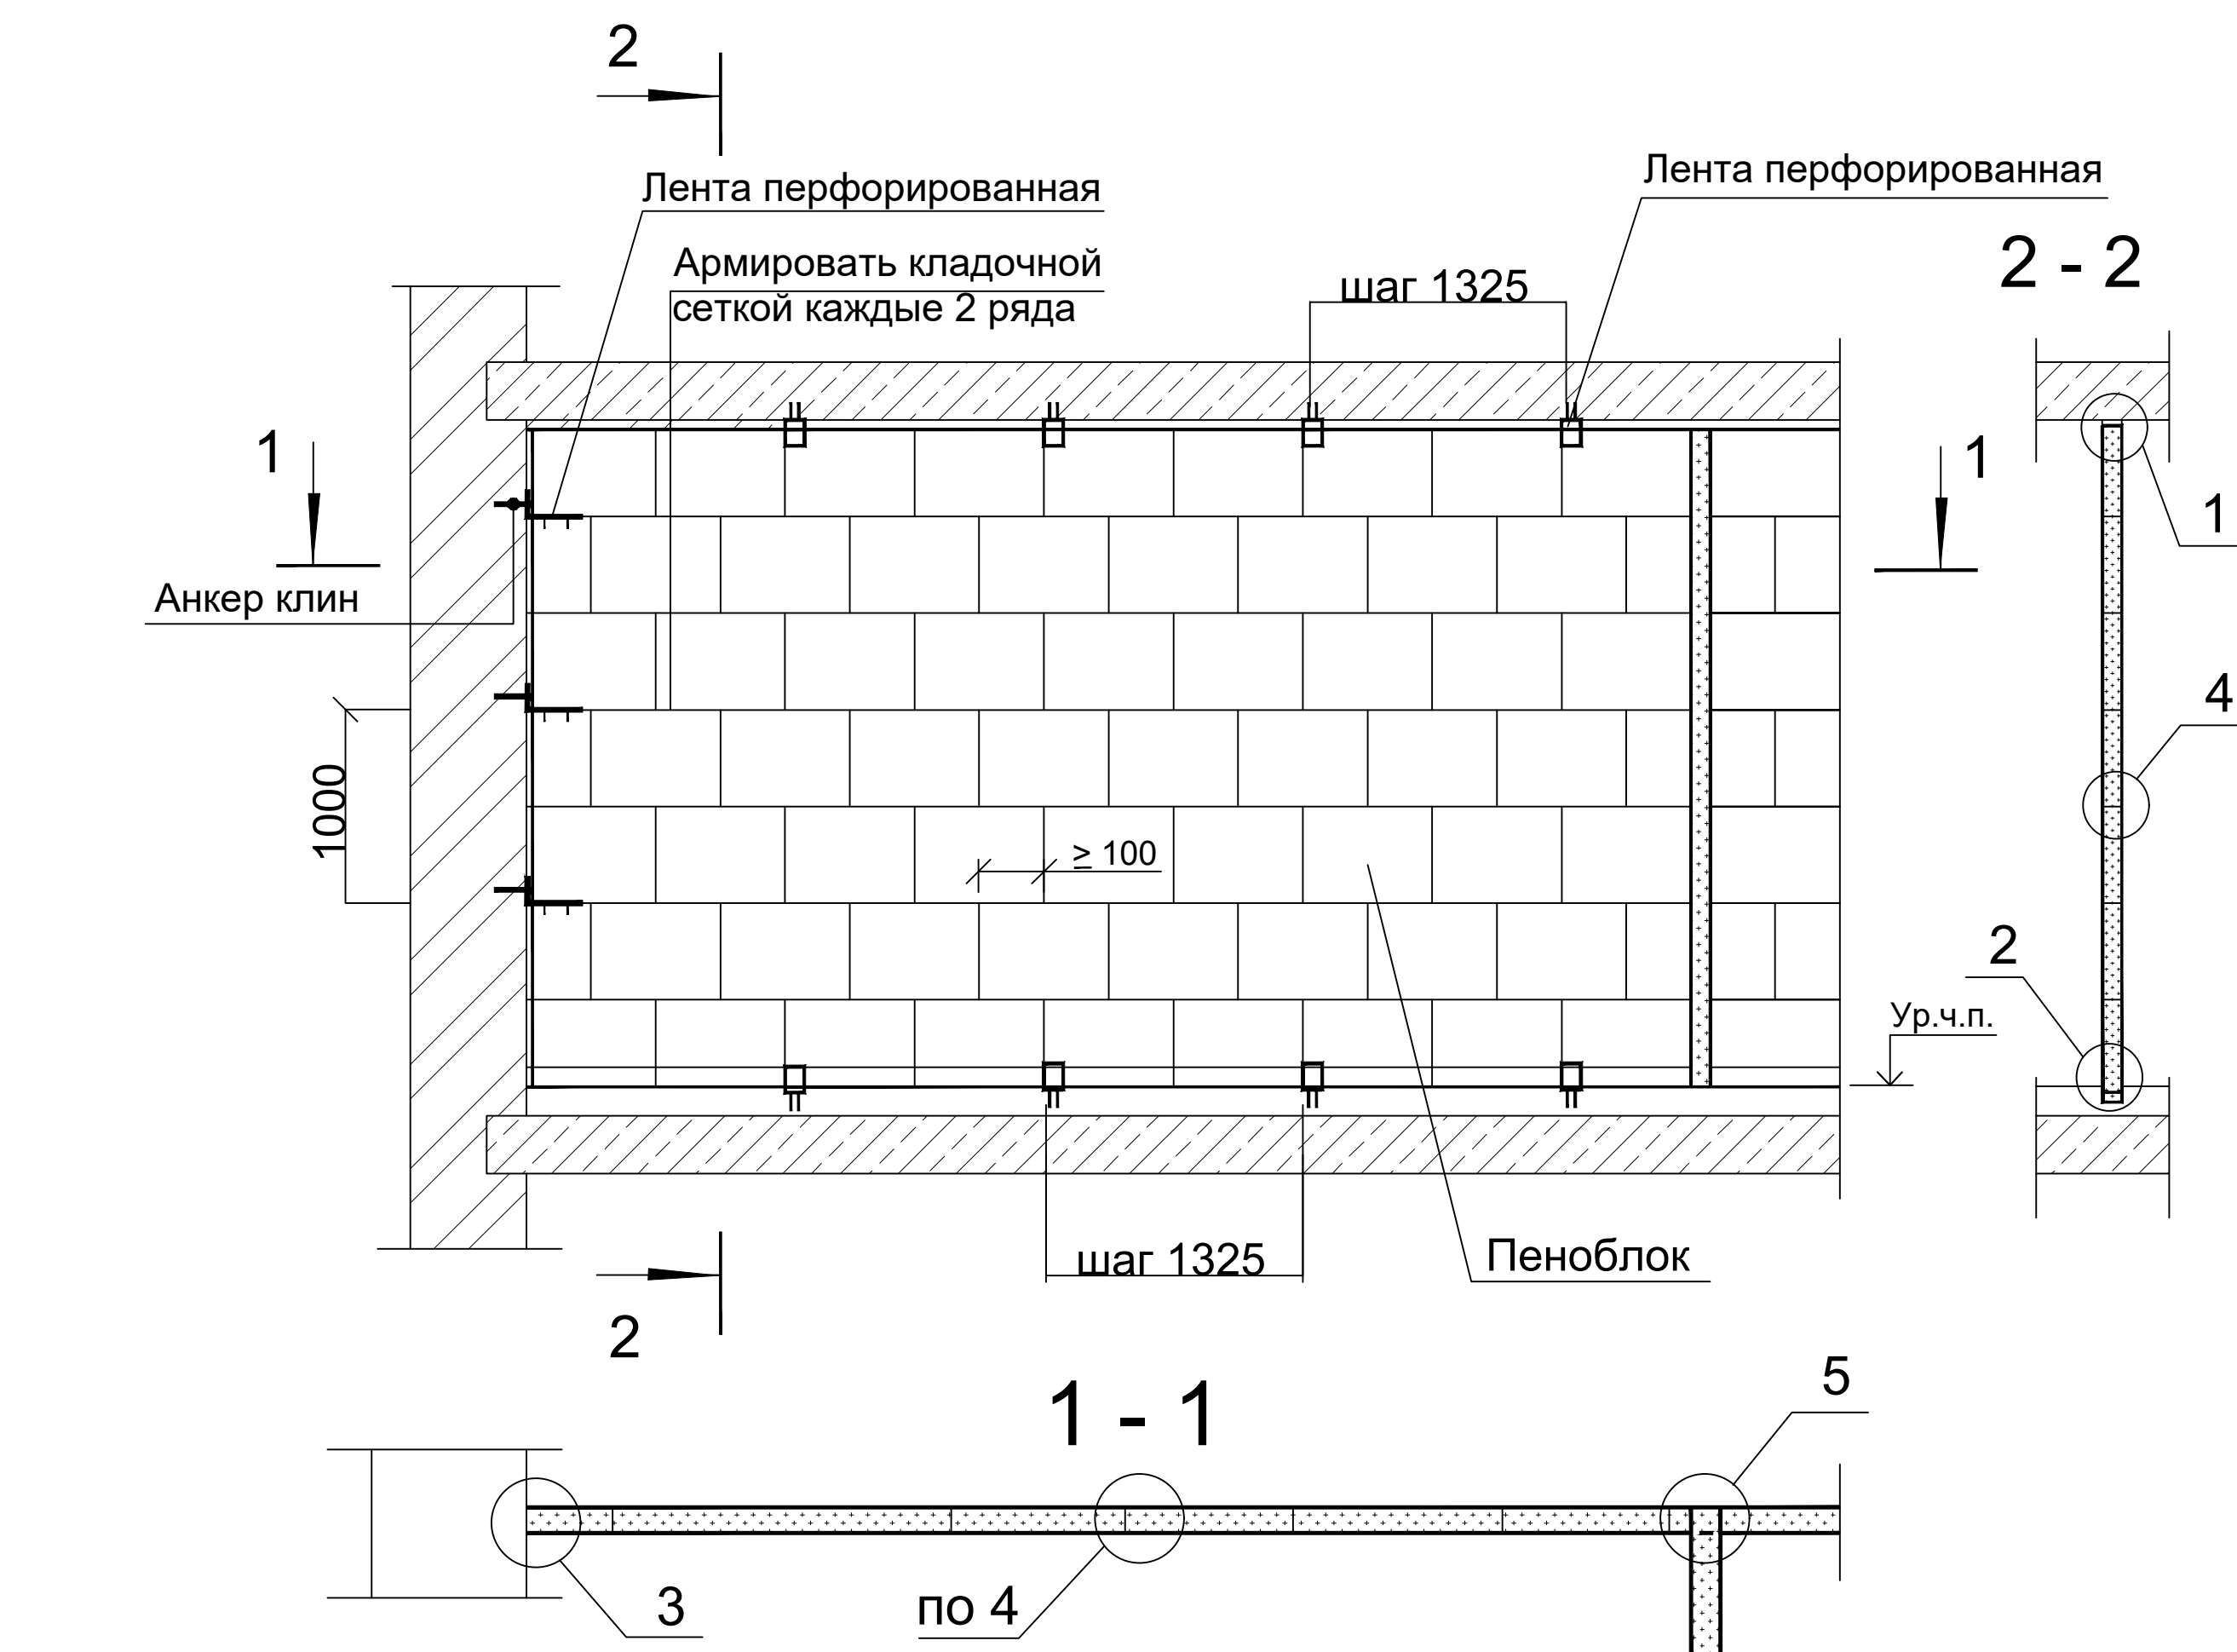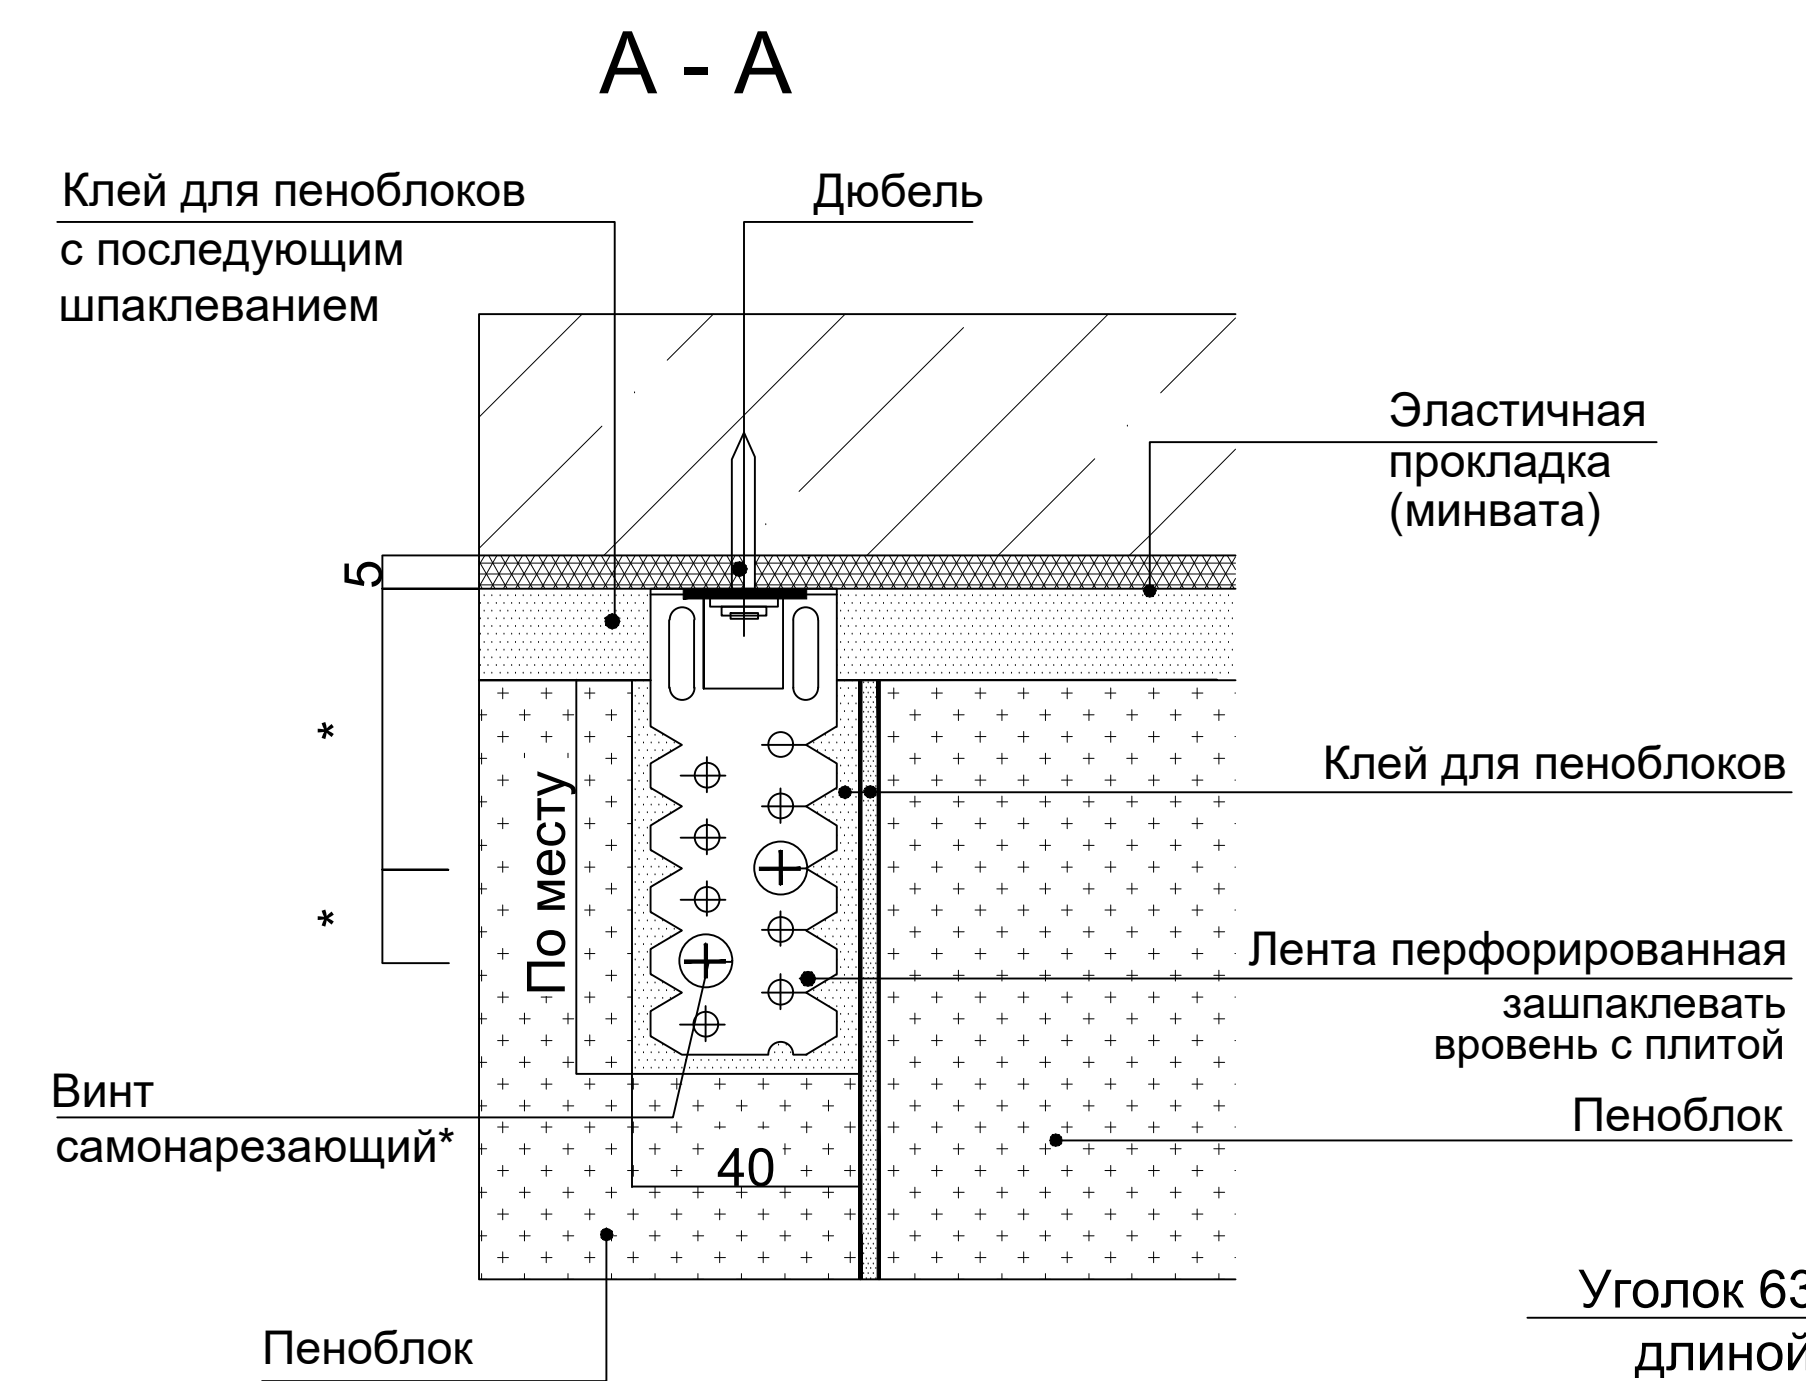



A - A
(Для крепления к профнастилу)

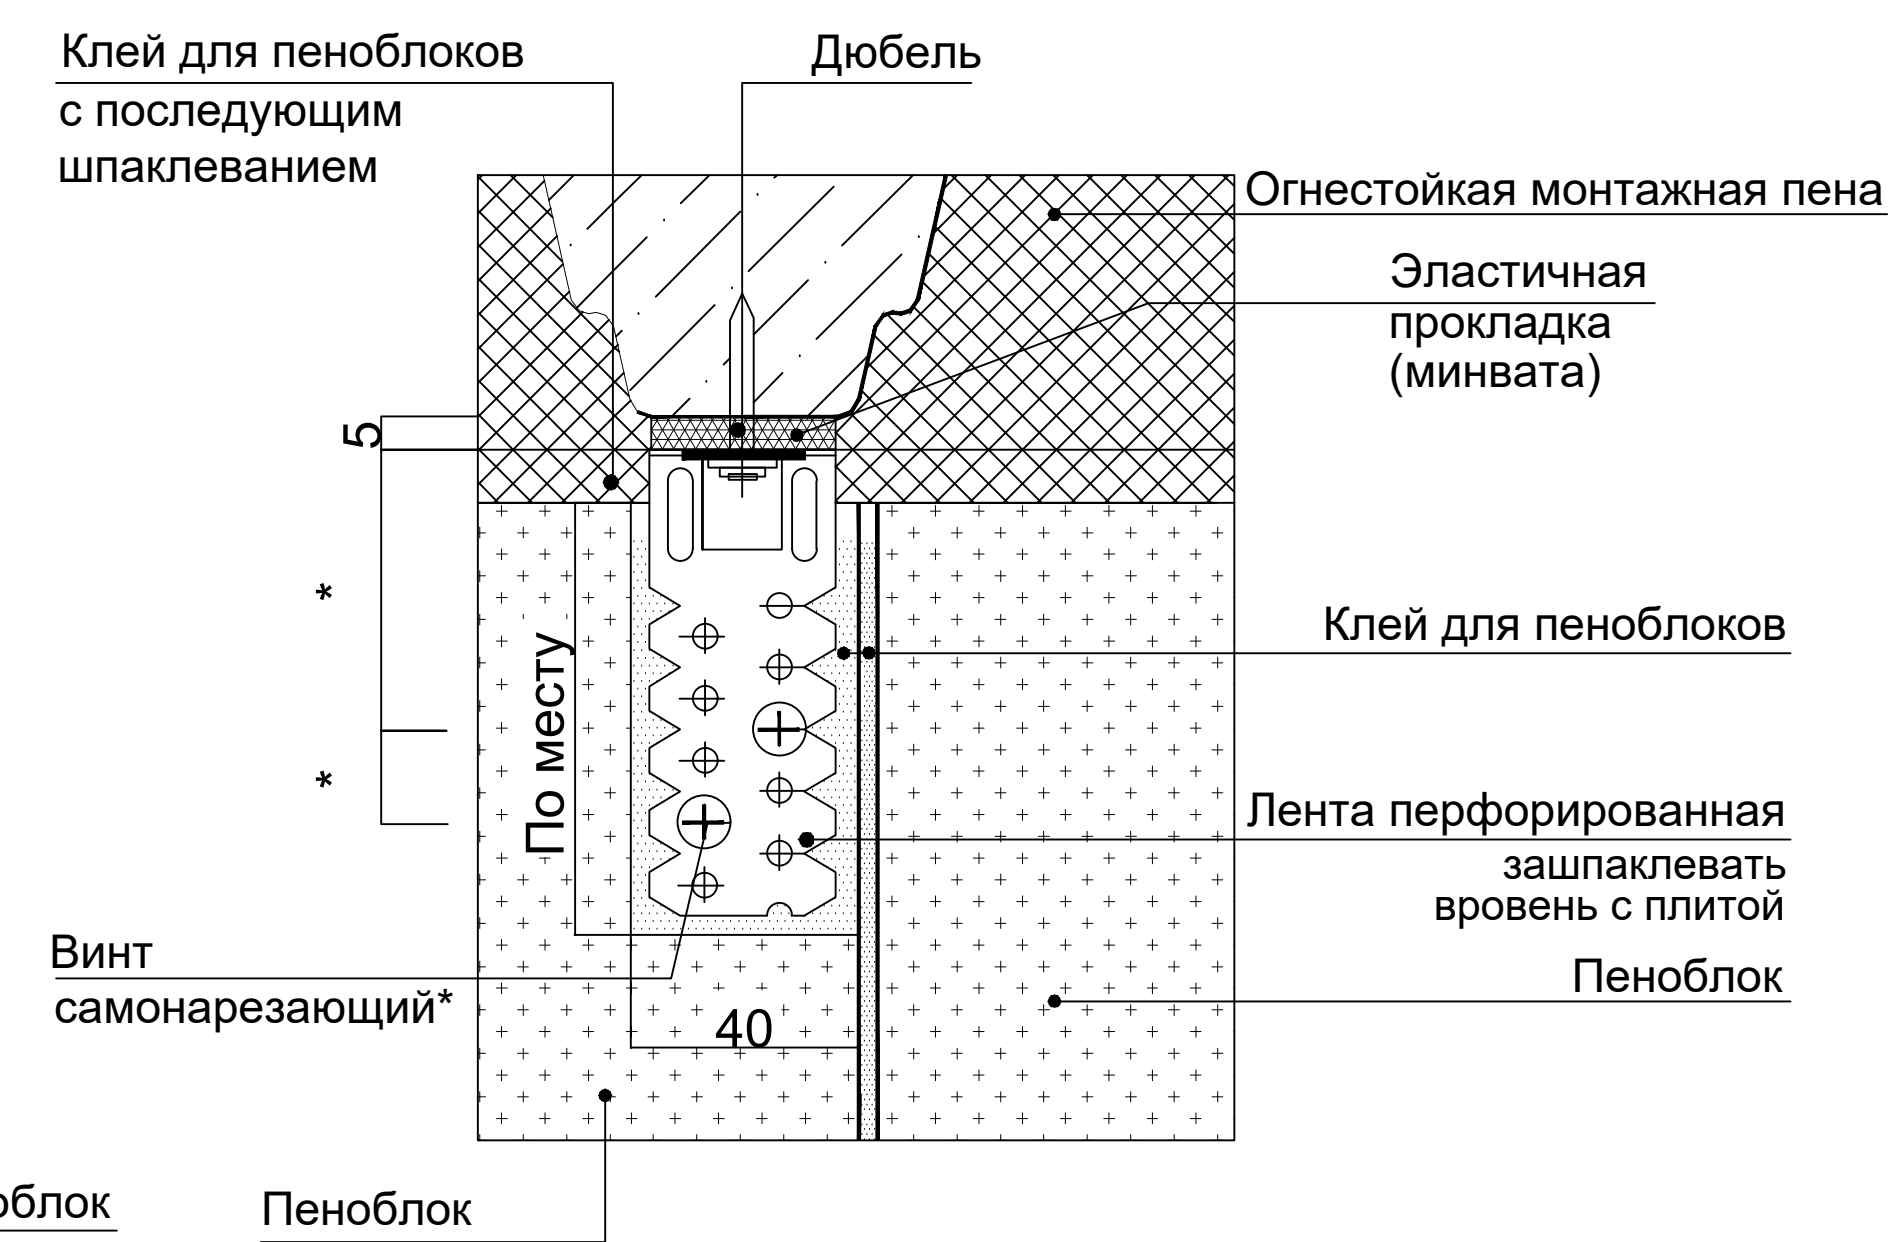



Крепление к металлической балке

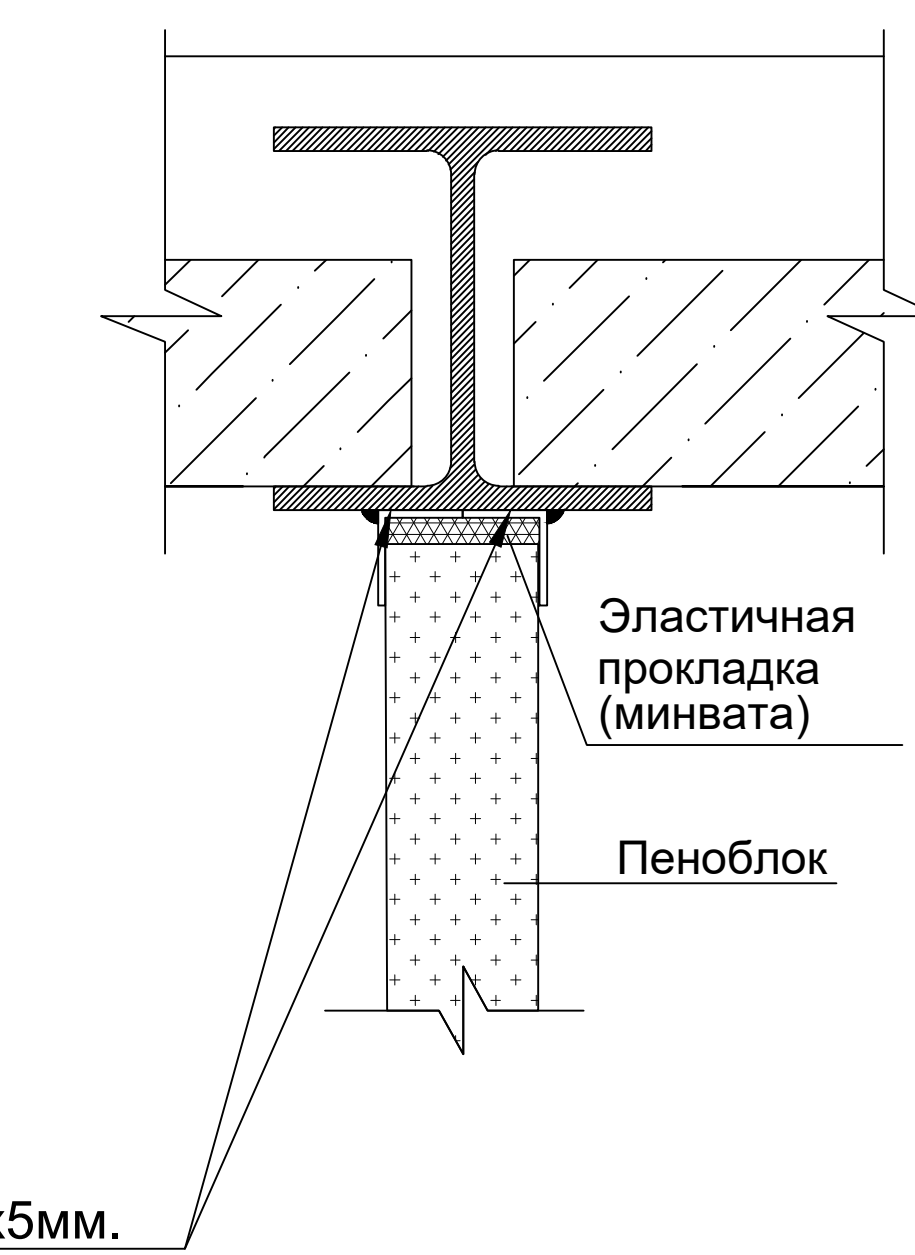

Уголок 63х63х5мм.
длинной 100мм
с шагом 1500мм
приварить
к металлической балке
перекрытия

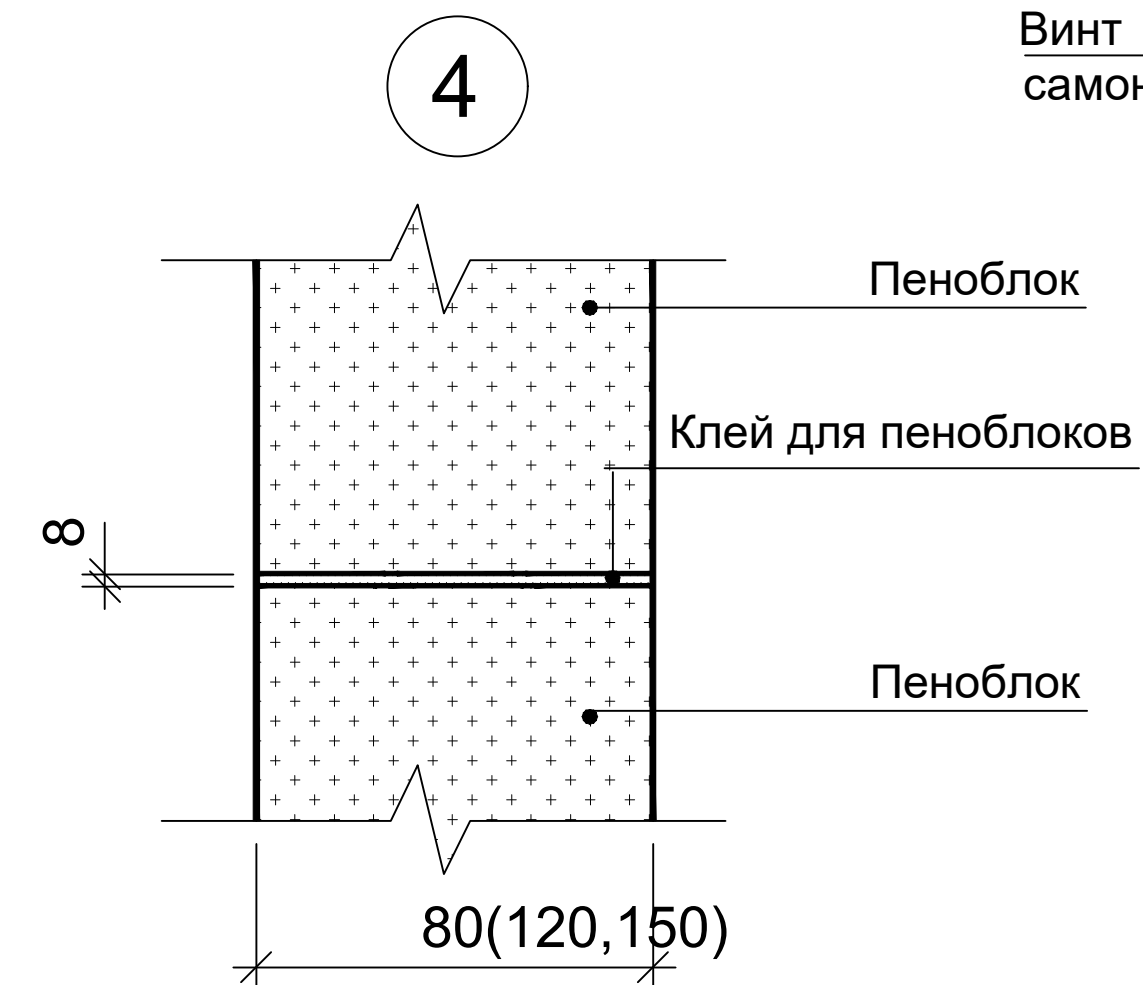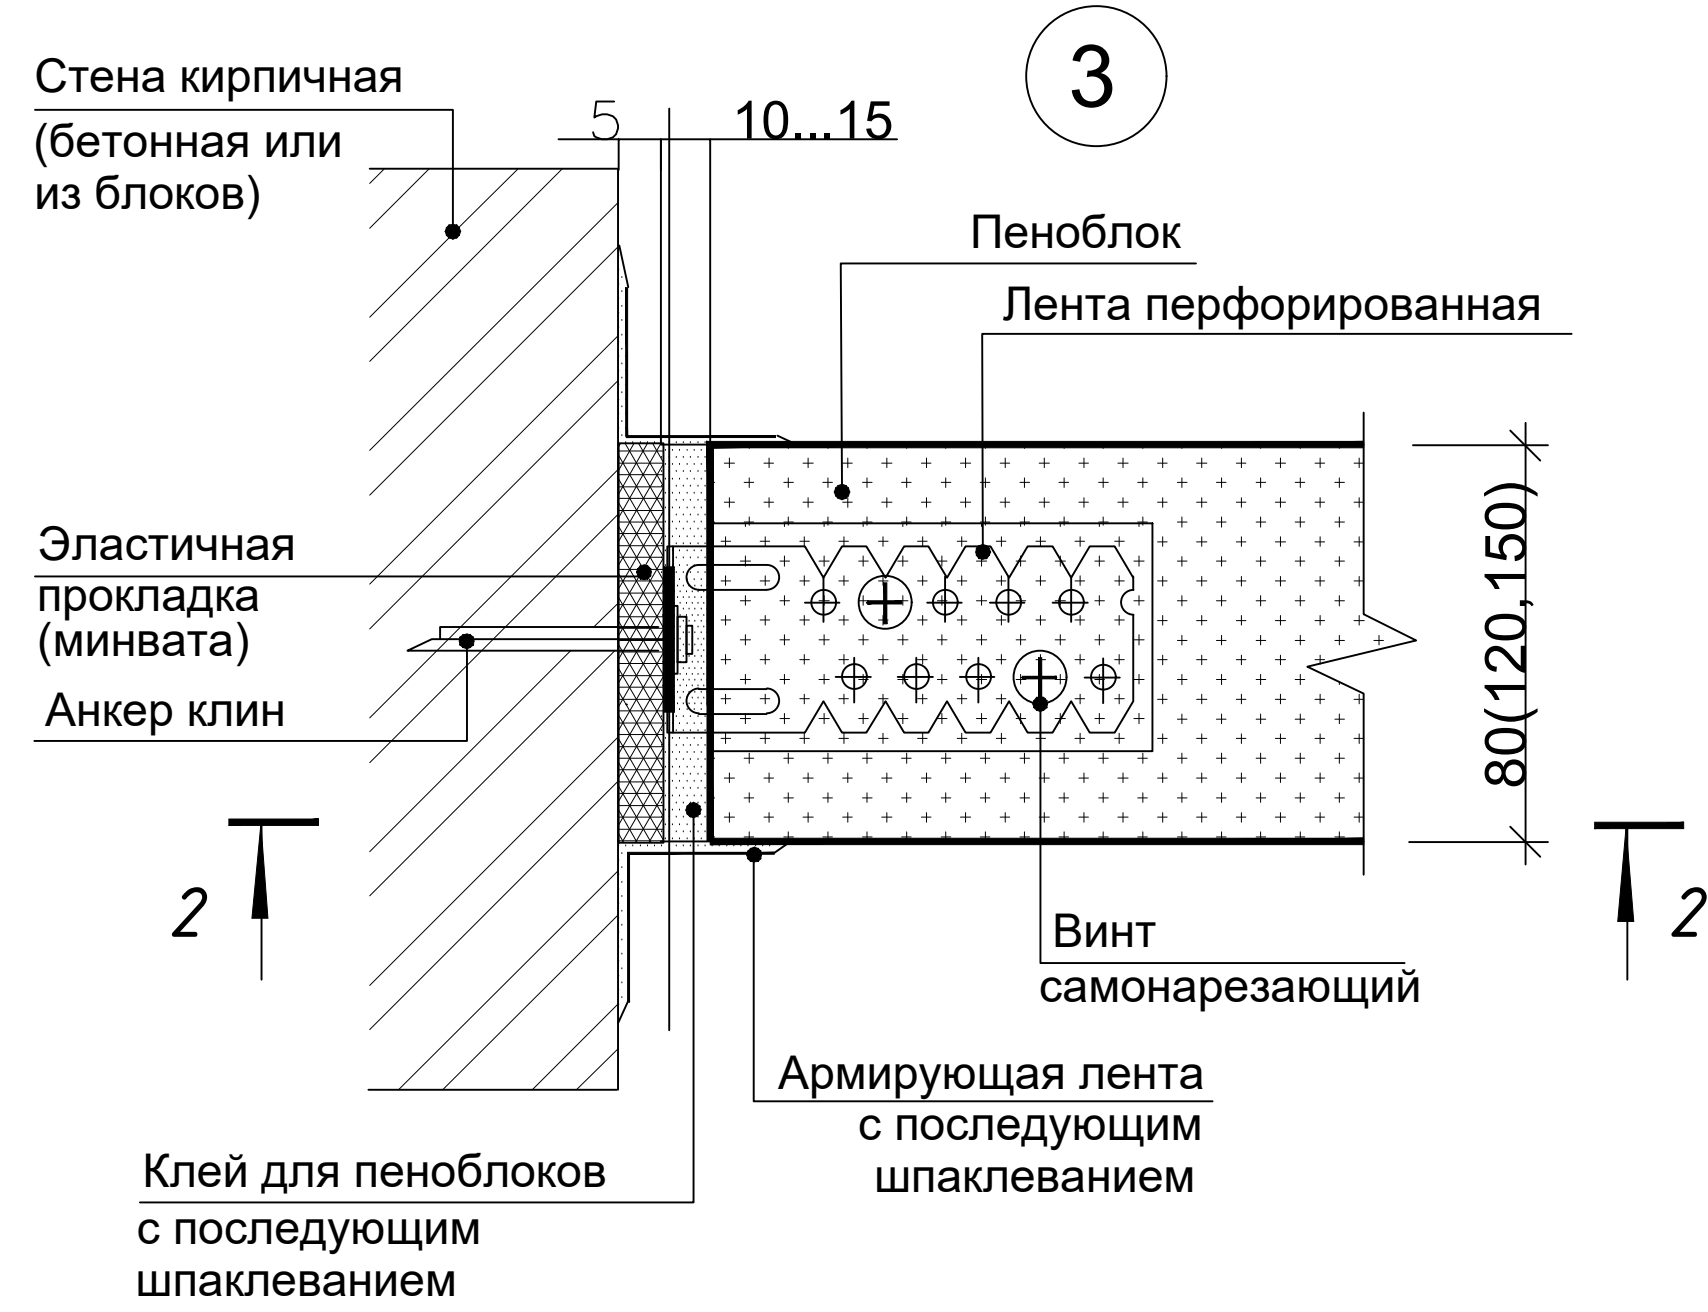


Прямой подвес С1 / перфолента

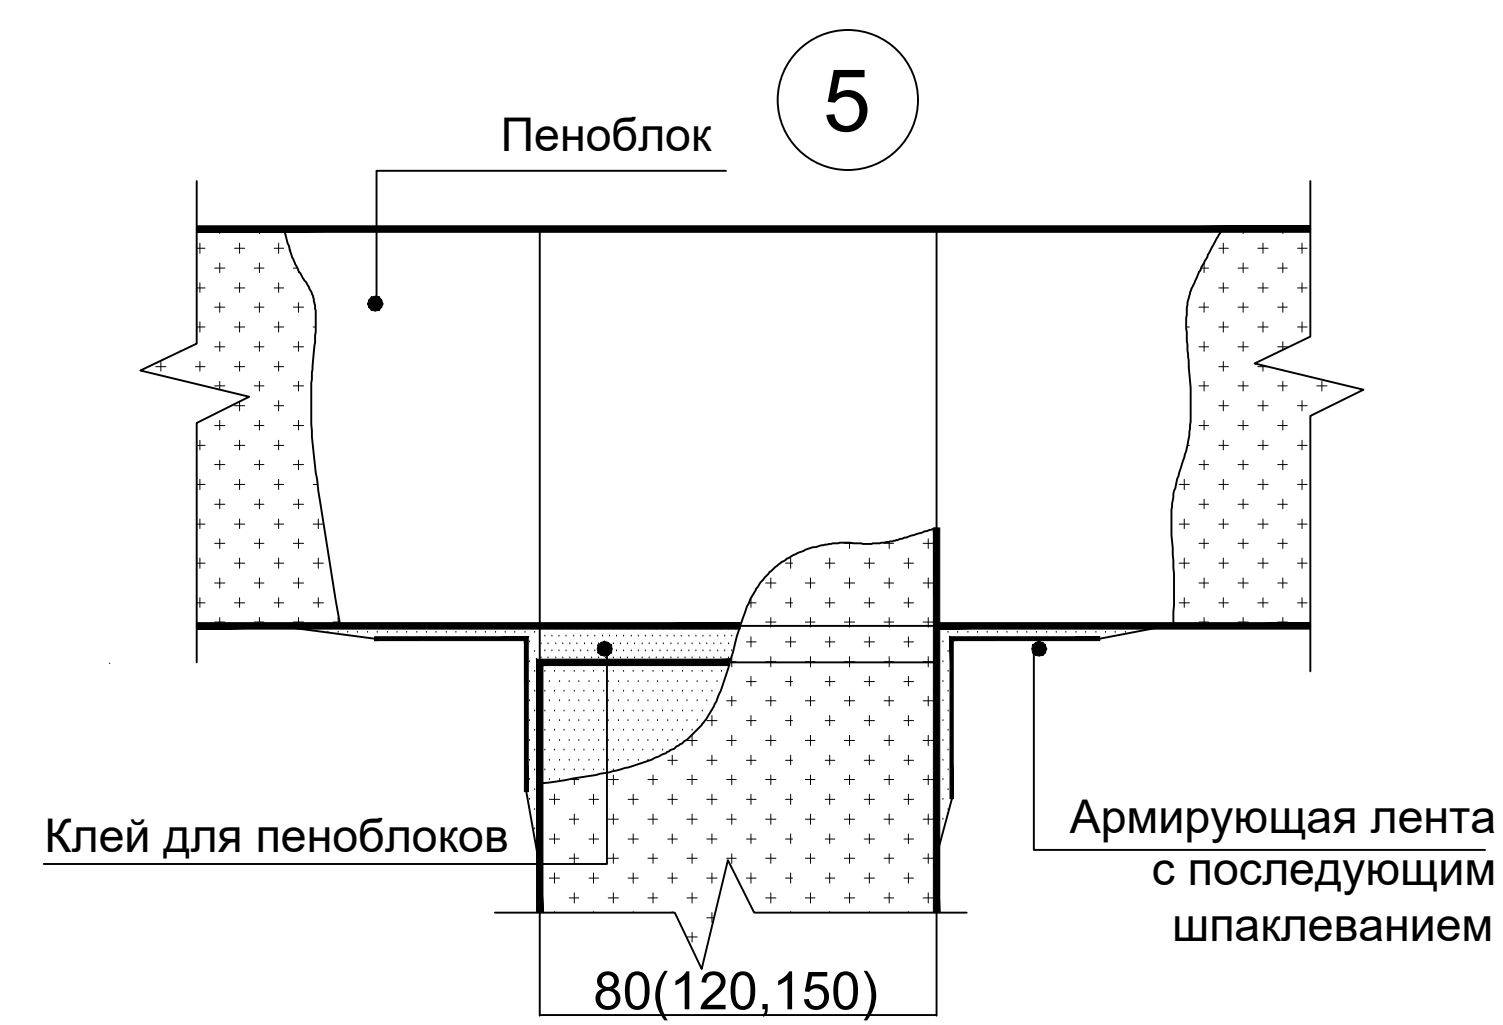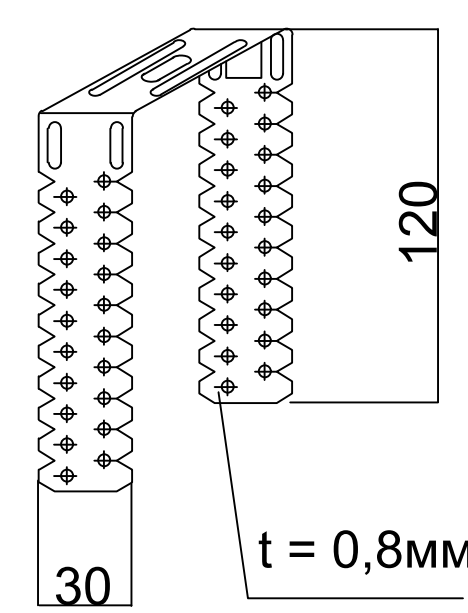[illegible]


[illegible][illegible]

№	Марка	Обозначение	Наименование ограждения	Длина ограждения	Высота ограждения	Кол-во	Примечание
	Or-44	ГОСТ 25772-2021	Ограждение лестницы из нержавеющей стали AISI 304, h=1200мм, h=900мм, Ø50 мм, h=500мм, Ø50 мм, с не травмирующим окончанием вертикальное заполнение - труба Ø16 с шагом 100мм	7015,53	1200	1	
	Or-45	ГОСТ 25772-2021	Ограждение лестницы из нержавеющей стали AISI 304, h=1200мм, h=900мм, Ø50 мм, h=500мм, Ø50 мм, с не травмирующим окончанием вертикальное заполнение - труба Ø16 с шагом 100мм	7025,753	1200	1	
	Or-46	ГОСТ 25772-2021	Ограждение лестницы из нержавеющей стали AISI 304, h=1200мм, h=900мм, Ø50 мм, h=500мм, Ø50 мм, с не травмирующим окончанием вертикальное заполнение - труба Ø16 с шагом 100мм	7040,327	1200	1	
	Or-47	ГОСТ 25772-2021	Ограждение окна из нержавеющей стали AISI 304, h=1200мм, вертикальное заполнение - труба Ø16 с шагом 100мм	1736,27	1200	1	
	Or-48	ГОСТ 25772-2021	Ограждение окна из нержавеющей стали AISI 304, h=1200мм, вертикальное заполнение - труба Ø16 с шагом 100мм	1736,27	1200	1	
	Or-49	ГОСТ 25772-2021	Ограждение пандуса из нержавеющей стали AISI 304, h=1200мм, вертикальное заполнение - труба Ø16 с шагом 100мм	1392,79	1200	2	
	Or-50	ГОСТ 25772-2021	Ограждение пандуса из нержавеющей стали AISI 304, h=1200мм, вертикальное заполнение - труба Ø16 с шагом 100мм	1840,75	1150	3	
	Or-51	ГОСТ 25772-2021	Ограждение калитки из нержавеющей стали AISI 304, h=1200мм, вертикальное заполнение - труба Ø16 с шагом 100мм	900	1150	1	
	Пс-1	ГОСТ 25772-2021	Перила (крепление к стене) из нержавеющей стали AISI 304, h=900мм, h=500мм	3024,5	1200	2	
	Пс-2	ГОСТ 25772-2021	Перила (крепление к стене) из нержавеющей стали AISI 304, h=900мм, h=500мм,	7265,6	1200	2	
	Пс-3	ГОСТ 25772-2021	Перила (крепление к стене) из нержавеющей стали AISI 304, h=900мм, h=500мм,	7379,16	1200	4	
	Пс-4	ГОСТ 25772-2021	Перила (крепление к стене) из нержавеющей стали AISI 304, h=900мм, h=500мм,	63520,488	1200	28	


Ограждения для входных групп, эвакуационных выходов

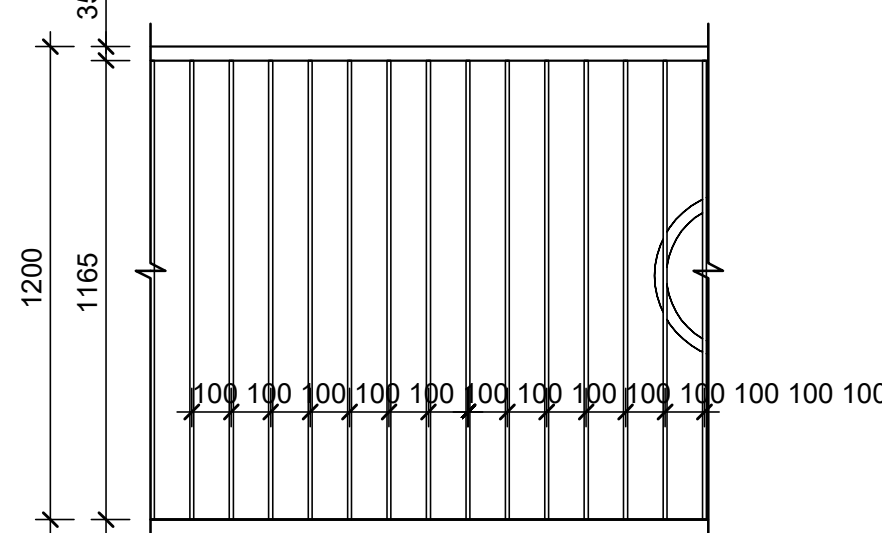


Ограждения для пандуса

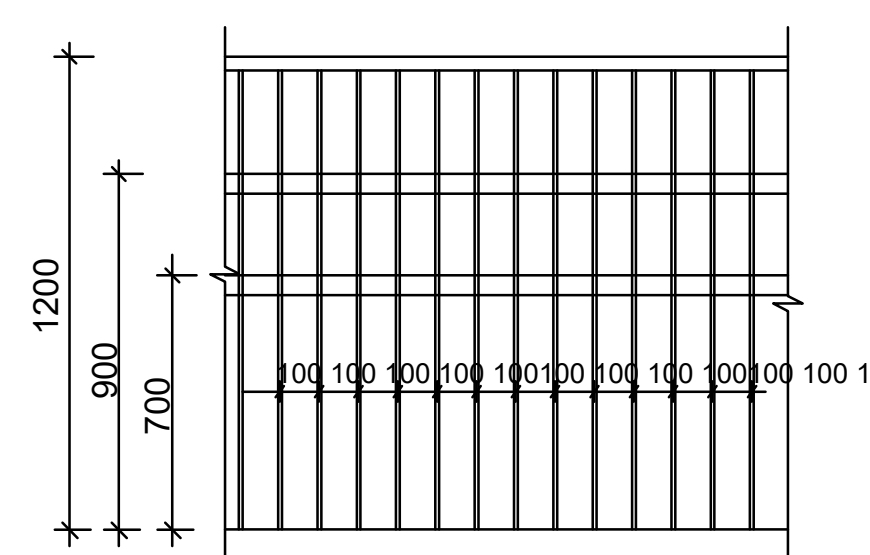

Ограждения для выходов из подвалов

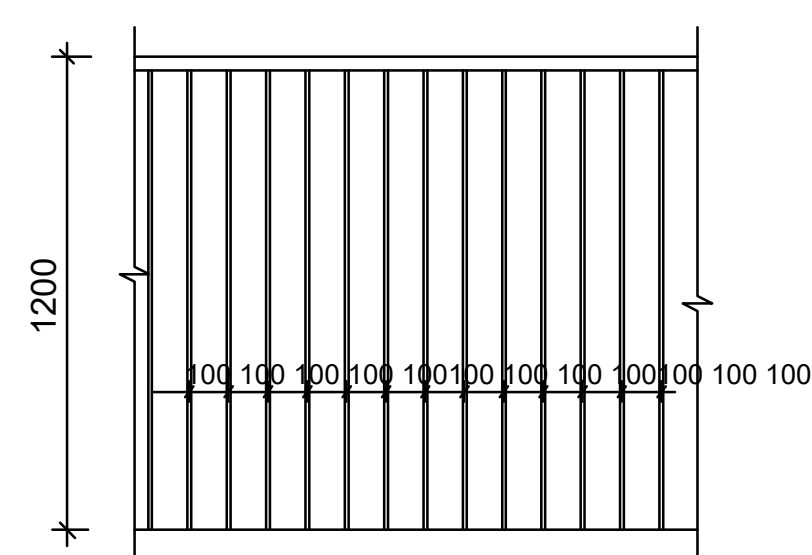

Ограждения для лестичных клеток


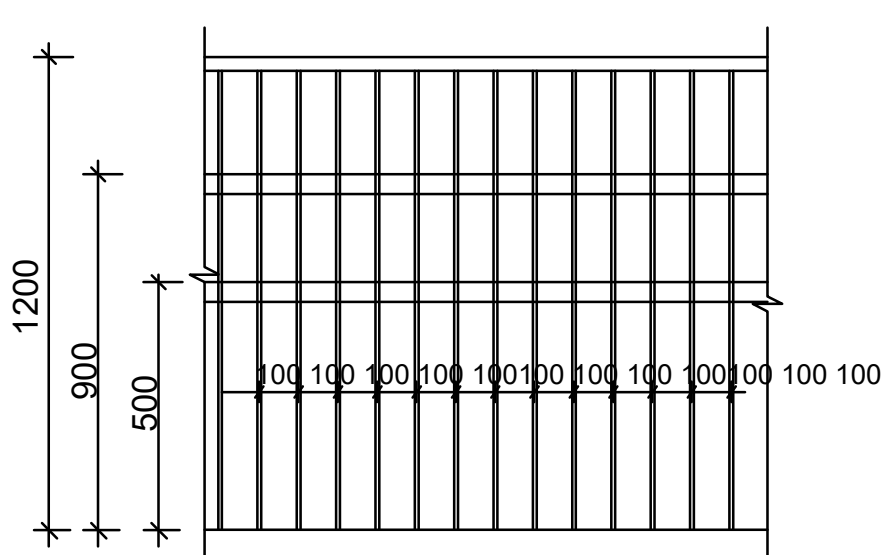


						205-25-AP		
Исполнительный ремонт здания Государственного бюджетного общеобразовательного учреждения школы №149, расположенного по адресу: ул. Авиаторов, д. 62, к. 7								
Изм. Контр.	Лист	Мод.	Перед.	Дато		Станд.	Лист	Листов
Разреш.	Копия		Сделка	02.25	Объемно-планировочные и архитектурные решения			
Н. контр.	Казанов			02.26	Спецификация ограждений	Объемно с оградительной ответственностью		
Гип	Гаршин			02.26		ГК "АЛЬФА-СТРОИ"		

Спецификация грязесборных решеток				
Марка	Описание	Ширина мм.	Длина мм.	Кол-во шт.
ГР-1	Монтаж системы грязезащитыДвухэтапная система грязезащиты типа МСКМеталлическая решетка с вставками из резины итрехряднойщеткой для наружного и внутреннего использования	900	1550	4
ГР-2	Монтаж системы грязезащиты. Двухэтапная система грязезащиты типа МСК Металлическая решетка для наружногоиспользования с мелким шагом сетки для установки в приямок на крыльце входной группы	900	1450	6

ГР-1









ГР-2





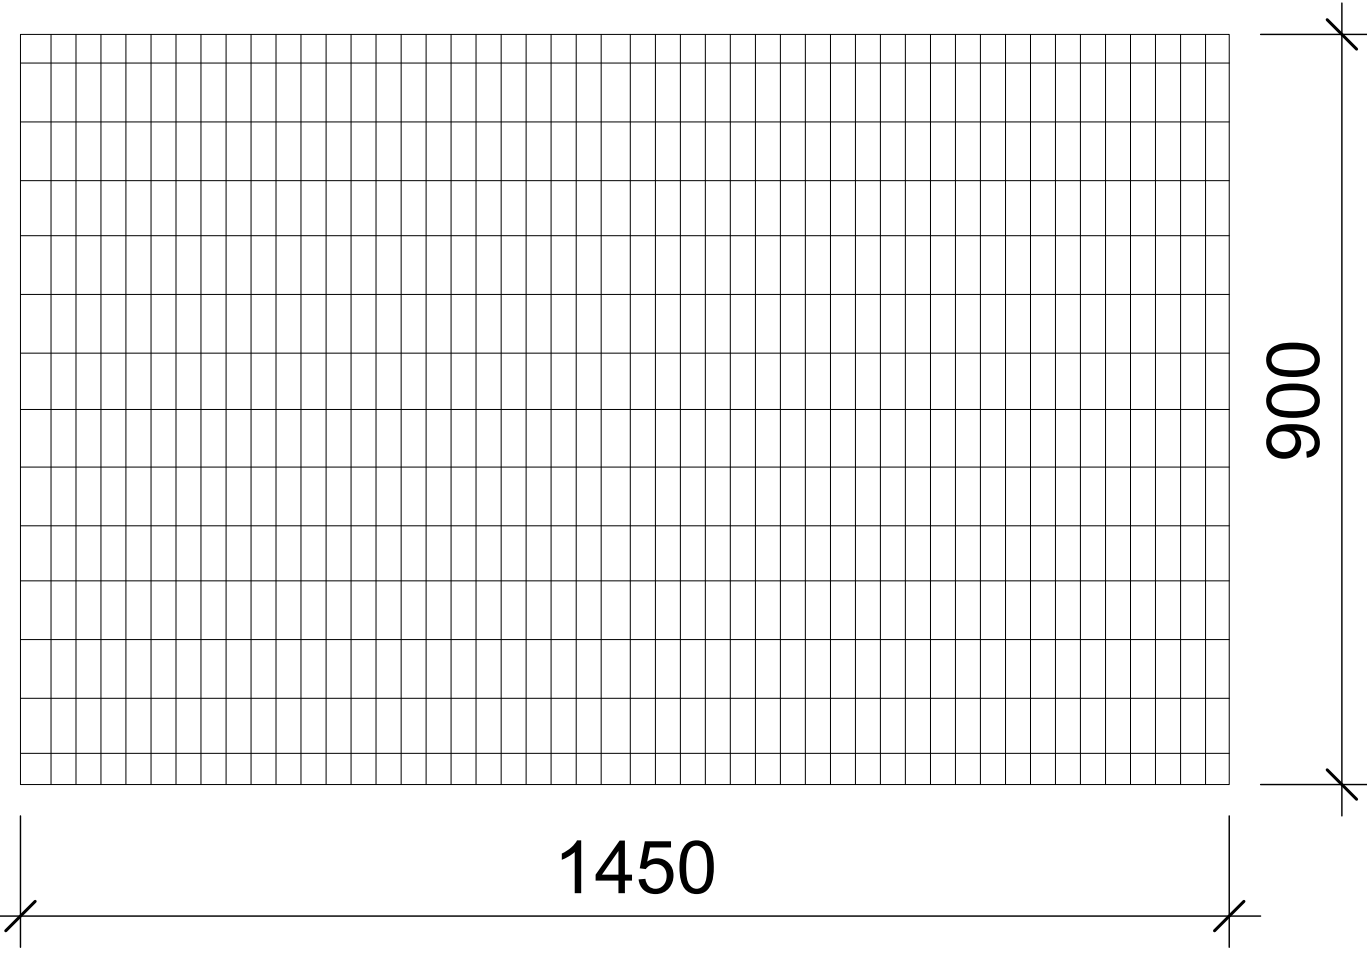
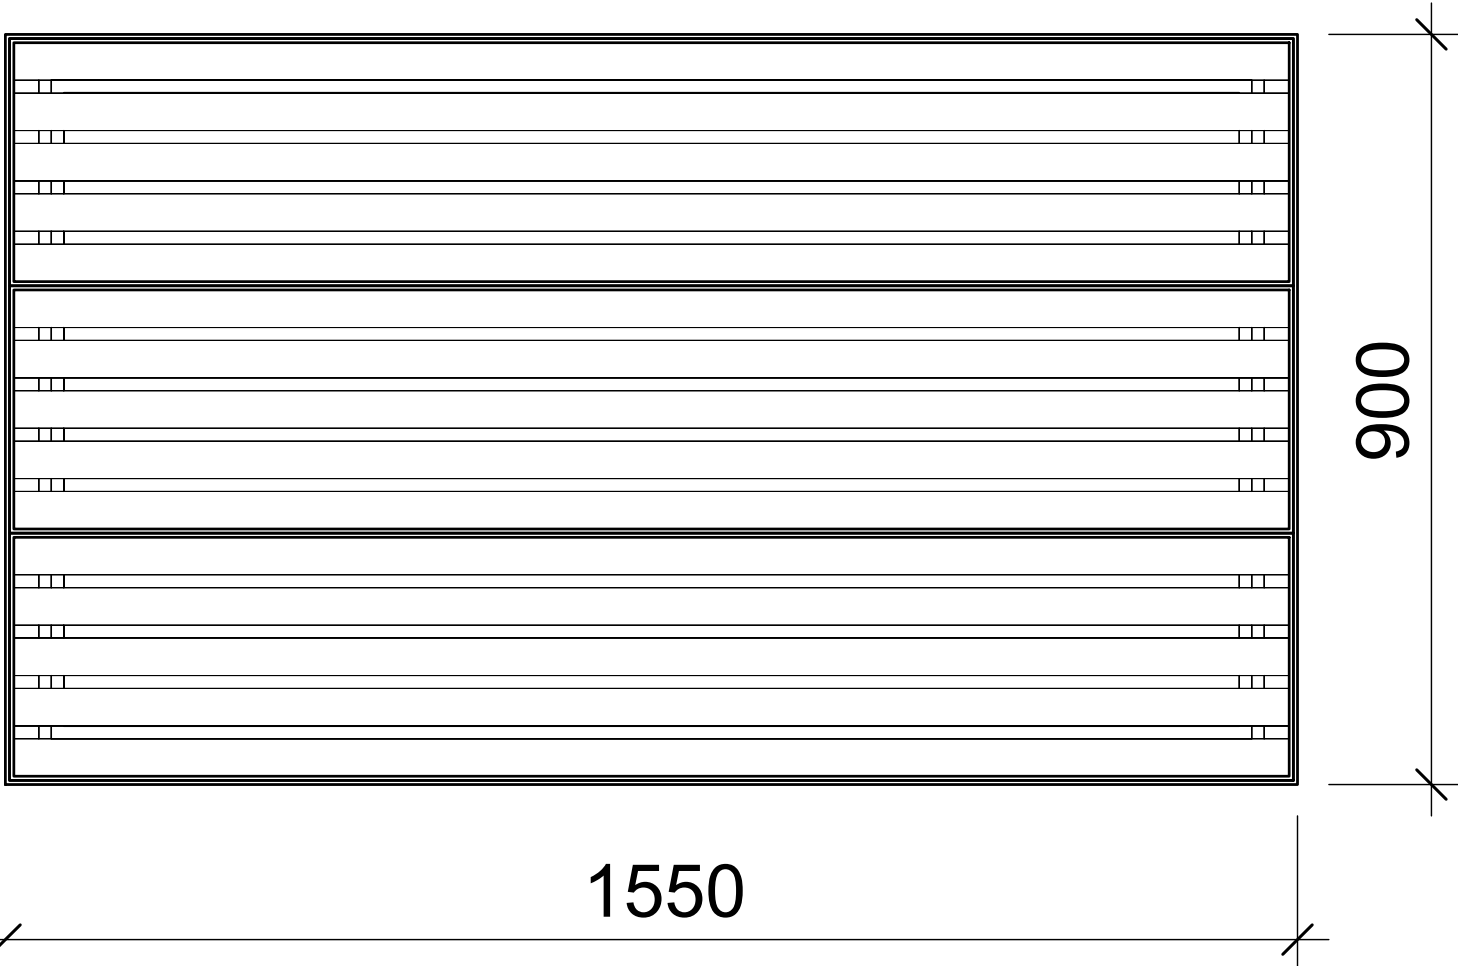


Согласовано					
Изм. № подл.	Взам. инв. №				
Изм. № подл.	Подп. и дата				

						205-25-AP				
						Капитальный ремонт здания Государственного бюджетного общеобразовательного учреждения города Москвы "Школа № 1492, расположенного по адресу : ул. Адмирала Лазарева, д. 62, к. 2				
Изм.	Кол.ч.	Лист	№ док	Подпись	Дата	Объемно-планировочные и архитектурные решения	Стадия	Лист	Листов	
Разраб.		Китов			02.26		П			
Н. контр		Казаков			02.26	Спецификация грязесборных решеток	Общество с ограниченной ответственностью ГК "АЛЬФА-СТРОЙ"			
ГИП		Гаршин			02.26					

Спецификация полов													
Марка		Помещения	Данные элементов пола			Схема пола	Марка		Помещения	Данные элементов пола			Схема пола
			Технический подвал							1 этаж			
Тип1.1		002 Техническое помещение для прокладки коммуникаций	- Обеспыливание методом грунтовки - Уклонообразующая ц/п стяжка армированная по сетке M150-200мм - 2 слоя обмазочной гидроизоляции - 5 мм (Завод гидроизоляции на стены на высоту 250 мм в 2 слоя) - Ж/Б плита - 150 мм (см. КР)				Тип4.4.		121 Учебный кабинет (1 класс), 122 Учебный кабинет (1 класс)	-ПВХ плитка 500х500мм. Forbo Effekta professional 8061 T Natural Concrete PRO (или аналог), на клею - 5 мм -Нивелирующая масса - 15 мм -Выравнивающая ц/п стяжка, армированная по сетке M150 - 45 мм - 2 слоя обмазочной гидроизоляции - 5 мм (С учетом завода гидроизоляции на стены на высоту 250 мм в 2 слоя) -Ж/Б плита			
Тип1.2		004 Вентиляционная камера 01 (Форкамера 01) 002 Вентиляционная камера 02 (Форкамера 02)	- Обеспыливание методом грунтовки - Выравнивающая ц/п стяжка армированная по сетке M150 - 30 мм - 2 слоя обмазочной гидроизоляции - 5 мм (Завод гидроизоляции на стены на высоту 250 мм в 2 слоя) - Ж/Б плита - 150 мм (см. КР)				Тип 6.		103 Санузел для МГН, 111 Санузел персонала, 112 ПУИ, 113 Санузел для девочек с комнатой личной гигиены (Основная школа), 114 Санузел для мальчиков (Основная школа), 118 Санузел для мальчиков (Начальная школа), 119 Санузел для девочек (Начальная школа), 128 Туалет медблока с местом для приготовления дезинфицирующих растворов и хранения уборочного инвентаря, предназначенных для помещений медицинского назначения	- Керамогранитная плитка 600х600мм. Фондамента пепельный светлый обрезной kerama Marazzi DL600720R (или аналог), на клею-15мм - Уклонообразующая ц/п стяжка, армированная по сеткеM150-50мм - 2 слоя обмазочной гидроизоляции-5мм (Завод гидроизоляции на стены на высоту 250 мм в 2 слоя) - Ж/Б плита			
Тип1.3		002 Техническое помещение для прокладки коммуникаций	-Выравнивающая ц/п стяжка армированная по сетке 150х150х4мм-50мм по подготовленй поверхности - Ж/Б плита - 150 мм (см. КР)				Тип7.1.		130 Помещение хранения уборочного инвентаря (пищеблок), 133 Кладовая и моечная оборотной тары, 134 Тамбур, 135а Коридор Зона "а" (Размещение холодильного оборудования), 136 Кладовая сухих продуктов, 137 Доготовочный цех, 138 Холодный цех, 139 Моечная для кухонной посуды, 140 Горячий цех, 141 Помещение для временного хранения пищевых отходов, 142 Моечная столовой посуды, 131 Санузел с душевой	- Керамогранитная плитка 600х600мм. Фондамента пепельный светлый обрезной kerama Marazzi DL600920R (или аналог), на клею-15мм - Уклонообразующая ц/п стяжка, армированная по сеткеM150 - 50мм - 2 слоя обмазочной гидроизоляции-5мм (Завод гидроизоляции на стены на высоту 250 мм в 2 слоя) - Ж/Б плита			
Тип3.1		001 Водомерный узел 003 ИТП 004 Вентиляционная камера 01 007 Вентиляционная камера 02					Тип7.2.		132 Помещение дляперсонала, 135 Коридор	- Керамогранитная плитка 600х600мм. Фондамента пепельный светлый обрезной kerama Marazzi DL600920R (или аналог), на клею-15мм - Уклонообразующая ц/п стяжка армированная по сеткеM150 – 55 мм - Полиэтиленовая пленка 200 мкм - Ж/Б плита			
Тип2.1		104 Коридор (зона ожидания для посетителей), 104 Коридор (с отделкой вестибюльного типа), 104 Коридор (с отделкой вестибюльного типа) зона "Б", 104 Коридор (с отделкой вестибюльного типа) зона "В", 116 Гардероб для обучающихся, 126 Коридор (с отделкой вестибюльного типа), 126 Коридор зона "А"	- Керамогранитная плитка 1195х600мм. Фондамента пепельный светлый обрезной kerama Marazzi DL500720R (или аналог), на клею - 15 мм - Выравнивающая ц/п стяжка, армированная по сетке M150 -55мм - Полиэтиленовая пленка 200 мкм - Ж/Б плита				Тип8.		143 Обеденный зал на 234 места	-Керамогранитная плитка 1195х600мм. Фондамента серый темный обрезной kerama Marazzi DL501020R (или аналог); Керамогранитная плитка 1195х600мм. Фондамента серый светлый обрезной kerama Marazzi DL500820R (или аналог); Керамогранитная плитка 1195х600мм. Фондамента пепельный светлый обрезной kerama Marazzi DL500720R (или аналог), на клею - 15мм - Выравнивающая ц/п стяжка, армированная по сетке M150 - 50мм -2 слоя обмазочной гидроизоляции -5 мм (Завод гидроизоляции на стены на высоту 250 мм в 2 слоя) -Ж/Б плита			
Тип2.2		104 Коридор (с отделкой вестибюльного типа), 126 Коридор (с отделкой вестибюльного типа), 143 Обеденный зал на 234 места (Умывальная)	- Керамогранитная плитка 1195х600мм. Фондамента пепельный светлый обрезной kerama Marazzi DL500720R (или аналог), на клею - 15 мм - Выравнивающая ц/п стяжка, армированная по сетке M150 -50мм - 2 слоя обмазочной гидроизоляции- 5 мм (Завод гидроизоляции на стены на высоту 250 мм в 2 слоя) - Ж/Б плита				Тип 9.		125 Кабинет врача (длинной не менее 5,5 м) 127 Процедурный (прививочный) кабинет	- Рулонный линолеум Forbo Smaragd Lux FR 6361SB (или аналог), на клею-5мм - Нивелирующая масса - 15 мм - Выравнивающая ц/п стяжка армированная по сетке M150-45мм - 2 слоя обмазочной гидроизоляции- 5 мм (Завод гидроизоляции на стены на высоту 250 мм в 2 слоя) - Ж/Б плита			
Тип3.2. Тип5.		101 Тамбур, 124 Тамбур	- Грязезащитная решетка высотой 23 мм, АЛСА А11010 (или аналог) - Керамогранитная плитка 600х600мм. Kerama Marazzi Про Стоун серый светлый обрезной DD600320R (или аналог), на клею - 15 мм - Выравнивающая ц/п стяжка, армированная по сетке M150-50 мм - 2 слоя обмазочной гидроизоляции- 5 мм (Завод гидроизоляции на стены на высоту 250 мм в 2 слоя) - Утеплитель Роквул Руф Баттс Н Оптима (или аналог) - 150 мм - Ж/Б плита				Тип 16.		145 Серверная	-Линолеум ПВХ гомогенный, виниловый антистатический с устройством мед-ной ленты в конструкции пола типа Линолеум Forbo Sphera SD 550005 dark neutral grey (класс износостойкости 34/43), на клею- 5 мм -Нивелирующая масса - 15 мм -Выравнивающая ц/п стяжка армированная по сетке M150-45мм -2 слоя обмазочной гидроизоляции - 5 мм (Завод гидроизоляции на стены на высоту 250 мм в 2 слоя) -Ж/Б плита предусмотрена обмазочная гидроизоляция марки Ceresit CR 166 (или аналог)			
							Примечание: 1. Допускается замена строительных конструкций и отделочных материалов на аналогичные, по согласованию с ГКУ ДИОМ 2. Гидроизоляцию завести на стены в мокрых помещениях на 250 мм в 2 слоя, в душевых кабинх CR 166 (или аналог) на высоту 1900 мм в 2 слоя. В проекте предусмотрена обмазочная гидроизоляция марки Ceresit 3. Затирка швов для отделки стен, плинтусов и полов подбирается индивидуально под цвет плитки. 4. Данный лист смотреть совместно с Ведомостью отделки.						
Тип3.4.		117 Электрощитовая	- Керамогранитная плитка 600х600мм. Kerama Marazzi Про Стоун серый светлый обрезной DD600320R (или аналог), на клею - 15 мм - Выравнивающая ц/п стяжка, армированная по сетке M150 -55мм - Полиэтиленовая пленка 200мкм - Ж/Б плита										
Тип4.1.		105 Гардеробная комната (для учителей), 106 Комната охраны (с диспетчерским пунктом), 148 Кладовая кабинета материальной технологии	-ПВХ плитка 500х500мм. Forbo Effekta professional 8061 T Natural Concrete PRO (или аналог), на клею-5 мм -Нивелирующая масса - 15 мм -Выравнивающая ц/п стяжка, армированная по сетке M150 -50мм -Полиэтиленовая пленка 200 мкм -Ж/Б плита										

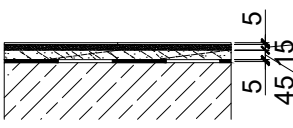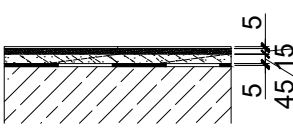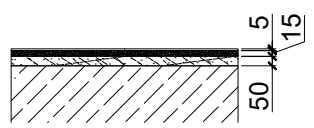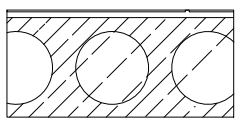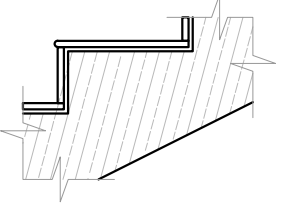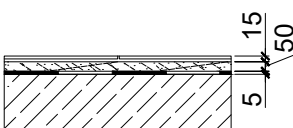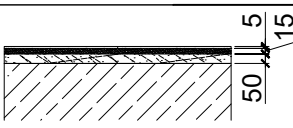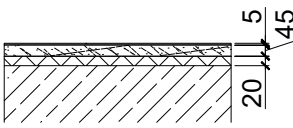Спецификация полов			
Помещения		Данные элементов пола	Схема пола
		1 этаж	
		- Текстильное коммерческое напольное флокированное покрытие Forbo Flotex 151001 black wood, 151002 grey wood, 151003 silver wood, размер 1000х250 мм (или аналог) - 5 мм - Нивелирующая масса-15 мм - Выравнивающая ц/п стяжка, армированная по сеткеМ150-45мм - 2 слоя обмазочной гидроизоляции- 5 мм (Завод гидроизоляции на стены на высоту 250 мм в 2 слоя) - Ж/Б плита	
115 Лабораторно-исследовательский комплекс для изучения естествознания тип 1, 146 Технология материальная Тип 2, 147 Технология материальная Тип 1		- ПВХ плитка 500х500мм. Forbo Effekta professional 8066 Silt Concrete PRO (или аналог); ПВХ плитка 500х500мм. Forbo Effekta professional 8065 Dark Grey Concrete PRO (или аналог); ПВХ плитка 500х500мм. Forbo Effekta professional 8121 Silt Imprint Concrete PRO (или аналог), на клею-5 мм - Нивелирующая масса - 15 мм - Выравнивающая ц/п стяжка, армированная по сетке М150 - 45 мм - 2 слоя обмазочной гидроизоляции-5 мм (С учетом завода гидроизоляции на стены на высоту 250 мм в 2 слоя) - Ж/Б плита	
109 Кабинет иностранного языка с возможностью деления трансформируемой перегородкой на два		- ПВХ плитка 500х500мм. Forbo Effekta professional 8066 Silt Concrete PRO (или аналог); ПВХ плитка 500х500мм. Forbo Effekta professional 8065 Dark Grey Concrete PRO (или аналог); ПВХ плитка 500х500мм. Forbo Effekta professional 8121 Silt Imprint Concrete PRO (или аналог), на клею-5мм - Нивелирующая масса - 15 мм - Выравнивающая ц/п стяжка, армированная по сетке М150-50мм - Полиэтиленовая пленка 200мкм - Ж/Б плита	
		Лестница тип Н2	
107, 123, 129, 150, 201, 213, 232, 243, 301, 316, 319, 331,		(лестничная площадка)Marazzi DD641020R ПРО ЛАЙМСТОУН - Керамический гранит Kerama серый, светлый, натуральный, обрезной, 600х600мм (или аналог), на клею - сущ. ж/б плита	
107, 123, 129, 150, 201, 213, 232, 243, 301, 316, 319, 331,		(лестн. ступени 1-4 этажи) - Ступень завальцованная с противоскользящей насечкой KERAMA MARAZZI DD205320RR ПРО ЛАЙМСТОУН СЕРЫЙ СВЕТЛЫЙ НАТУРАЛЬНЫЙ ОБРЕЗНОЙ 600Х300 мм (или аналог), DD205320R\2 ПОДСТУПЕНОК ПРО ЛАЙМСТОУН СЕРЫЙ СВЕТЛЫЙ НАТУРАЛЬНЫЙ ОБРЕЗНОЙ 600Х145 мм (или аналог), на клею - 20мм	
		2 этаж	
216 Душевая для девочек, 219 Душевая для мальчиков, 223 Душевая для девочек, 226 Душевая		- Керамогранитная плитка 600х600мм. Kerama Marazzi Про Стоун серый светлый обрезной DD600320R (или аналог), на клею - 15 мм - Выравнивающая ц/п стяжка, армированная по сетке М150-50 мм - 2 слоя обмазочной гидроизоляции- 5 мм (Завод гидроизоляции на стены на высоту 250 мм в 2 слоя) - Ж/Б плита	
228 Снарядная, 236 Подсобное помещение, 239 Кладовая инвентаря		- ПВХ плитка 500х500мм. Forbo Effekta professional 8061 T Natural Concrete PRO (или аналог), на клею - 5 мм - Нивелирующая масса - 15 мм - Выравнивающая ц/п стяжка, армированная по сетке М150 - 50мм - Полиэтиленовая пленка 200 мкм - Ж/Б плита	
202 Коридор (Начальная школа), 208 Кабинет для индивидуальных занятий, в т.ч. с коррекционным педагогом, 217 Раздевальная, 218 Раздевальная, 224 Раздевальная, 225 Раздевальная, 229 Раздевальная, 230 Раздевальная, 233 Коридор (Основная школа), 234		- ПВХ плитка 500х500мм. Forbo Effekta professional 8061 T Natural Concrete PRO (или аналог), на клею - 5 мм - Выравнивающая армированная ц/п стяжка по сетке М150 - 45 мм - Полиэтиленовая пленка 200 мкм - Плита звукоизоляционная Стопзвук БП Флор (или аналог)-20 мм - Ж/Б плита	
языка и литературы, 235 Кабинет русского языка и литературы, 240 Кабинет истории Тип1, 241 Кабинет русского языка и литературы,			

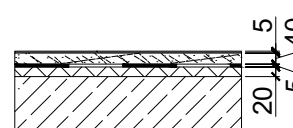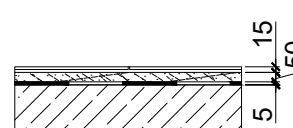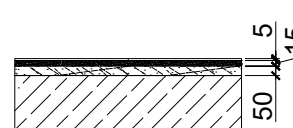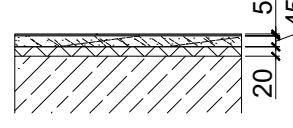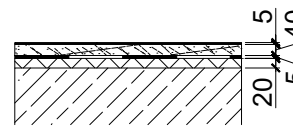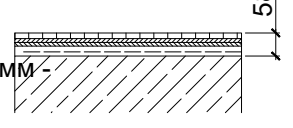Спецификация полов			
Марка	Помещения	Данные элементов пола	Схема пола
2 этаж			
Тип 4.3.	202 Коридор (Начальная школа), 203 Учебный кабинет 204 Учебный кабинет (2-4 класс) 207 Учебный кабинет (2-4 класс), 211Учебный кабинет (2-4 класс), 233 Коридор (Основная школа), 308 Лаборантская кабинета физики	- ПВХ плитка 500х500мм. Forbo Effekta professional 8061 T Natural Concrete PRO (или аналог), на клею - 5 мм - Выравнивающая армированная ц/п стяжка по сетке М150 - 40 мм - 2 слоя обмазочной гидроизоляции- 5мм (Завод гидроизоляции на стены на высоту 250 мм в 2 слоя) - Плита звукоизоляционная Стопзвук БП Флор (или аналог)-20 мм - Ж/Б плита	
Тип 6.	202 Коридор (Начальная школа), 205 ПУИ, 206 Санузел персонала, 209 Санузел персонала, 210 ПУИ, 215 Санузел для девочек (Начальная школа), 220 Санузел для мальчиков (Начальная школа), 222 Санузел для девочек с комнатой личной гигиены (Основная школа), 227 Санузел для мальчиков (Основная школа)	- Керамогранитная плитка 600х600мм. Фондамента пепельный светлый обрезной kerama Marazzi DL600720R (или аналог), на клею-15мм - Уклонообразующая ц/п стяжка, армированная по сеткеМ150-50мм - 2 слоя обмазочной гидроизоляции - 5 мм (Завод гидроизоляции на стены на высоту 250 мм в 2 слоя) - Ж/Б плита	
Тип10.2.	214 Комната инструктора	- ПВХ плитка 1000х200мм. Forbo Effekta professional 8043 WhiteFine Oak PRO (или аналог)-5мм - Нивелирующая масса - 15 мм - Выравнивающая ц/п стяжка, армированная по сетке М150 -50мм - Полиэтиленовая пленка 200мкм - Ж/Б плита	
Тип13.1.	244 Пространство с функцией актового зала (с эстрадой в уровне пола)	- ПВХ плитка 500х500мм. Forbo Effekta professional 8066 Silt Concrete PRO (или аналог); ПВХ плитка 500х500мм. Forbo Effekta professional 8065 Dark Grey Concrete PRO (или аналог); ПВХ плитка 500х500мм. Forbo Effekta professional 8121 Silt Imprint Concrete PRO (или аналог), на клею - 5 мм - Выравнивающая ц/п стяжка армированная по сетке М150 -45мм - Полиэтиленовая пленка 200мкм - Плита звукоизоляционная Стопзвук БП Флор (или аналог)-20 мм - Ж/Б плита	
Тип13.3.	237 Учебный кабинет для изучения естествознания: физика	- ПВХ плитка 500х500мм. Forbo Effekta professional 8066 Silt Concrete PRO (или аналог); ПВХ плитка 500х500мм. Forbo Effekta professional 8065 Dark Grey Concrete PRO (или аналог); ПВХ плитка 500х500мм. Forbo Effekta professional 8121 Silt Imprint Concrete PRO (или аналог), на клею - 5 мм - Выравнивающая ц/п стяжка, армированная по сетке М150 -40мм - 2 слоя обмазочной гидроизоляции- 5 мм (С учетом завода гидроизоляции на стены на высоту 250 мм в 2 слоя) - Плита звукоизоляционная Стопзвук БП Флор (или аналог)-20мм - Ж/Б плита	
Тип 14.	221 Универсальный спортивный зал тип 2, 231 Универсальное помещение с возможностью проведения ЛФК	-Спортивный паркет krast school kr57 1800х 300 мм (или аналог)-14мм -Каучуковые профессиональные амортизаторы - 20мм -2 слоя влагостойкой фанеры ФК, сорт 2/3, шлифованная, 1525мм*1525мм*12мм-24мм -Ж/Б плита	




Примечание:
1. Допускается замена строительных конструкций и отделочных материалов на аналогичные,по согласованию с ГКУ ДИОМ
2. Гидроизоляцию завести на стены в мокрых помещениях на 250 мм в 2 слоя, в душевых кабинах на высоту 1900 мм в 2 слоя. В проекте предусмотрена обмазочная гидроизоляция марки Ceresit CR 166 (или аналог)
3. Затирка швов для отделки стен, плинтусов и полов подбирается индивидуально под цвет плитки.
4. Данный лист смотреть совместно с Ведомостью отделки.

							205-25-AP			
							Капитальный ремонт здания Государственное бюджетное общеобразовательное учреждение города Москвы "Школа № 1492, расположенного по адресу : ул. Адмирала Лазарева, д. 62, к. 2			
Изм.	Кол.уч.	Лист	№ док	Подпись	Дата	Объемно-планировочные и архитектурные решения		Стадия	Лист	Листов
Разраб.		Китов		Китов	02.26			П		
						Спецификация полов (продолжение)		Общество с ограниченной ответственностью ГК "АЛЬФА-СТРОЙ"		
Н. контр		Казаков		Казаков	02.26					
ГИП		Гаршин		Гаршин	02.26					

Инв. № подл.	Подп. и дата	Взам. инв. №

Согласовано _____

Марка		Помещения	Данные элементов пола	Схема пола
3 этаж				
Тип3.5.	317	Венткамера	- Керамогранитная плитка 600х600мм. Kerama Marazzi Про Стоун серый светлый обрешной DD600320R (или аналог), на клею - 15 мм - Выравнивающая ц/п стяжка, армированная по сетке M150 -35мм - Полиэтиленовая пленка 200мкм - Плита звукоизоляционная Стопзвук БП Флор (или аналог)-20 мм - Ж/Б плита	
Тип4.1.	305	Подсобное помещение	-ПВХ плитка 500х500мм. Forbo Effekta professional 8061 T Natural Concrete PRO (или аналог), на клею - 5 мм -Нивелирующая масса - 15 мм -Выравнивающая ц/п стяжка, армированная по сетке M150 - 50 мм -Полиэтиленовая пленка 200 мкм -Ж/Б плита	
Тип 4.2	302	Коридор (Начальная школа), 309 Кабинет для индивидуальных занятий, в т.ч. с учителем - логопедом, 315 Кабинет для индивидуальных занятий, в т.ч. с педагогом- психологом, 317а Коридор, 318 Коридор (Основная школа), 320 Кабинет математики, 321 Кабинет ОБЗР, 330 Лабораторская при кабинете информационных технологий	- ПВХ плитка 500х500мм. Forbo Effekta professional 8061 T Natural Concrete PRO(или аналог), на клею - 5 мм - Выравнивающая армированная ц/п стяжка по сетке M150 - 45 мм - Полиэтиленовая пленка 200 мкм - Плита звукоизоляционная Стопзвук БП Флор (или аналог)-20 мм - Ж/Б плита	
Тип 4.3	302	Коридор (Начальная школа), 303 Учебный кабинет (2-4 классы), 304 Учебный кабинет (2-4 классы), 313 Учебный кабинет (2-4 классы), 314 Учебный кабинет (2-4 классы), 318 Коридор (Основная школа), 323 Лаборантская кабинета биологии	- ПВХ плитка 500х500мм. Forbo Effekta professional 8061 T Natural Concrete PRO (или аналог), на клею - 5 мм - Выравнивающая армированная ц/п стяжка по сетке M150 - 40 мм - 2 слоя обмазочной гидроизоляции- 5мм (Завод гидроизоляции на стены на высоту 250 мм в 2 слоя) - Плита звукоизоляционная Стопзвук БП Флор (или аналог)-20 мм - Ж/Б плита	
Тип 6.	307	Санузел для девочек (Начальная школа), 310 Санузел для мальчиков (Начальная школа), 311 Санузел персонала, 312 ПУИ, 325 Санузел для девочек с комнатой личной гигиены (Основная школа), 327 Санузел для мальчиков (Основная школа)	- Керамогранитная плитка 600х600мм. Фондамента пепельный светлый обрешной kerama Marazzi DL600720R (или аналог), на клею-15мм - Уклонообразующая ц/п стяжка, армированная по сеткеM150-50мм - 2 слоя обмазочной гидроизоляции - 5 мм (Завод гидроизоляции на стены на высоту 250 мм в 2 слоя) - Ж/Б плита	
Тип10.2	308	Административный кабинет тип 1 (Начальная школа), 326 Административный кабинет тип 1 (Начальная школа)	- ПВХ плитка 1000х200мм. Forbo Effekta professional 8043 WhiteFine Oak PRO (или аналог) -5мм - Нивелирующая масса - 15 мм - Выравнивающая ц/п стяжка, армированная по сетке M150 -50мм - Полиэтиленовая пленка 200мкм -Ж/Б плита	

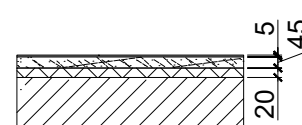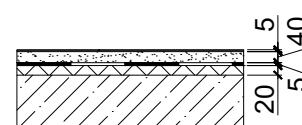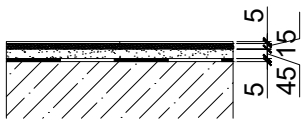Марка		Помещения	Данные элементов пола	Схема пола
3 этаж				
Тип13.1.	329 Кабинет информационны технологий, 332 Универсальное помещение с возможностью организации Медиацентра тип 1	- ПВХ плитка 500х500мм. Forbo Effekta professional 8066 Silt Concrete PRO (или аналог); ПВХ плитка 500х500мм. Forbo Effekta professional 8065 Dark Grey Concrete PRO (или аналог); ПВХ плитка 500х500мм. Forbo Effekta professional 8121 Silt Imprint Concrete PRO (или аналог), на клею - 5 мм - Выравнивающая ц/п стяжка армированная по сетке M150 -45мм - Полиэтиленовая пленка 200мкм - Плита звукоизоляционная Стопзвук БП Флор (или аналог)-20 мм - Ж/Б плита		
Тип13.3.	306 Кабинет иностранного языка с возможностью деления трансформируемой перегородкой на два помещения (начальная школа), 324 Учебный кабинет для изучения естествознания: биология тип 1	- ПВХ плитка 500х500мм. Forbo Effekta professional 8066 Silt Concrete PRO (или аналог); ПВХ плитка 500х500мм. Forbo Effekta professional 8065 Dark Grey Concrete PRO (или аналог); ПВХ плитка 500х500мм. Forbo Effekta professional 8121 Silt Imprint Concrete PRO (или аналог), на клею - 5 мм - Выравнивающая ц/п стяжка армированная по сетке M150 -40мм - 2 слоя обмазочной гидроизоляции- 5 мм (С учетом завода гидроизоляции на стены на высоту 250 мм в 2 слоя) - Плита звукоизоляционная Стопзвук БП Флор (или аналог)-20мм - Ж/Б плита		
Тип 16.	322 Кроссовая, 328 Кроссовая	-Линолеум ПВХ гомогенный, виниловый антистатический с устройством мед-ной ленты в конструкции пола типа Линолеум Forbo Sphera SD 550005 dark neutral greu (класс износостойкости 34/43), на клею- 5 мм -Нивелирующая масса - 15 мм -Выравнивающая ц/п стяжка армированная по сетке M150-45мм -2 слоя обмазочной гидроизоляции - 5 мм (Завод гидроизоляции на стены на высоту 250 мм в 2 слоя) -Ж/Б плита		

Примечание:



1. Допускается замена строительных конструкций и отделочных материалов на аналогичные, по согласованию с ГКУ ДИОМ






2. Гидроизоляцию завести на стены в мокрых помещениях на 250 мм в 2 слоя, в душевых кабинках

CR 166 (или аналог)

3. Затирка швов для отделки стен, плинтусов и полов подбирается индивидуально под цвет плитки.

4. Данный лист смотреть совместно с Ведомостью отделки на высоту 1900 мм в 2 слоя. В проекте предусмотрена обмазочная гидроизоляция марки Ceresit

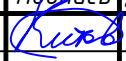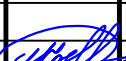						205-25-AP			
						Капитальный ремонт здания Государственное бюджетное общеобразовательное учреждение города Москвы "Школа № 1492, расположенного по адресу : ул. Адмирала Лазарева, д. 62, к. 2			
Изм.	Кол.ч	Лист	№ док	Подпись	Дата				
Разраб.		Китов			02.26	Объемно-планировочные и архитектурные решения	Стадия	Лист	Листов
							П		
Н. контр		Казаков			02.26	Спецификация полов (продолжение)	Общество с ограниченной ответственностью ГК "АЛЬФА-СТРОЙ"		
ГИП		Гаршин			02.26				

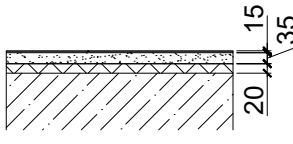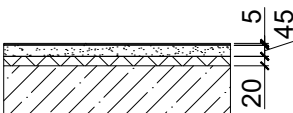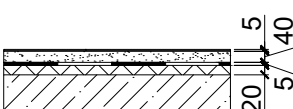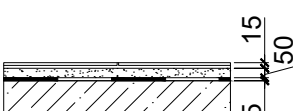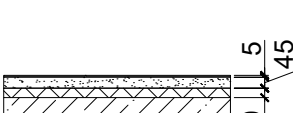				Спецификация полов			
Марка		Помещения		Данные элементов пола		Схема пола	
3 этаж							
Тип3.5.	418 Венткамера, 419 Венткамера	- Керамогранитная плитка 600х600мм. Kerama Marazzi Про Стоун серый светлый обрезной DD600320R (или аналог), на клею - 15 мм - Выравнивающая ц/п стяжка, армированная по сетке M150 -35мм - Полиэтиленовая пленка 200мкм - Плита звукоизоляционная Стопзвук БП Флор (или аналог)-20 мм - Ж/Б плита					
Тип4.1.	405 Подсобное помещение, 417 Балкон, 426 Балкон, 428 Техническое помещение, 429 Техническое помещение, 433 Подсобное помещение, 435 Крессовая	Тип4.1. - ПВХ плитка 500х500мм. Forbo Effekta professional 8061 T Natural Concrete PRO (или аналог), на клею - 5 мм - Нивелирующая масса - 15 мм - Выравнивающая ц/п стяжка, армированная по сетке M150-50мм - Полиэтиленовая пленка 200 мкм - Ж/Б плита					
Тип4.2.	402 Коридор, 403 Кабинет географии, 404 Кабинет истории Тип 1, 406 Лаборантская кабинета химии, 408 Кабинет математики, 409 Кабинет математики, 420 Рекреация (Основная и старшая школа), 422 Коридор, 427 Коридор, 436 Кабинет информатики с возможностью деления трансформируемой перегородкой на два помещения	- ПВХ плитка 500х500мм. Forbo Effekta professional 8061 T Natural Concrete PRO (или аналог), на клею - 5 мм - Выравнивающая армированная ц/п стяжка по сетке M150-45мм - Полиэтиленовая пленка 200 мкм - Плита звукоизоляционная Стопзвук БП Флор (или аналог) -20 мм - Ж/Б плита					
Тип4.3.	402 Коридор, 422 Коридор	- ПВХ плитка 500х500мм. Forbo Effekta professional 8061 T Natural Concrete PRO (или аналог), на клею - 5 мм - Выравнивающая армированная ц/п стяжка по сетке M150-40мм - 2 слоя обмазочной гидроизоляции - 5мм (Завод гидроизоляции на стены на высоту 250 мм в 2 слоя) - Плита звукоизоляционная Стопзвук БП Флор (или аналог) -20 мм - Ж/Б плита					
Тип6.	410 Санузел персонала, 411 ПУИ, 413 Санузел для мальчиков (Основная школа), 416 Санузел для девочек (Основная школа), 423 Санузел для мальчиков (Основная школа), 425 Санузел для девочек с комнатой личной гигиены (Основная школа)	- Керамогранитная плитка 600х600мм. Фондамента пепельный светлый обрезной kerama Marazzi DL600720R (или аналог), на клею - 15 мм - Уклонообразующая ц/п стяжка, армированная по сеткеM150-50мм - 2 слоя обмазочной гидроизоляции - 5 мм (Завод гидроизоляции на стены на высоту 250 мм в 2 слоя) - Ж/Б плита					
Тип10.2	414 Административный кабинет тип 1 (Основная школа), 415 Административный кабинет тип 1 (Основная школа),	- ПВХ плитка 1000х200мм. Forbo Effekta professional 8043 WhiteFine Oak PRO (или аналог)-5мм - Нивелирующая масса - 15 мм - Выравнивающая ц/п стяжка, армированная по сетке M150-50мм - Полиэтиленовая пленка 200мкм -Ж/Б плита					
Тип13.1	424 Многофункциональный информационный библиотечный центр (хранение книг), 430 Многофункциональный информационный библиотечный центр с зоной для индивидуальных занятий, 432 Информационный библиотечный центр с зоной для индивидуальных занятий, 434 Кабинет иностранного языка с возможностью деления трансформируемой перегородкой на два помещения (Основная школа)	- ПВХ плитка 500х500мм. Forbo Effekta professional 8066 Silt Concrete PRO (или аналог); ПВХ плитка 500х500мм. Forbo Effekta professional 8065 Dark Grey Concrete PRO (или аналог); ПВХ плитка 500х500мм. Forbo Effekta professional 8121 Silt Imprint Concrete PRO (или аналог), на клею - 5 мм - Выравнивающая ц/п стяжка, армированная по сетке M150-45мм - Полиэтиленовая пленка 200мкм - Плита звукоизоляционная Стопзвук БП Флор (или аналог) -20 мм - Ж/Б плита					
Тип13.3	407 Учебные кабинеты для изучения естествознания: химия	- ПВХ плитка 500х500мм. Forbo Effekta professional 8066 Silt Concrete PRO (или аналог); ПВХ плитка 500х500мм. Forbo Effekta professional 8065 Dark Grey Concrete PRO (или аналог); ПВХ плитка 500х500мм. Forbo Effekta professional 8121 Silt Imprint Concrete PRO (или аналог), на клею - 5 мм - Выравнивающая ц/п стяжка, армированная по сетке M150-40мм - 2 слоя обмазочной гидроизоляции - 5 мм (С учетом завода гидроизоляции на стены на высоту 250 мм в 2 слоя) - Плита звукоизоляционная Стопзвук БП Флор (или аналог) -20мм - Ж/Б плита					

Помещения	Данные элементов пола	Схема пола
Наружные работы		
Площадка главных входных групп в осях "А, 6-9" и "С, 6-9"	-Термообработанный гранит Габбро северный 300х600 мм (или аналог)-30мм -Клеевая основа - 5 мм -Мастика гидроизоляционная МБИ битумная - 3-5 мм -Ж/Б плита (см. в КР)	
Пандус	-Термообработанный гранит Габбро северный 300х600 мм (или аналог) - 30 мм -Клеевая основа - 5 мм -Мастика гидроизоляционная МБИ битумная - 5 мм -Ж/Б плита (см. в КР)	
Лестница главных входных групп в осях "А, 6-9" и "С, 6-9"	-Термообработанный гранит Габбро северный для ступеней 300х600мм (или аналог)-30 мм -Термообработанный гранит Габбро северный для подступенков 300х600мм (или аналог) - 20 мм -Клеевая основа - 5 мм -Мастика гидроизоляционная МБИ битумная - 5 мм -Ж/Б плита (см. в КР)	
Облицовка горизонтальных площадок остальных входов в здание и приямков в подвал	-Керамогранитная плитка Kerama Marazzi Про Фьюче антрацит обрезной 600х600мм (или аналог) - 10 мм -Клеевая основа - 5 мм -Мастика гидроизоляционная МБИ битумная - 5 мм -Ж/Б плита (см. в КР)	
Облицовка ступеней лестниц остальных входов в здание и приямков в подвал	-Керамогранитная плитка Kerama Marazzi Про Фьюче антрацит обрезной 600х600мм (или аналог) - 10 мм -Клеевая основа - 5 мм -Мастика гидроизоляционная МБИ битумная - 5 мм -Ж/Б плита (см. в КР)	






Примечание:


1. Допускается замена строительных конструкций и отделочных материалов на аналогичные, по согласованию с ГКУ ДИОМ
2. Гидроизоляцию завести на стены в мокрых помещениях на 250 мм в 2 слоя, в душевых кабинах

3. Затирка швов для отделки стен, плинтусов и полов подбирается индивидуально под цвет плитки.

4. Данный лист смотреть совместно с Ведомостью отделки на высоту 1900 мм в 2 слоя. В проекте предусмотрена обмазочная гидроизоляция марки Ceresit

						205-25-AP			
						Капитальный ремонт здания Государственное бюджетное общеобразовательное учреждение города Москвы "Школа № 1492, расположенного по адресу: ул. Адмирала Лазарева, д. 62, к. 2			
Изм.	Кол.уч	Лист	№ док	Подпись	Дата	Объемно-планировочные и архитектурные решения	Стадия	Лист	Листов
Разраб.	Китов				02.26		П		
						Спецификация полов (продолжение)	Общество с ограниченной ответственностью ГК "АЛЬФА-СТРОЙ"		
Н. контр	Казаков				02.26				
ГИП	Гаршин				02.26				

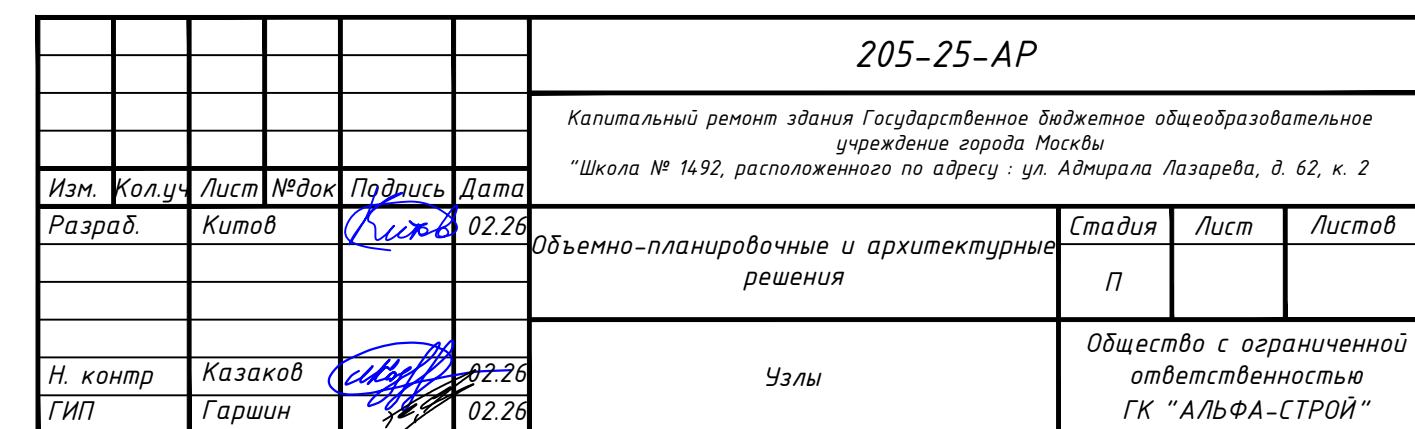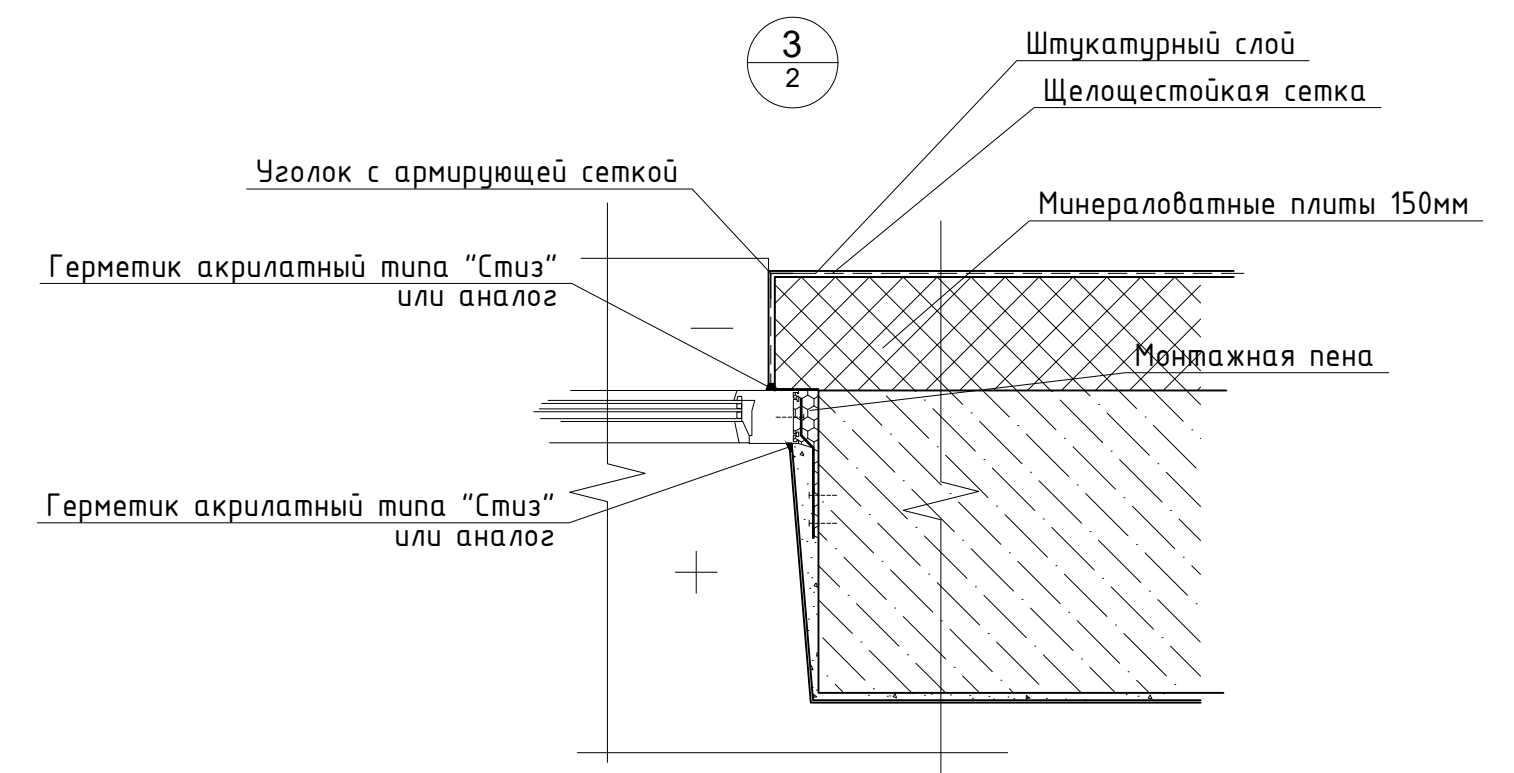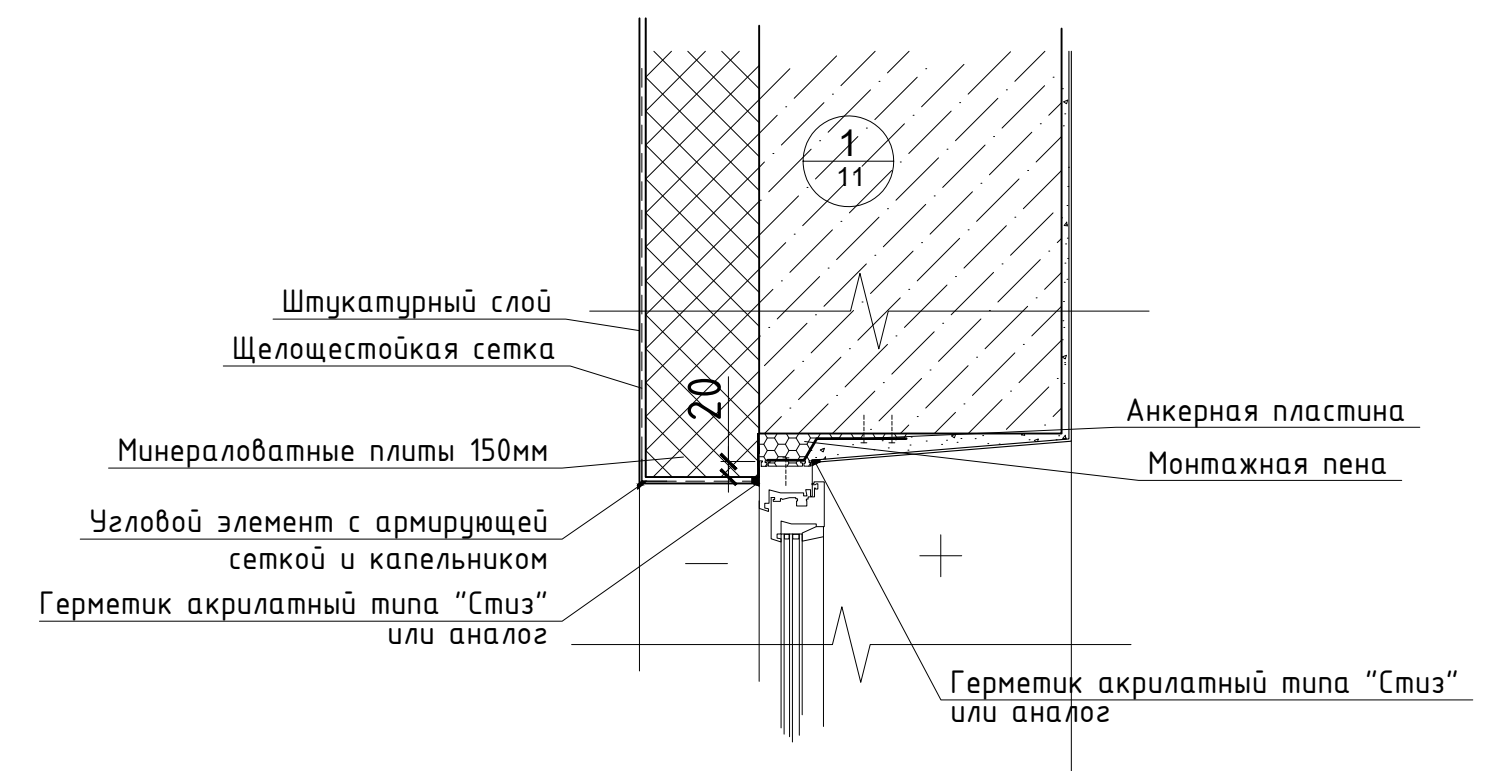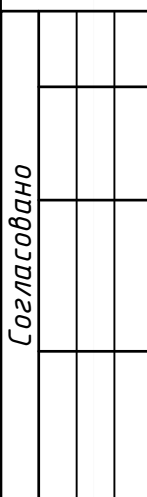
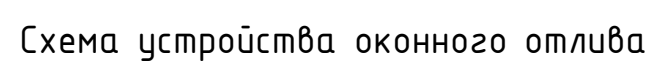


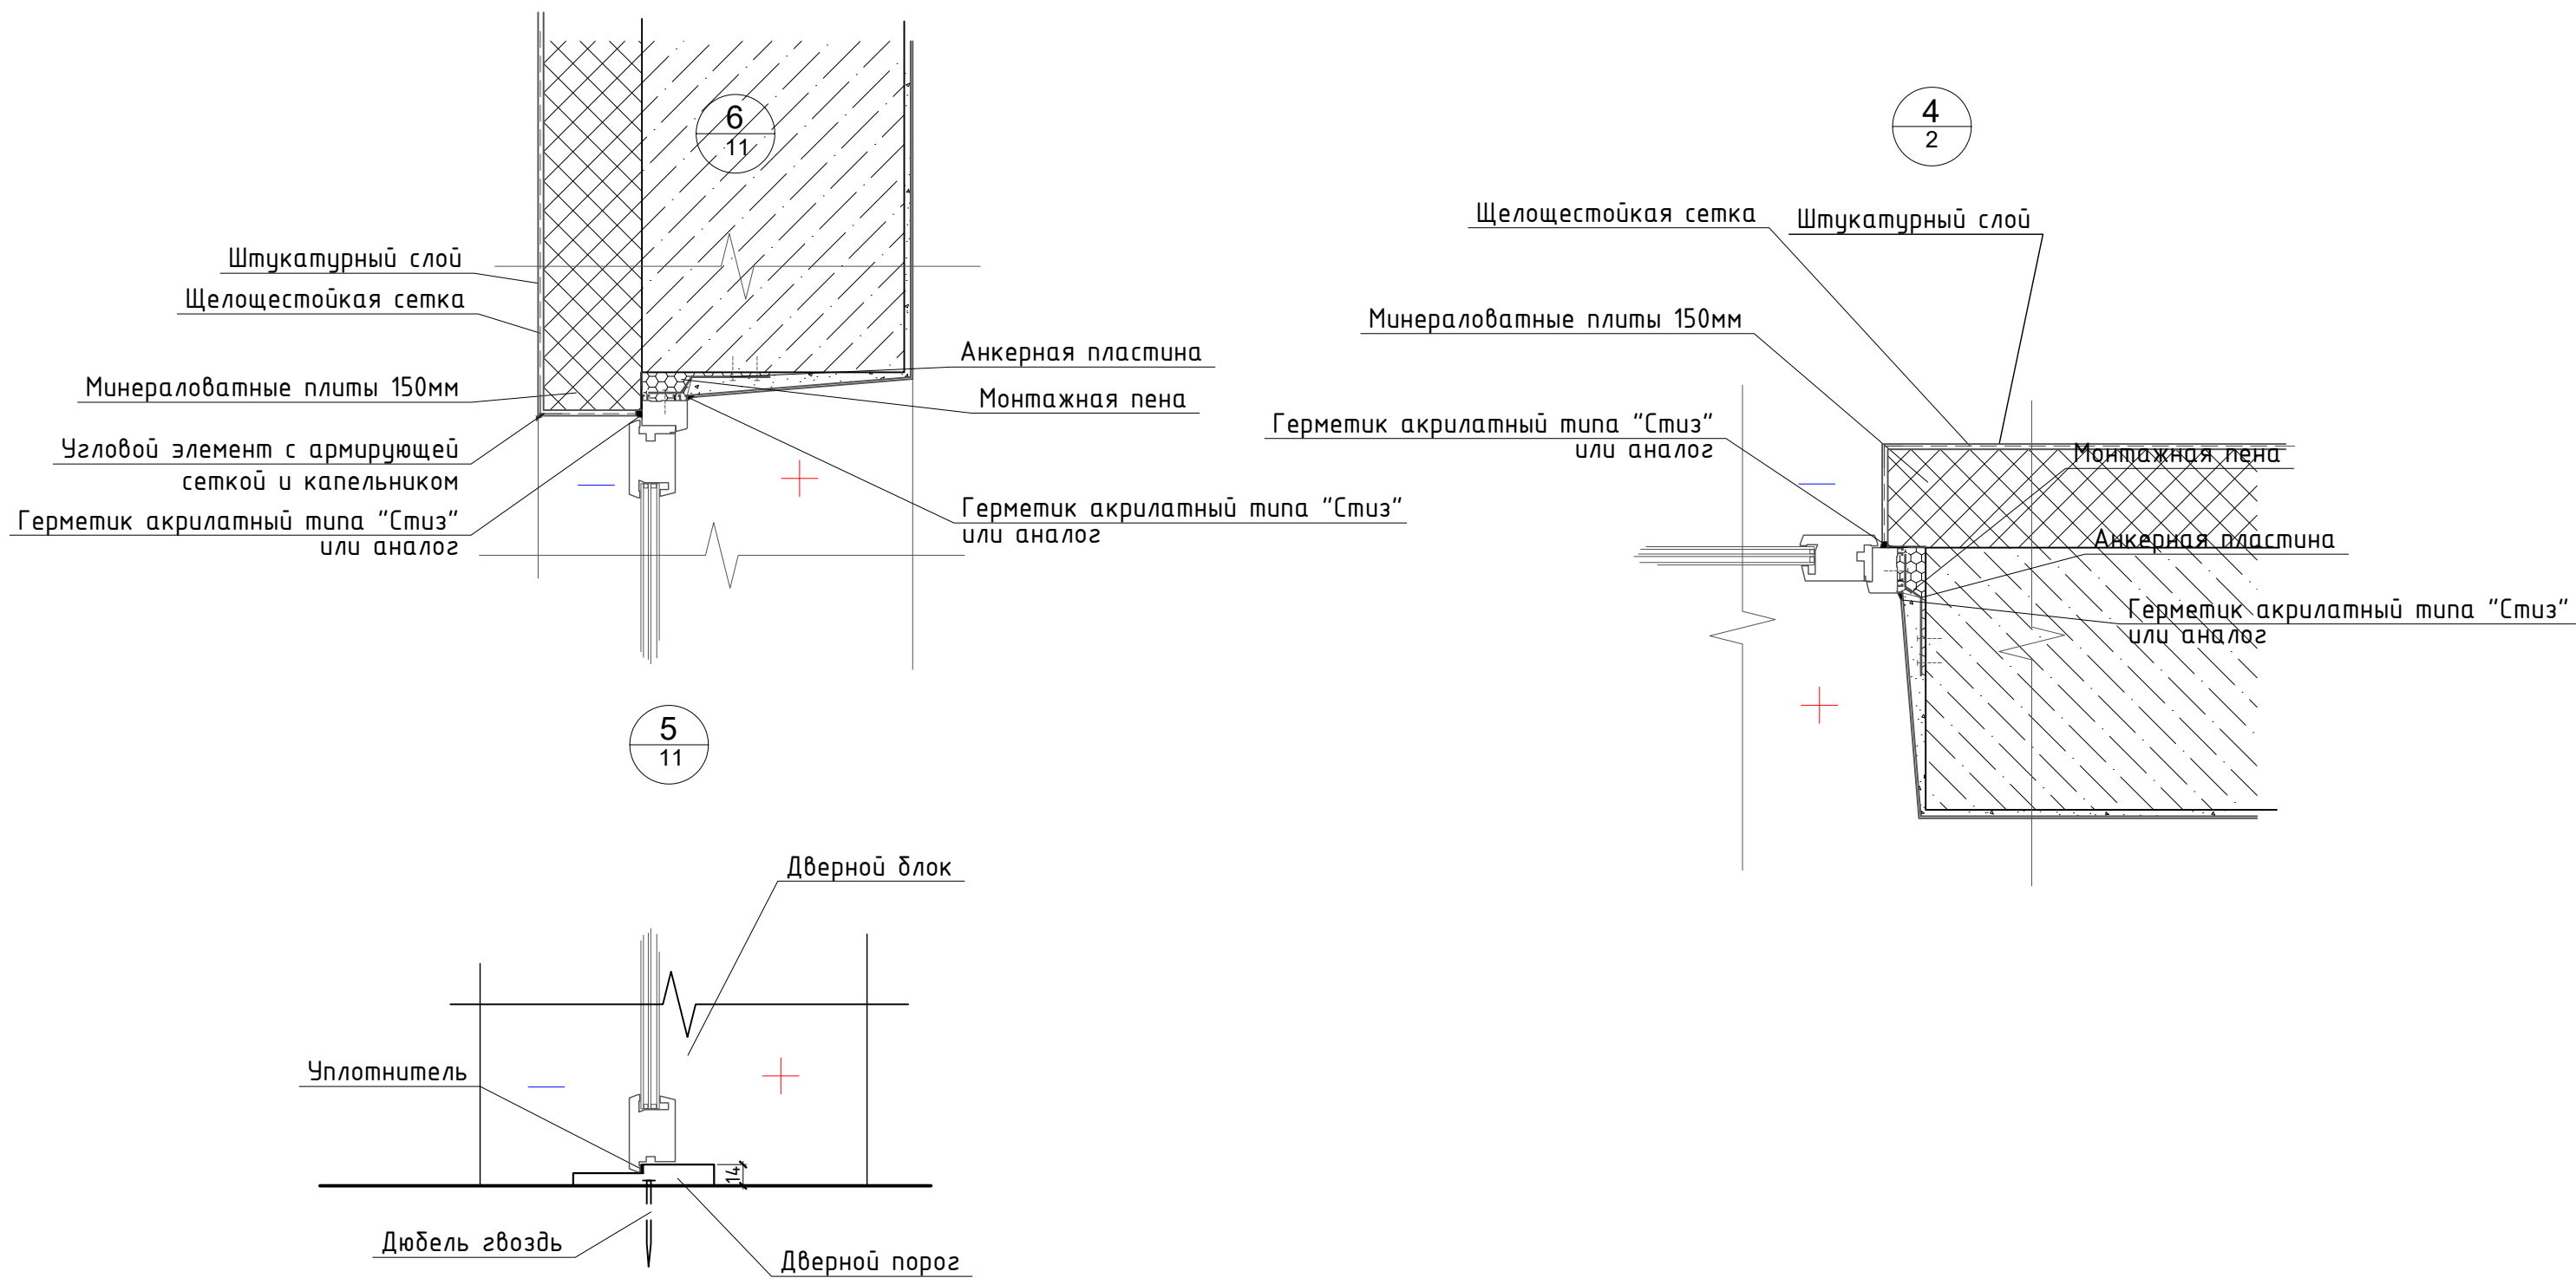


Согласовано				
Инв. № подл.	Подп. и дата	Взам. инв. №		

							205-25-AP			
							Капитальный ремонт здания Государственное бюджетное общеобразовательное учреждение города Москвы "Школа № 1492, расположенного по адресу : ул. Адмирала Лазарева, д. 62, к. 2			
Изм.	Кол.уч.	Лист	№ док	Подпись	Дата	Объемно-планировочные и архитектурные решения		Стадия	Лист	Листов
Разраб.	Китов			Китов	02.26			П		
Н. контр	Казаков			Казаков	02.26	Узлы		Общество с ограниченной ответственностью ГК "АЛЬФА-СТРОЙ"		
ГИП	Гаршин			Гаршин	02.26					

Вертикальный разрез пооконному проему

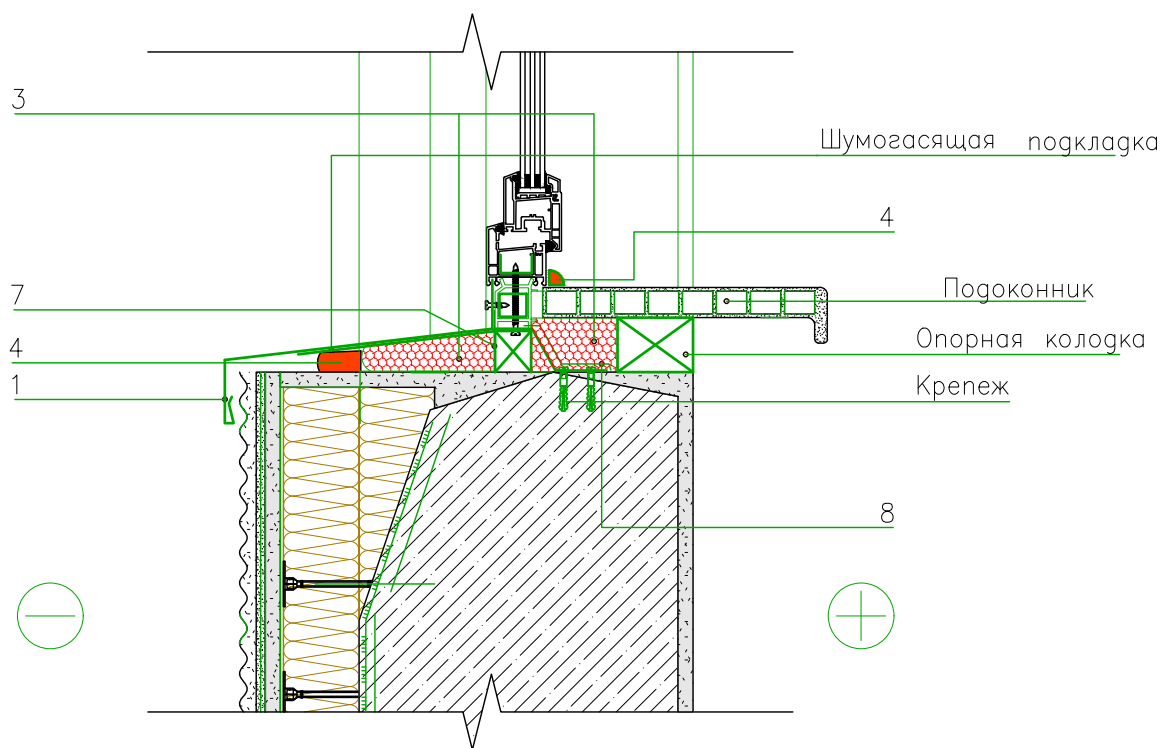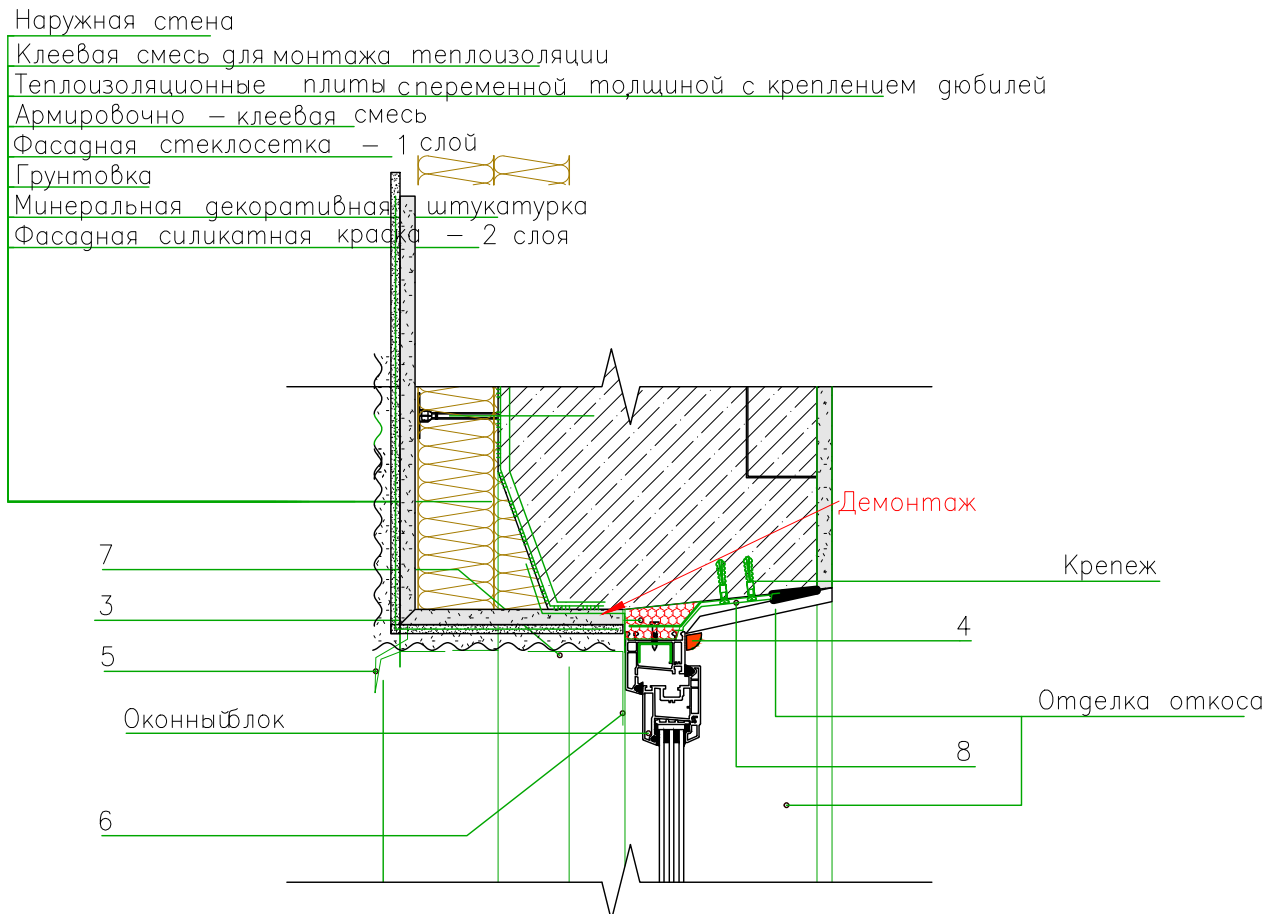

Горизонтальный разрез по оконному проему

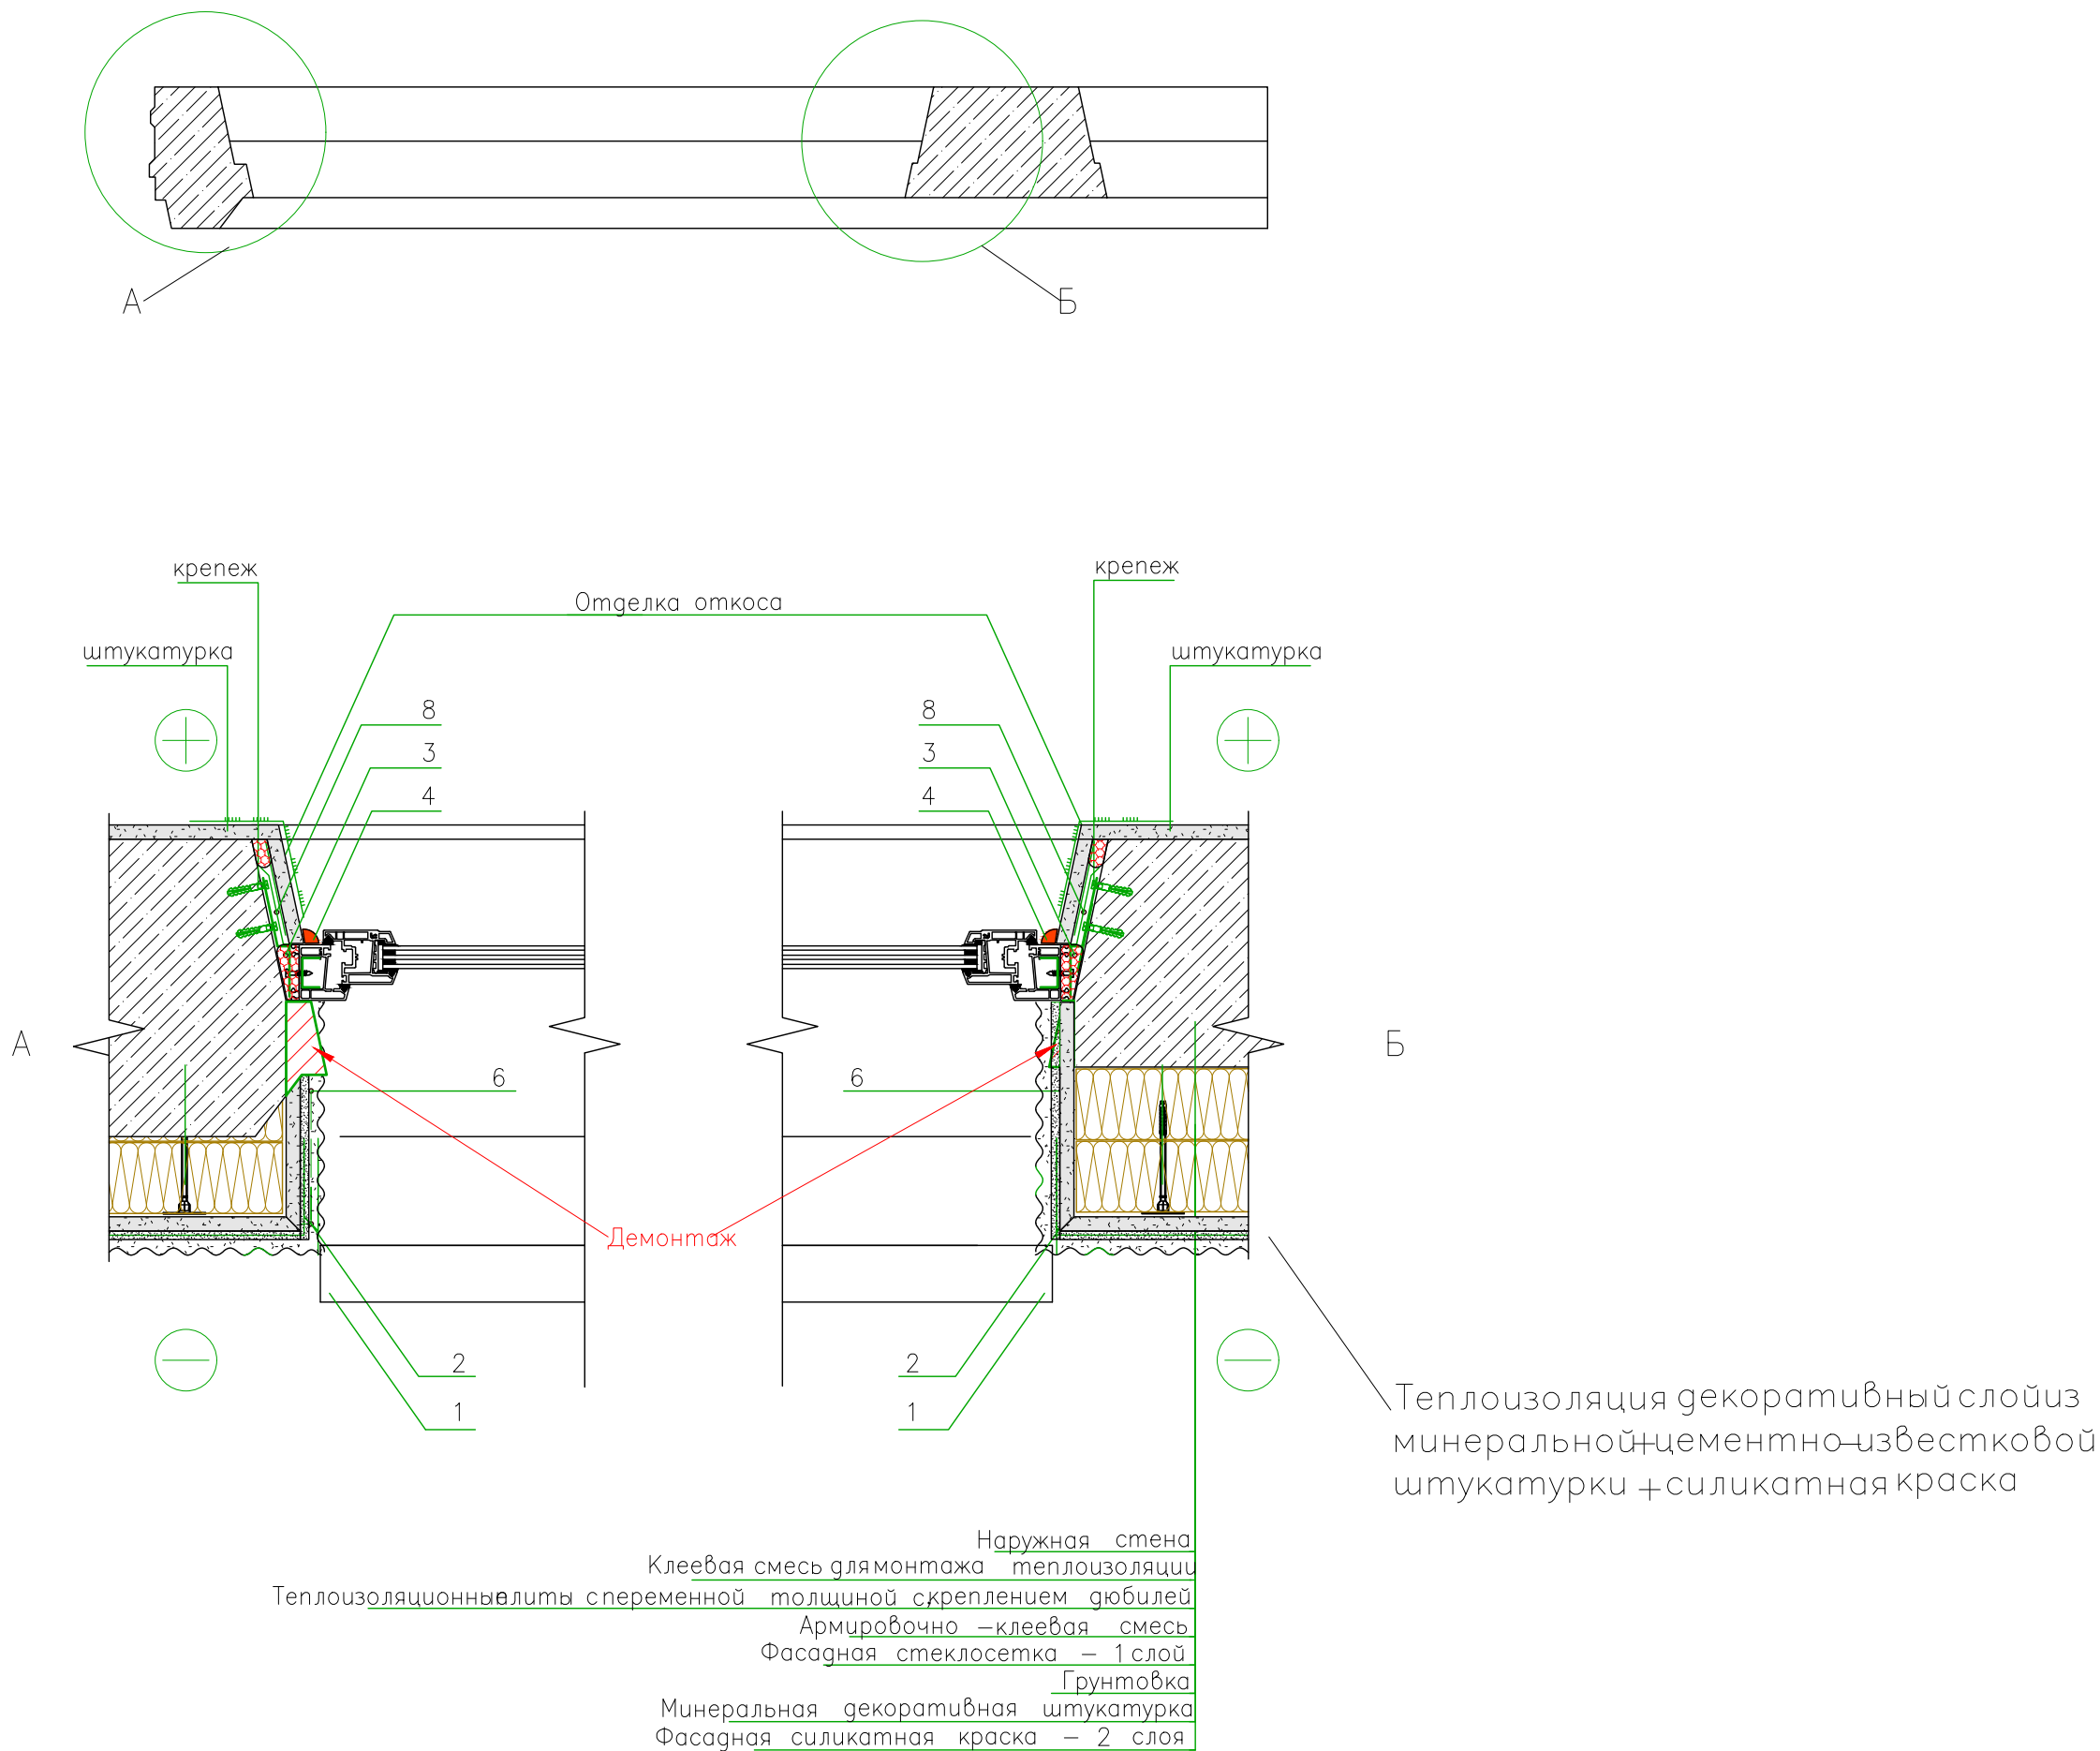

Спецификация на узел

Поз.	Наименование	Расход	Ед.изм.	Примечание
1	Отлив из оцинкованной стали	по проекту	м.п.	
2	Угловой ПВХ профиль с арм сеткой капельником	по проекту	м.п.	
3	Монтажная пена	по проекту		
4	Герметик универсальный нейтр силиконовый	по проекту		
5	Угловой ПВХ профиль с капельником с арм сеткой	по проекту	м.п.	
6	Оконный ПВХ профиль примыкания с арм сеткой	по проекту	м.п.	
7	Паропроницаемый герметик или лента	по проекту	м.п.	
8	Паронепроницаемый герметик или лента	по проекту	м.п.	

									205-25-AP
									Капитальный ремонт здания Государственное бюджетное общеобразовательное учреждение города Москвы "Школа № 1492, расположенного по адресу : ул. Адмирала Лазарева, д. 62, к. 2
Изм.	Кол.уч.	Лист	№ док	Подпись	Дата	Разраб.	Китов	Визов	02.26
									Объемно-планировочные и архитектурные решения
									П
									Узлы
Н. контр	Казаков				02.26	ГИП	Гаршин		02.26
									Общество с ограниченной ответственностью ГК "АЛЬФА-СТРОЙ"