

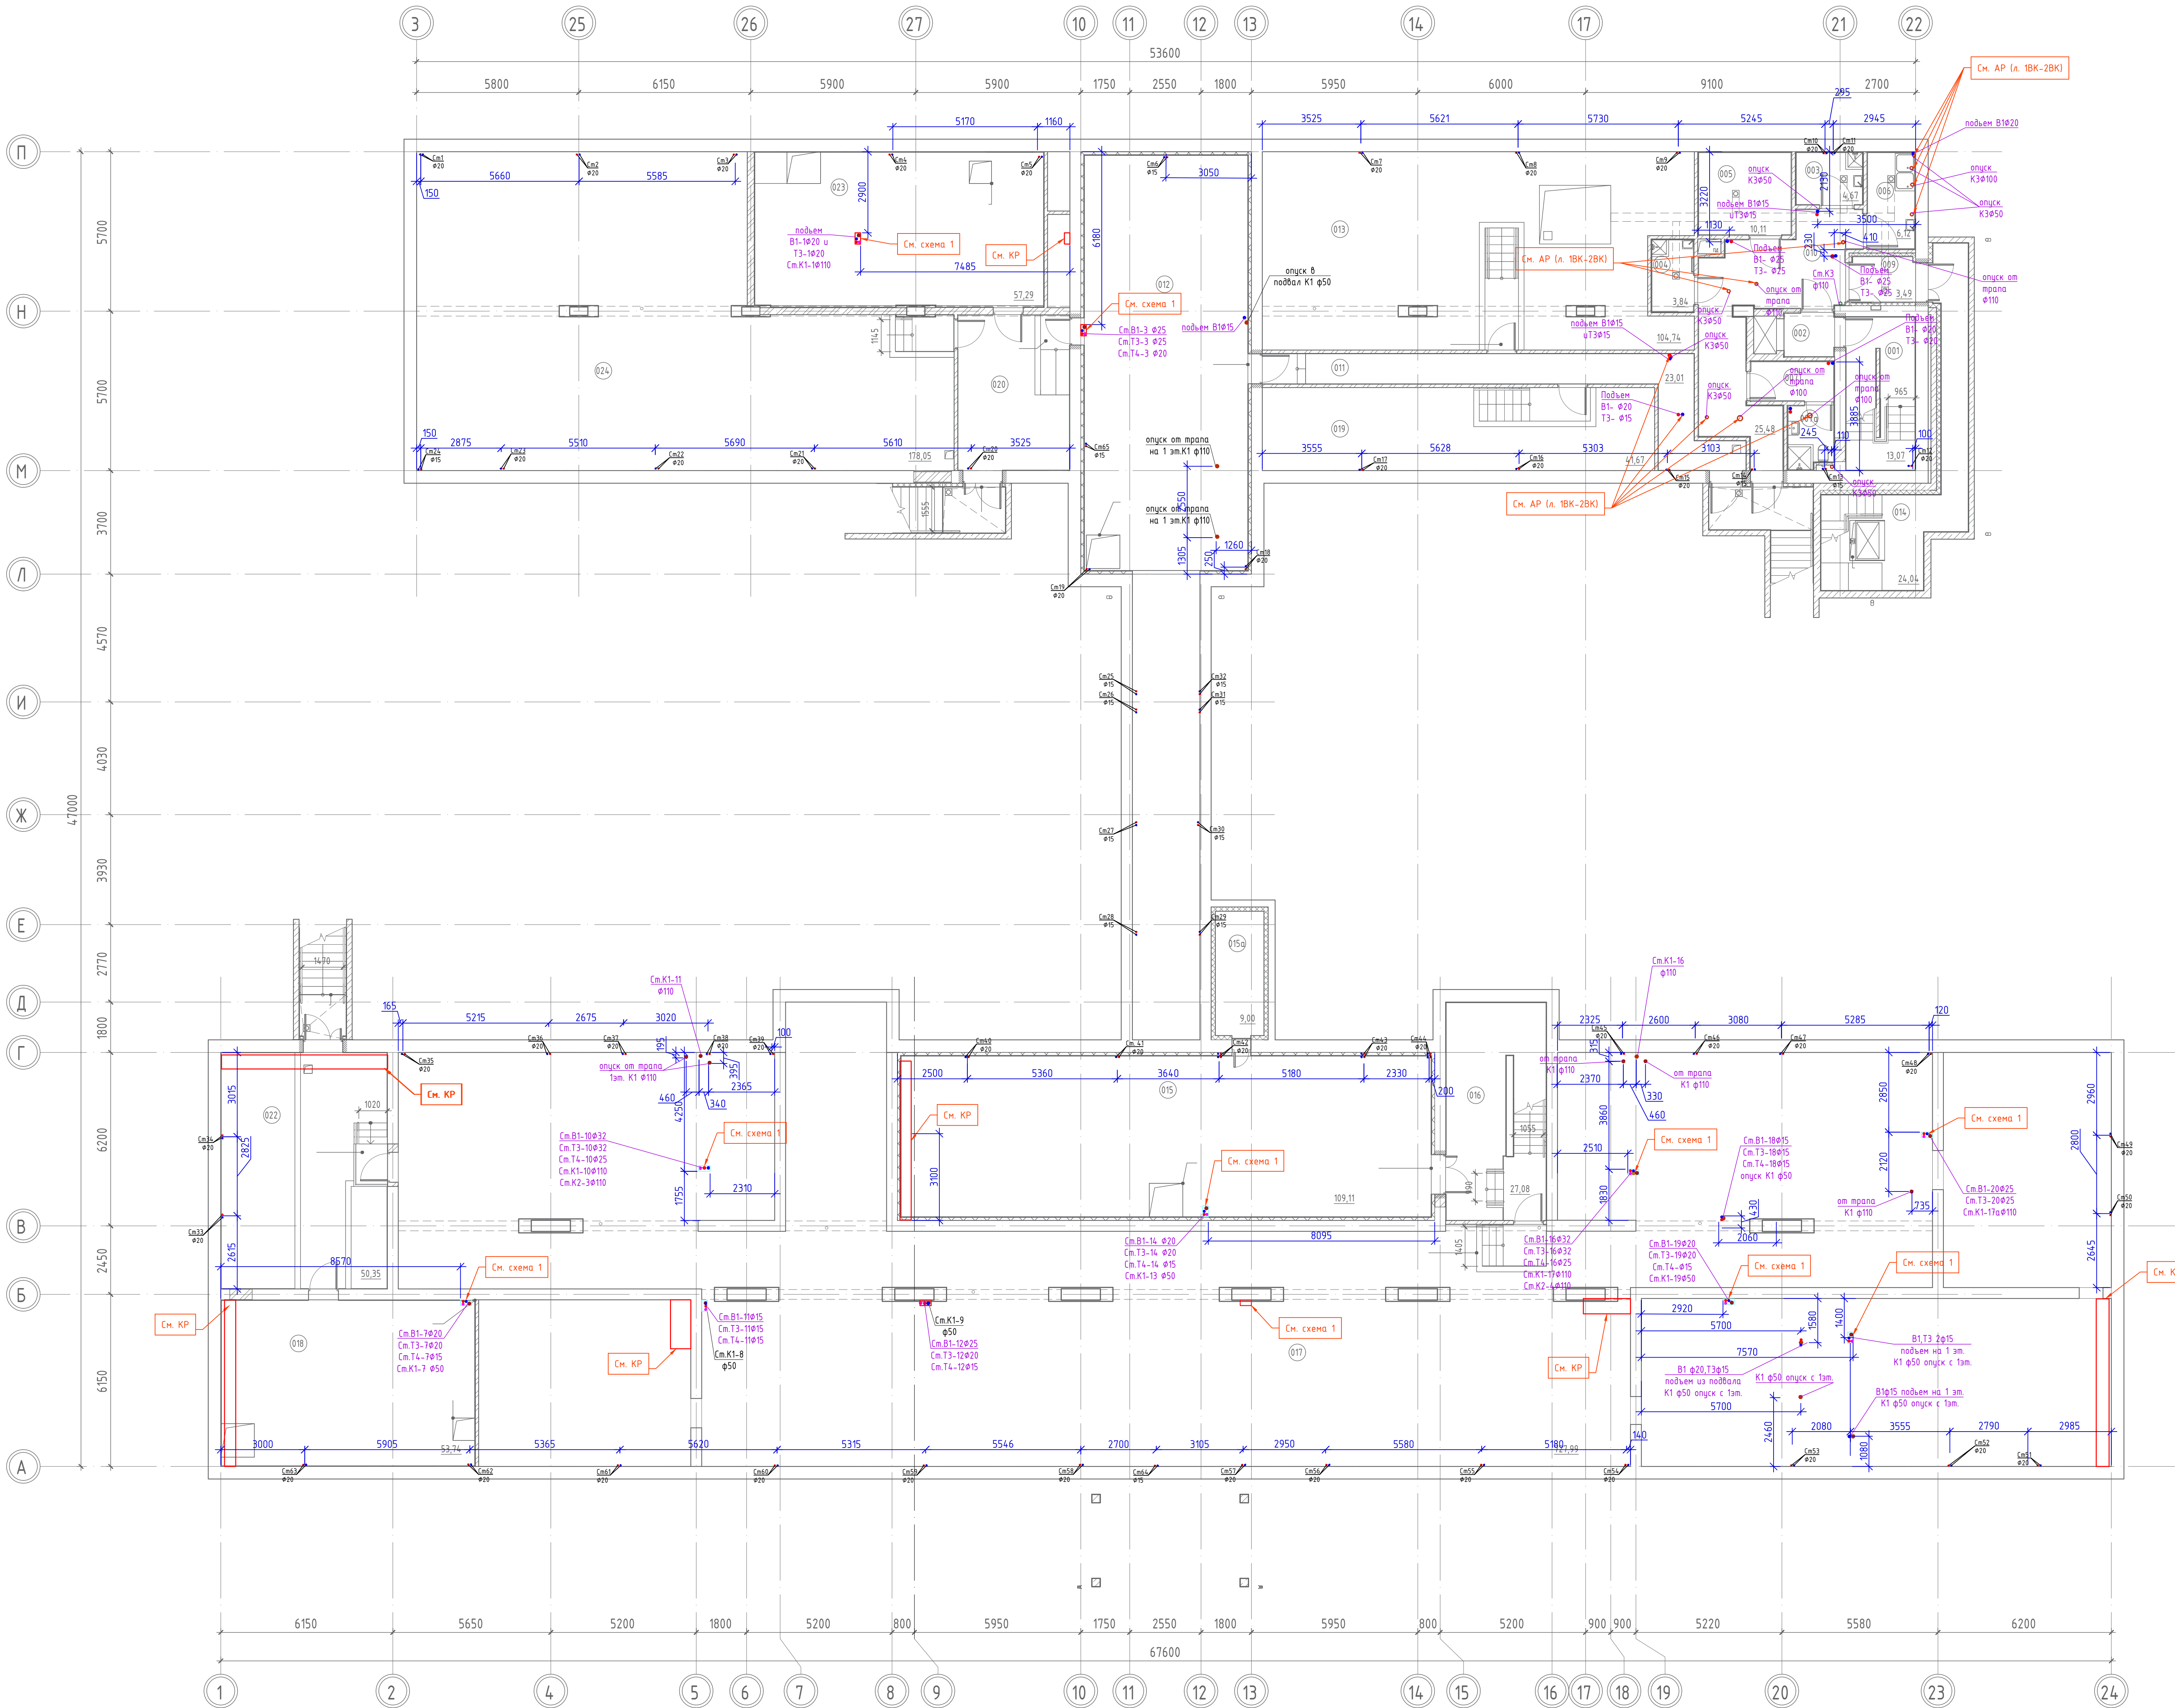
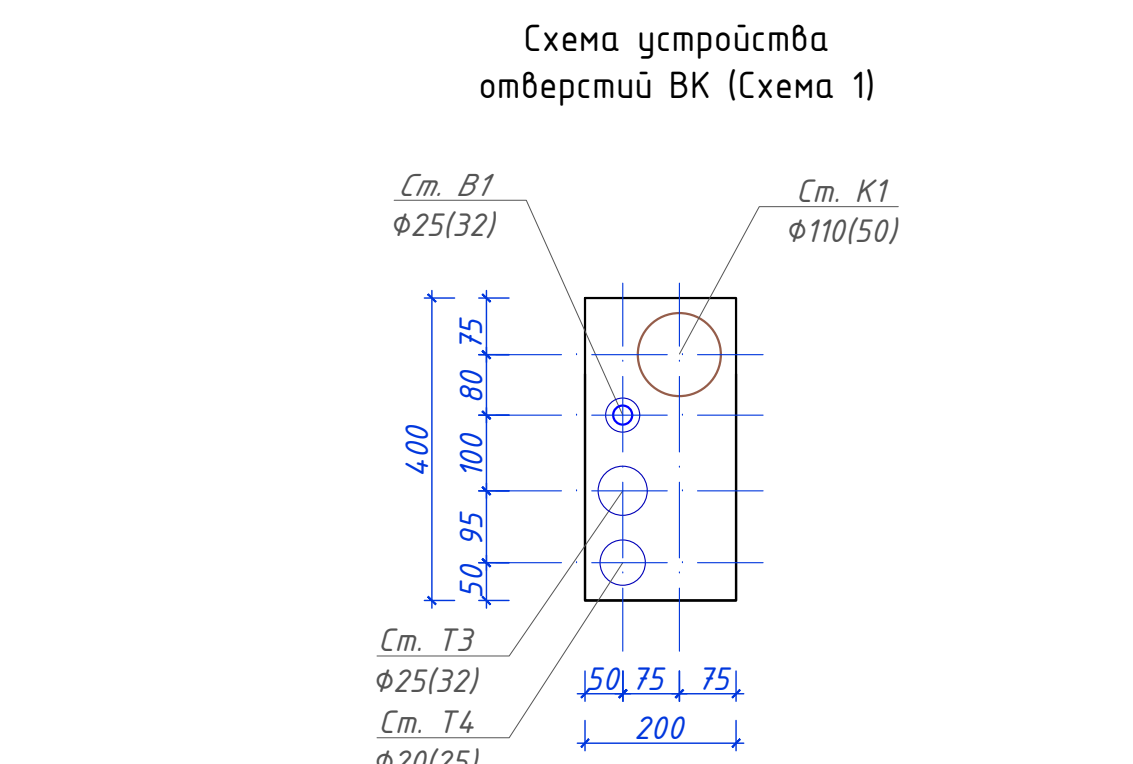


План привязки проходок инженерных систем  
(ВК, Отопление, Кондиционирование)  
в плитах перекрытия подвала

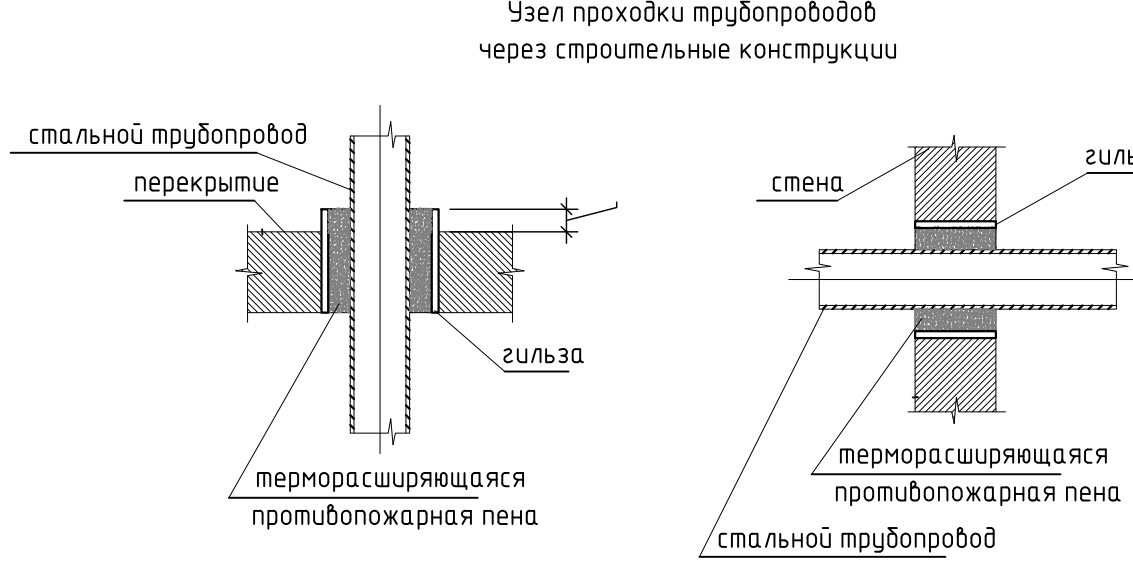


| Экспликация помещений подвала |                                                        |             |                |
|-------------------------------|--------------------------------------------------------|-------------|----------------|
| Номер помещения               | Наименование                                           | Площадь, м² | Кол. помещений |
| 001                           | Технологическая лестница                               | 13,07       |                |
| 002                           | Тамбур-шлюз                                            | 2,74        |                |
| 003                           | Помещение для временного хранения пищевых отходов      | 4,67        | Б4             |
| 004                           | Помещение для хранения уборочного инвентаря (Помойная) | 3,84        | Б4             |
| 005                           | Помещение с местом установки холодильного оборудования | 10,11       | Б3             |
| 006                           | Кладовая и моечная обратной тары                       | 6,12        | Б4             |
| 007                           | Помещение для персонала                                | 4,42        |                |
| 007а                          | Санузел персонала с душевой                            | 3,59        |                |
| 009                           | Зеленый цех                                            | 3,44        | Б4             |
| 010                           | Коридор                                                | 25,48       |                |
| 011                           | Коридор                                                | 22,40       |                |
| 012                           | Вентилятор                                             | 127,83      | Б4             |
| 013                           | Техническое помещение для прокладки инженерных сетей   | 103,70      | Б4             |
| 014                           | Зона заправки                                          | 24,04       | Б3             |
| 015                           | Вентилятор                                             | 109,11      | Б4             |
| 016                           | Лестничная клетка (плита П)                            | 27,08       |                |
| 017                           | Техническое помещение для прокладки инженерных сетей   | 728,04      | Б4             |
| 018                           | Водонапорный цех                                       | 53,74       | Б4             |
| 019                           | Техническое помещение для прокладки инженерных сетей   | 41,67       | Б4             |
| 020                           | Коридор                                                | 22,12       |                |
| 022                           | Коридор                                                | 50,35       |                |
| 023                           | ИТП                                                    | 57,16       | Б4             |
| 024                           | Техническое помещение для прокладки инженерных сетей   | 178,05      | Б4             |
|                               |                                                        | 1622,77     |                |

| Экспликация технических пространств подвала |              |             |                |
|---------------------------------------------|--------------|-------------|----------------|
| Номер помещения                             | Наименование | Площадь, м² | Кол. помещений |
| 015а                                        | Воздухозабор | 9,69        |                |
|                                             |              | 9,69        |                |

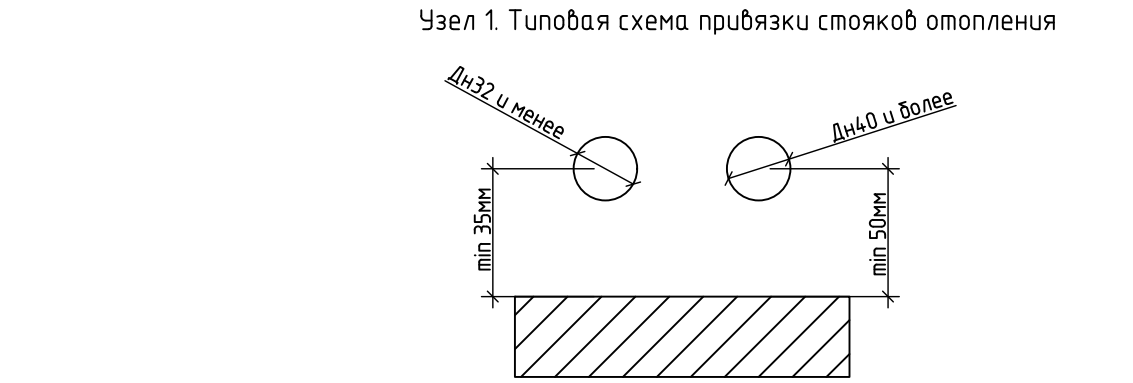


- Примечание**
- Размер гильз под каждый трубопровод принять на диаметр больше самого трубопровода (трубопровод Ø20 гильза Ø32, трубопровод Ø15 – гильза Ø25)
  - Привязки даны в проектных значениях с сохранением вертикали прокладки инженерных систем. Допускается отклонение от проектных привязок для сохранения вертикали систем по месту.
  - Отверстия для вертикальных инженерных систем выполнять без разрешения рабочей арматуры плиты перекрытия.
  - Запрещено использовать ручной инструмент, не позволяющий проконтролировать ход выполнения работы, в части сохранения целостности рабочей арматуры плиты перекрытия.

План привязки проходок инженерных систем  
(ВК, Отопление, Кондиционирование)  
в плитах перекрытия 1-ого этажа

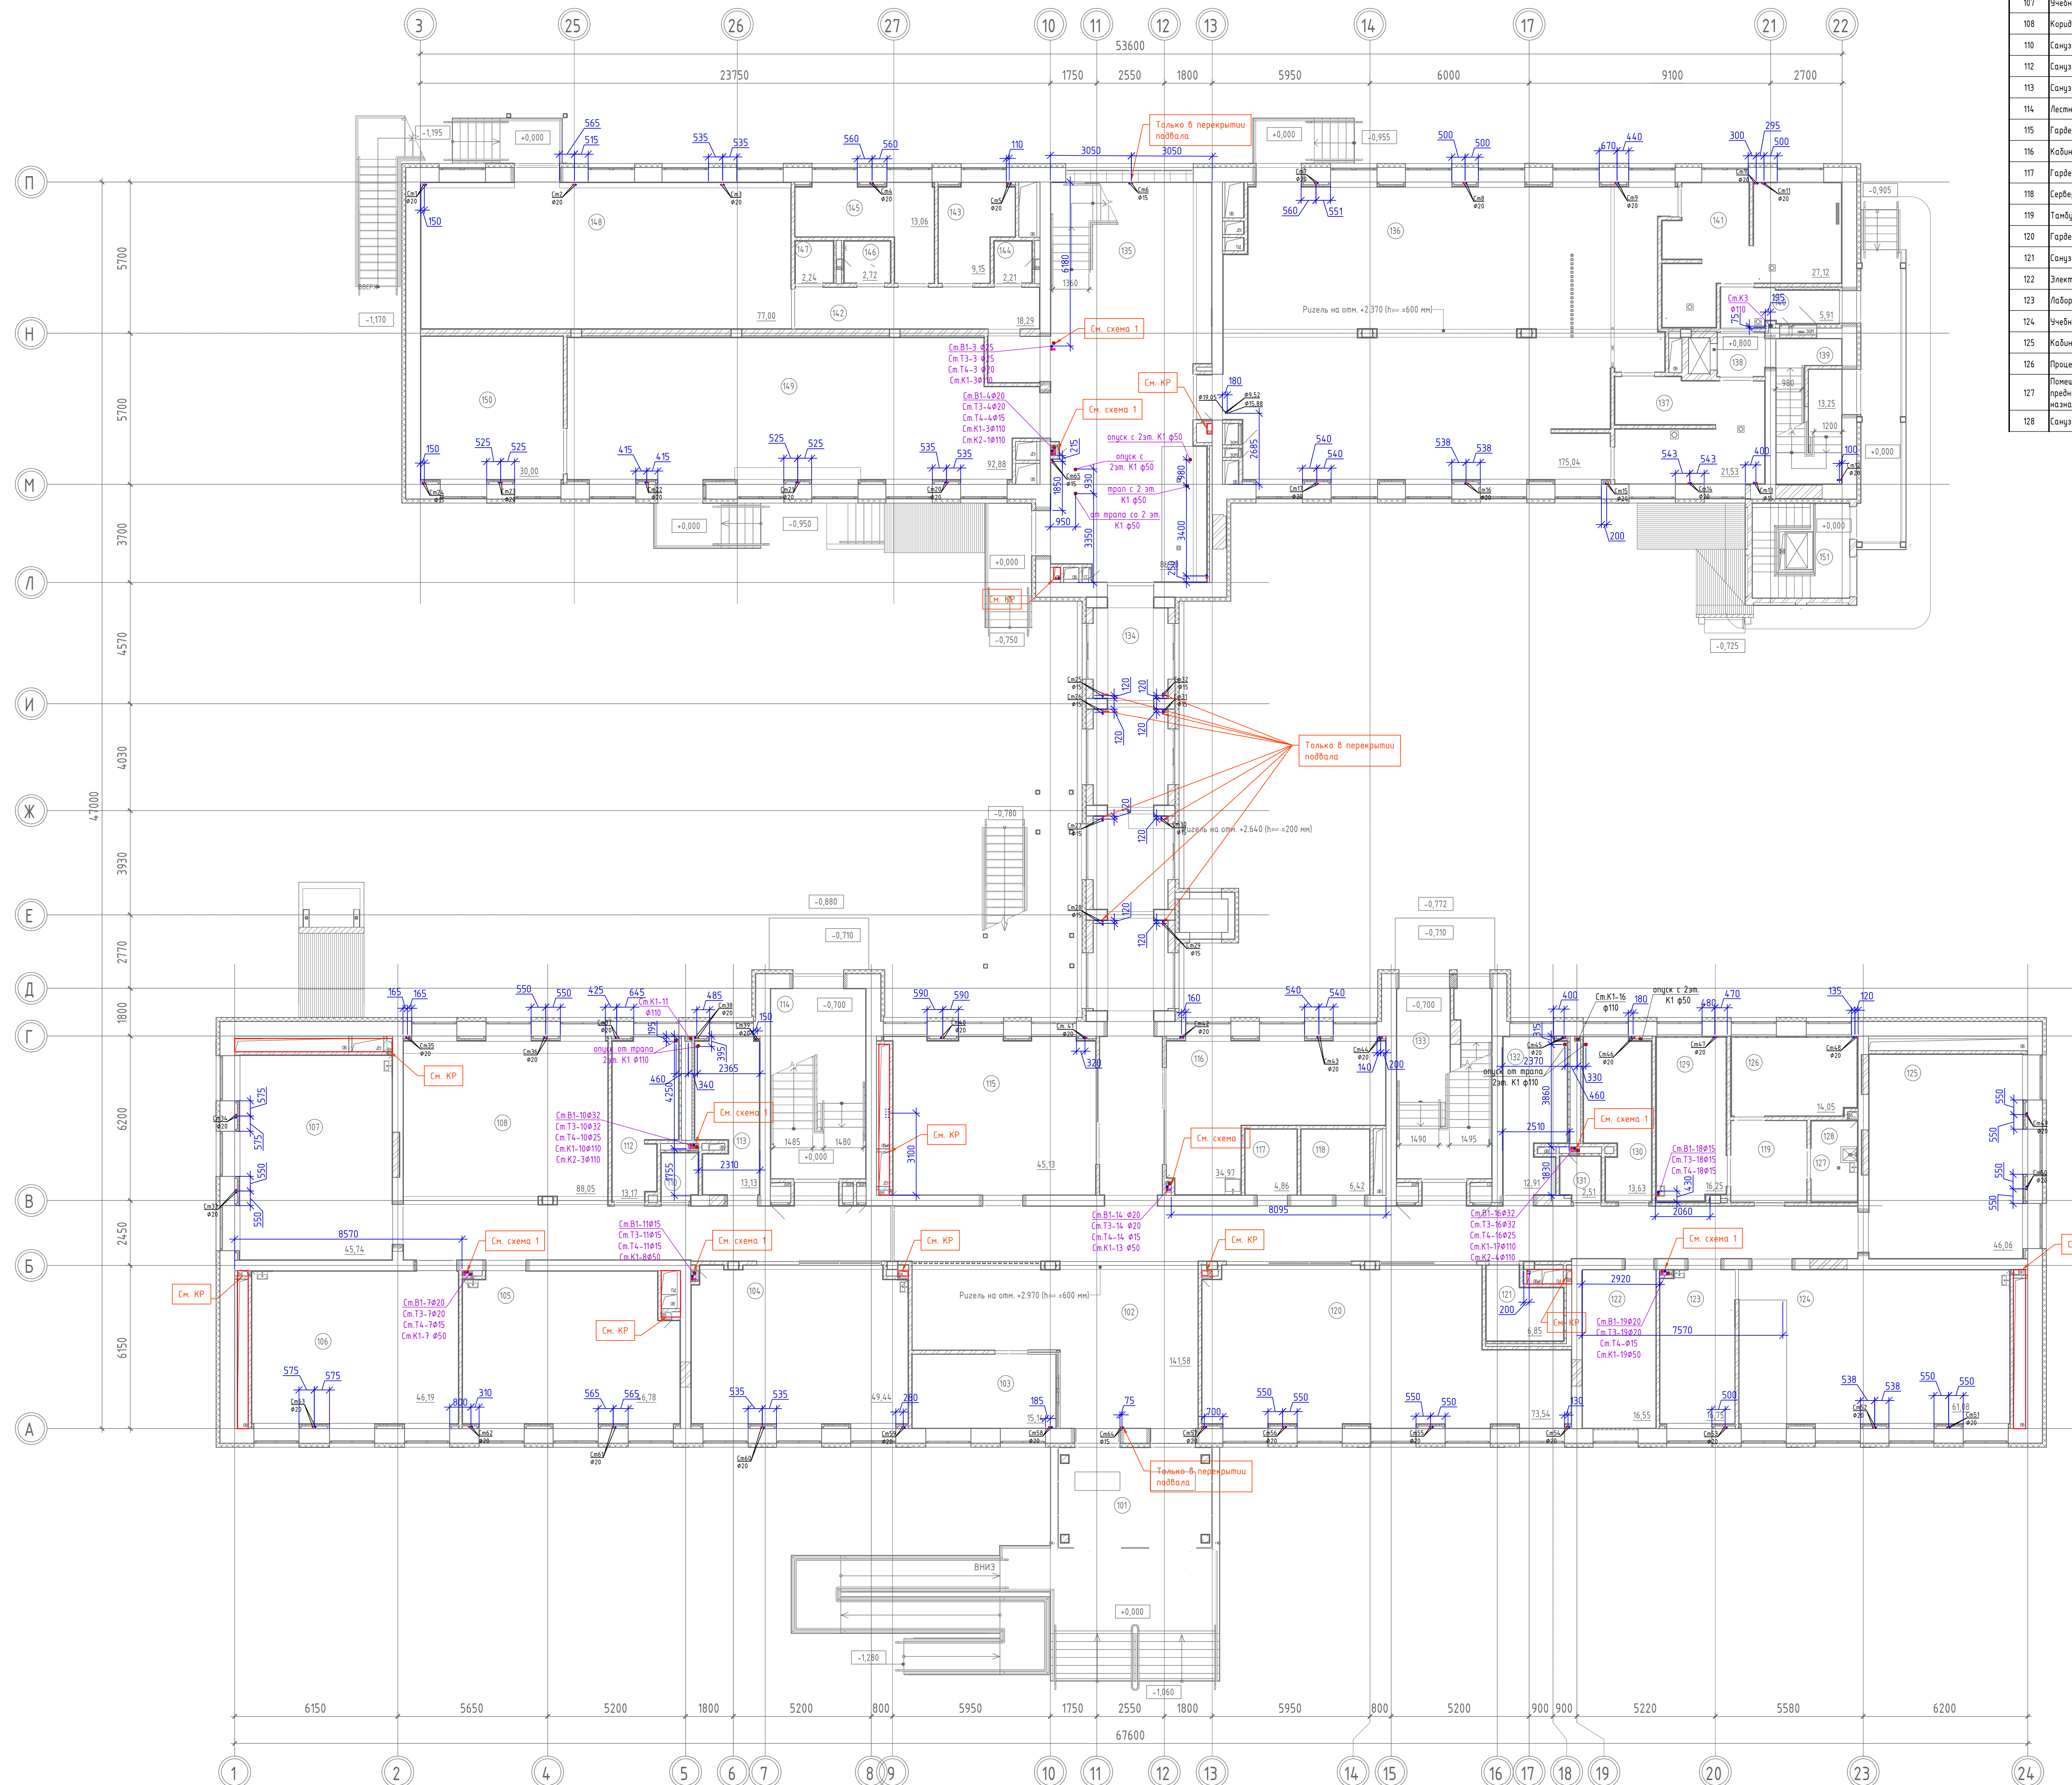

| Экспликация помещений первого этажа |   |             |                | Экспликация помещений первого этажа |                                                                           |             |                |
|-------------------------------------|---|-------------|----------------|-------------------------------------|---------------------------------------------------------------------------|-------------|----------------|
| Номер помеще- ния                   | Наименование                                                                                                 | Площадь, м² | Комплек- сация | Номер помеще- ния                   | Наименование                                                              | Площадь, м² | Комплек- сация |
| 101                                 | Танцзал   | 21,46       |                | 129                                 | Кабинет врача (площадью не менее 5,5 м²)                                  | 16,25       |                |
| 102                                 | Вестибюль   | 14,158      |                | 130                                 | Санузел для девочек с комнатой личной гигиены                             | 13,59       |                |
| 103                                 | Комната охраны с диспетчерским пунктом                                                                       | 15,14       |                | 131                                 | ПМБ                                                                       | 2,71        | Б4             |
| 104                                 | Учебный кабинет                                                                                              | 49,44       |                | 132                                 | Санузел для мальчиков                                                     | 13,00       |                |
| 105                                 | Учебный кабинет                                                                                              | 46,78       |                | 133                                 | Лестничная клетка (этажа II)                                              | 45,27       |                |
| 106                                 | Учебный кабинет                                                                                              | 46,19       |                | 134                                 | Коридор                                                                   | 23,34       |                |
| 107                                 | Учебный кабинет                                                                                              | 45,74       |                | 135                                 | Лестничная клетка (этажа III)                                             | 86,98       |                |
| 108                                 | Коридор с рекреацией                                                                                         | 88,05       |                | 136                                 | Общественный зал                                                          | 175,77      |                |
| 110                                 | Санузел персонала                                                                                            | 2,45        |                | 137                                 | Мечеть для столовой посуды                                                | 215,3       | Б4             |
| 112                                 | Санузел для мальчиков                                                                                        | 13,31       |                | 138                                 | Коридор пищеблока                                                         | 2,96        |                |
| 113                                 | Санузел для девочек                                                                                          | 13,27       |                | 139                                 | Лестничная клетка (этажа III)                                             | 13,25       |                |
| 114                                 | Лестничная клетка (этажа III)                                                                                | 25,65       |                | 140                                 | Коридор пищеблока                                                         | 5,91        |                |
| 115                                 | Гардероб для обучающихся                                                                                     | 45,13       |                | 141                                 | Помещение подсобного блока с репродуктор с участком мойки кухонной посуды | 27,12       | Б4             |
| 116                                 | Кабинет с рабочим пространством для учителей пун 1                                                           | 34,97       |                | 142                                 | Коридор                                                                   | 18,29       |                |
| 117                                 | Гардеробная комната (для учителей)                                                                           | 4,86        |                | 143                                 | Раздевалка мужская                                                        | 9,36        |                |
| 118                                 | Серверная   | 6,42        | Б3             | 144                                 | Туалет мужской                                                            | 2,21        |                |
| 119                                 | Танцзал   | 8,81        |                | 145                                 | Раздевалка женская                                                        | 13,38       |                |
| 120                                 | Гардероб для обучающихся                                                                                     | 73,54       |                | 146                                 | ПМБ                                                                       | 2,72        | Б4             |
| 121                                 | Санузел для МПБ на 1-м этаже                                                                                 | 6,85        |                | 147                                 | Туалет женский                                                            | 2,24        |                |
| 122                                 | Электрощитовая                                                                                               | 16,55       | Б3             | 148                                 | Гимнастический зал                                                        | 77,00       |                |
| 123                                 | Лаборатория кабинета химии                                                                                   | 16,75       | Б3             | 149                                 | Библиотека                                                                | 93,09       |                |
| 124                                 | Учебный кабинет для изучения естественных наук                                                               | 61,08       |                | 150                                 | Кинотеатр                                                                 | 30,00       | Б3             |
| 125                                 | Кабинет наемного                                                                                             | 44,06       |                | 151                                 | Детский пищеблок                                                          | 13,10       | Б3             |
| 126                                 | Проектиров (пробирочный) кабинет                                                                             | 16,05       |                | Итого помещений:                    |                                                                           | 958,50      |                |
| 127                                 | Помещение без раздаточной и уборочного инвентаря, предельно ограничено для помещений медицинского назначения | 3,63        | Б4             |                                     |                                                                           |             |                |
| 128                                 | Санузел пищеблока                                                                                            | 1,67        |                |                                     |                                                                           |             |                |

Узел 1 Типовая схема привязки стояков отопления

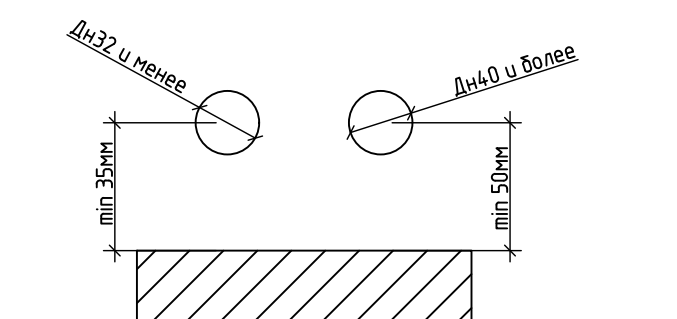

Узел проходки трубопроводов  
через строительные конструкции


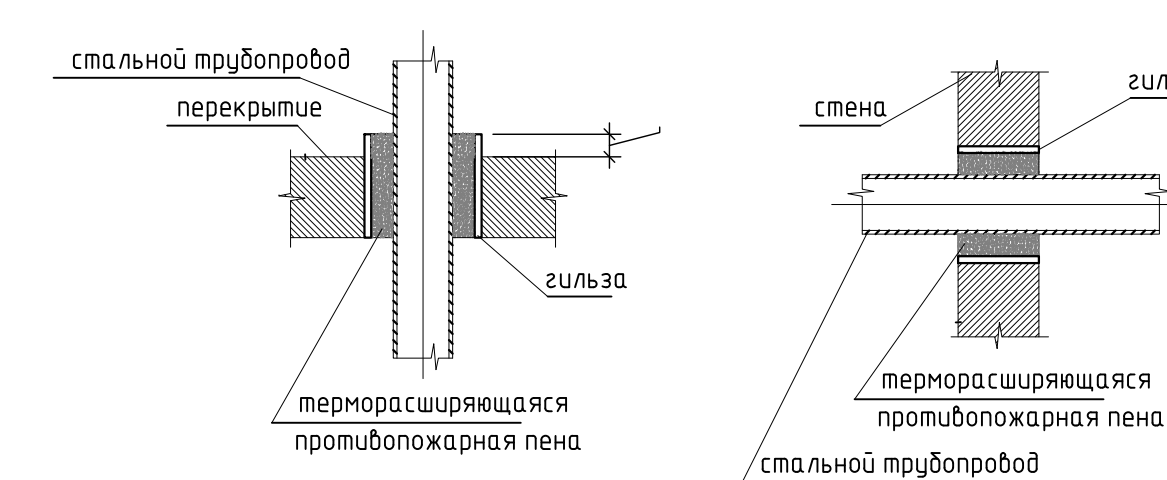


Схема устройства  
отверстий ВК (Схема 1)

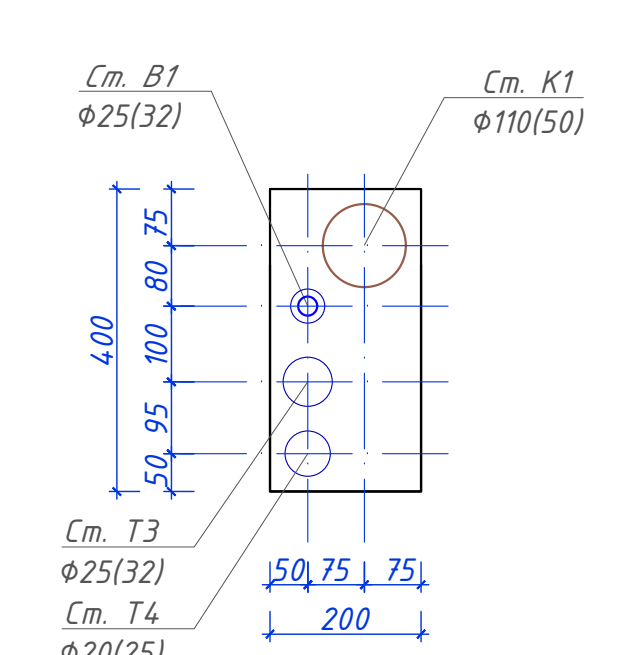


Примечание

- Размер гильз под каждый трубопровод принять на диаметр больше самого трубопровода (трубопровод  $\varnothing 20$  гильза  $\varnothing 32$ , трубопровод  $\varnothing 15$  – гильза  $\varnothing 25$ )
- Привязки даны в проектных значениях с сохранением вертикали прокладок инженерных систем. Допускается отклонение от проектных привязок для сохранения вертикали систем по месту
- Отверстия для вертикальных инженерных систем выполнять без разрушения рабочей арматуры плиты перекрытия.
- Запрещено использовать ручной инструмент, не позволяющий контролировать ход выполнения работы, в части сохранения целостности рабочей арматуры плиты перекрытия.


|                |         |                  |       |                |   |  |  |                                                                                       |  |  |
|----------------|---------|------------------|-------|----------------|---|--|--|---------------------------------------------------------------------------------------|--|--|
|                |         |                  |       |                | 708/П-24 - АНО –АР                                                                                                |  |  |                                                                                       |  |  |
|                |         |                  |       |                | Капитальный ремонт общеобразовательного учреждения (ГБОУ Школа № 1210) по адресу: г. Москва, ул. Хивинская, д. 32 |  |  |                                                                                       |  |  |
| Изм.           | Кол.ум. | Лист № док.      | Подп. | Дата           |   |  |  |                                                                                       |  |  |
| Разработка ГАП |         | Федосова Еролова |       | 06.26<br>06.26 | Архитектурные решения                                                                                             |  |  |                                                                                       |  |  |
|                |         |                  |       |                | Таблица   |  |  | Листов                                                                                |  |  |
|                |         |                  |       |                | Р   |  |  | 2                                                                                     |  |  |
|                |         |                  |       |                | План распространяется технологического оборудования и мебели                                                      |  |  |                                                                                       |  |  |
|                |         |                  |       |                | 1 этаж   |  |  |  |  |  |
| Н.Контроль ИГИ |         | Лукашова         |       | 06.26<br>06.26 |   |  |  | ООО "АТИСМ"                                                                           |  |  |
|                |         |                  |       |                |   |  |  | ИНН 77-07-000000 ОГРН 1047707000000                                                   |  |  |

План привязки проходок инженерных систем  
(ВК, Отопление, Кондиционирование)  
в плитах перекрытия 2-ого этажа

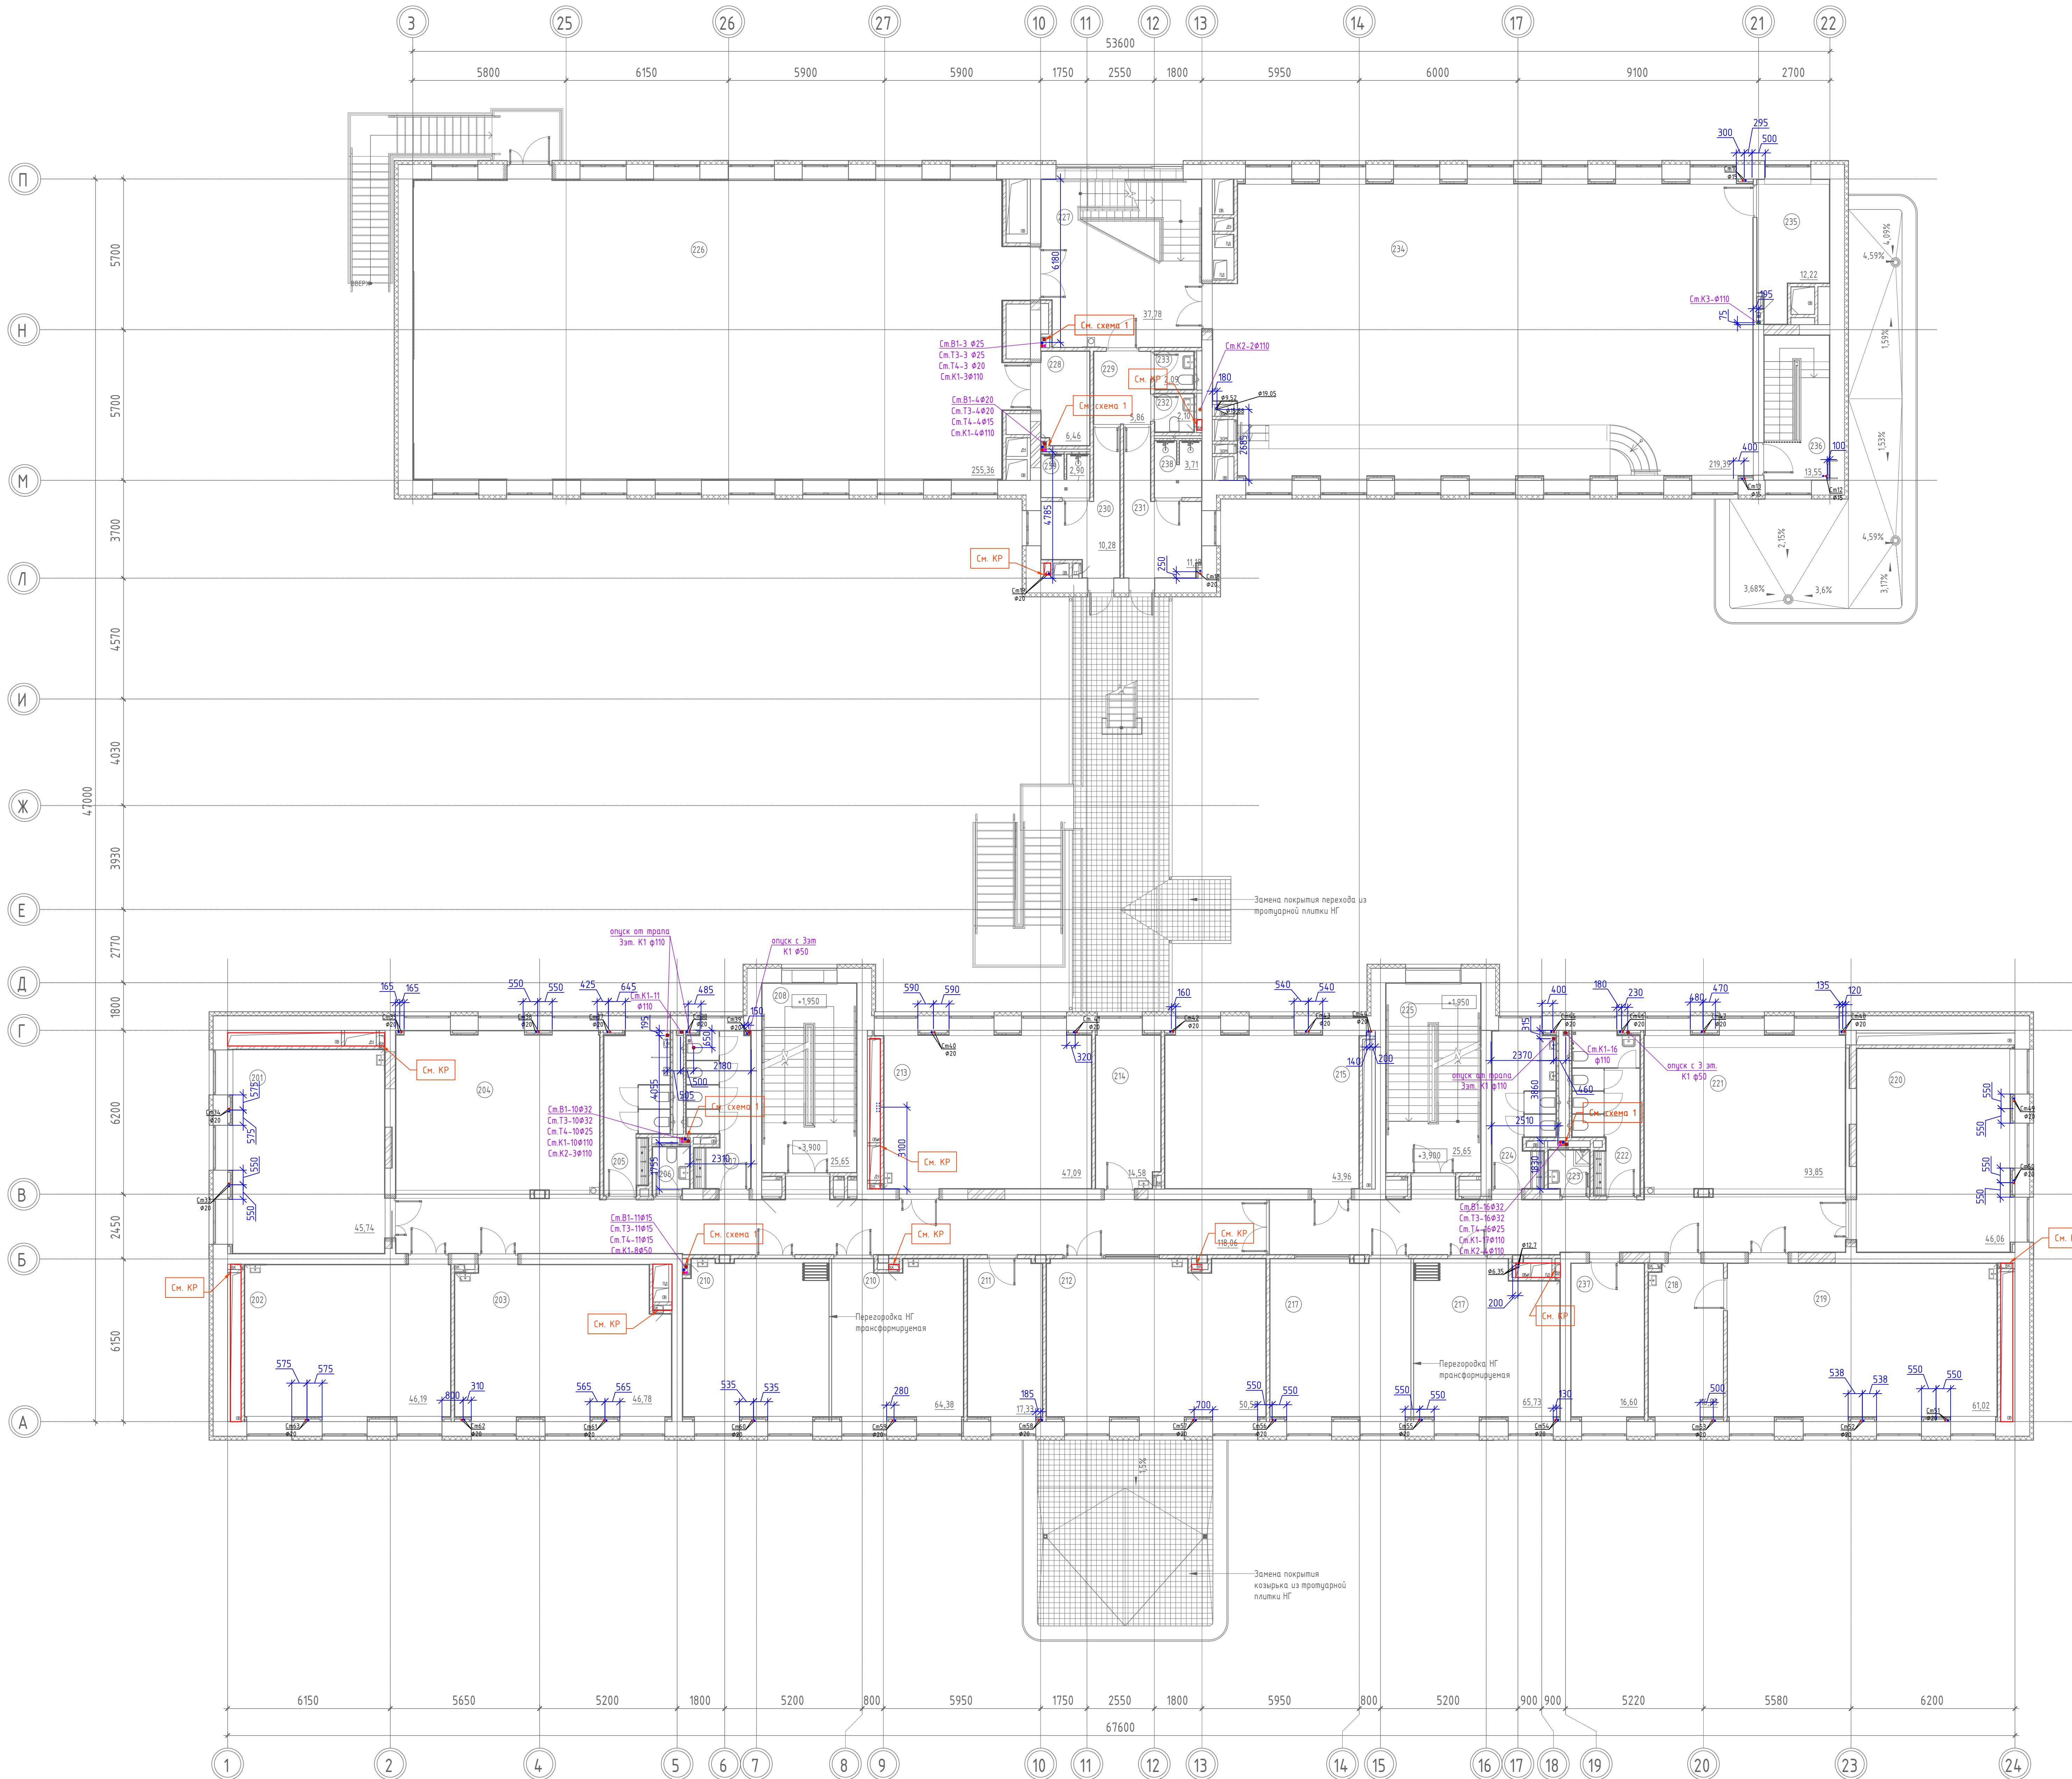

| Экспликация помещений второго этажа |                                                                   |             |                |
|-------------------------------------|-------------------------------------------------------------------|-------------|----------------|
| Номер помещения                     | Наименование                                                      | Площадь, м² | Кол. помещений |
| 201                                 | Учебный кабинет                                                   | 45,74       |                |
| 202                                 | Учебный кабинет                                                   | 46,19       |                |
| 203                                 | Учебный кабинет                                                   | 46,78       |                |
| 204                                 | Коридор с рекреацией                                              | 118,66      |                |
| 205                                 | Санузел для мальчиков                                             | 13,29       |                |
| 206                                 | Санузел персонала                                                 | 2,47        |                |
| 207                                 | Санузел для девочек                                               | 13,27       |                |
| 208                                 | Лестничная клетка (типа П)                                        | 25,65       |                |
| 210                                 | Кабинет иностранного языка с трансформируемой перегородкой        | 64,38       |                |
| 211                                 | Административный кабинет                                          | 17,33       |                |
| 212                                 | Учебный кабинет                                                   | 50,58       |                |
| 213                                 | Учебный кабинет                                                   | 47,09       |                |
| 214                                 | Кабинет для индивидуальных занятий, в т.ч. с учителем-логопедом   | 14,58       |                |
| 215                                 | Кабинет математики                                                | 43,96       |                |
| 217                                 | Кабинет иностранного языка с трансформируемой перегородкой        | 65,73       |                |
| 218                                 | Лаборантская кабинета биологии и ОБЭР                             | 16,83       | Б3             |
| 219                                 | Учебный кабинет для изучения естественных наук                    | 61,02       |                |
| 220                                 | Кабинет ОБЭР                                                      | 46,06       |                |
| 221                                 | Коридор с рекреацией                                              | 93,85       |                |
| 222                                 | Санузел для девочек с комнатой личной гигиены                     | 13,79       |                |
| 223                                 | ПМ                                                                | 2,53        | В4             |
| 224                                 | Санузел для мальчиков                                             | 12,98       |                |
| 225                                 | Лестничная клетка (типа П)                                        | 25,65       |                |
| 226                                 | Спортивный зал                                                    | 256,26      |                |
| 227                                 | Лестничная клетка (типа П)                                        | 37,78       |                |
| 228                                 | Сварочная                                                         | 6,44        | Б3             |
| 229                                 | Коридор                                                           | 5,86        |                |
| 230                                 | Раздевалка мужская                                                | 10,28       |                |
| 231                                 | Раздевалка женская                                                | 11,30       |                |
| 232                                 | Туалет мужской                                                    | 2,10        |                |
| 233                                 | Туалет мужской                                                    | 2,09        |                |
| 234                                 | Актовый зал                                                       | 220,65      |                |
| 235                                 | Кладовая инвентаря                                                | 12,22       | Б3             |
| 236                                 | Лестничная клетка (типа П)                                        | 13,55       |                |
| 237                                 | Кабинет для индивидуальных занятий, в т.ч. с педагогом-психологом | 16,60       |                |
| 238                                 | Душевая женская                                                   | 3,71        |                |
| 239                                 | Душевая мужская                                                   | 2,90        |                |
| Общая площадь: 37                   |                                                                   | 1489,57     |                |

Узел 1 Типовая схема привязки стояков отопления

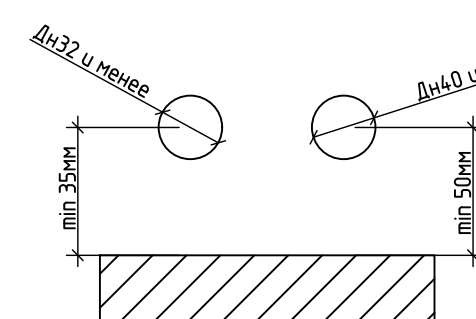

Узел проходки трубопровода через строительные конструкции


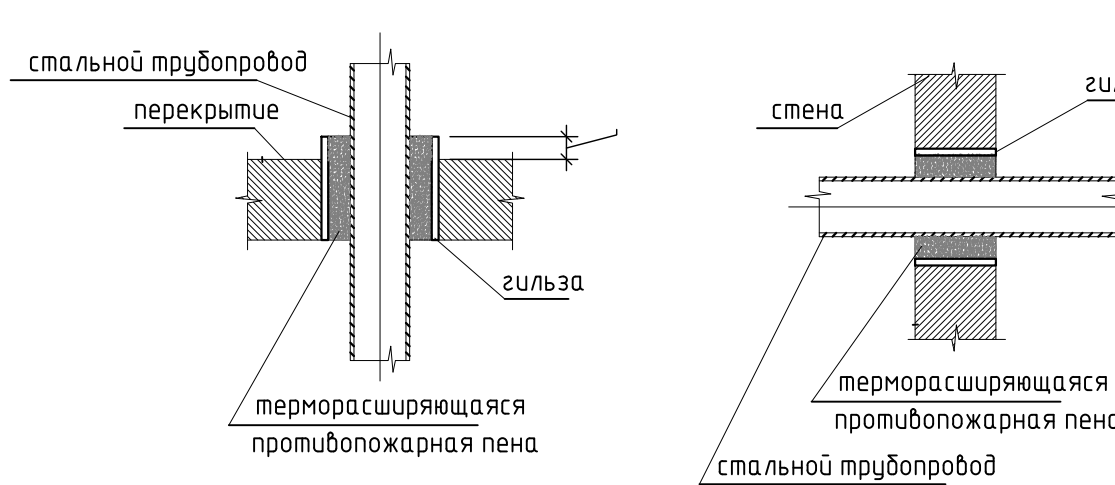


Схема устройства отверстий ВК (Схема 1)

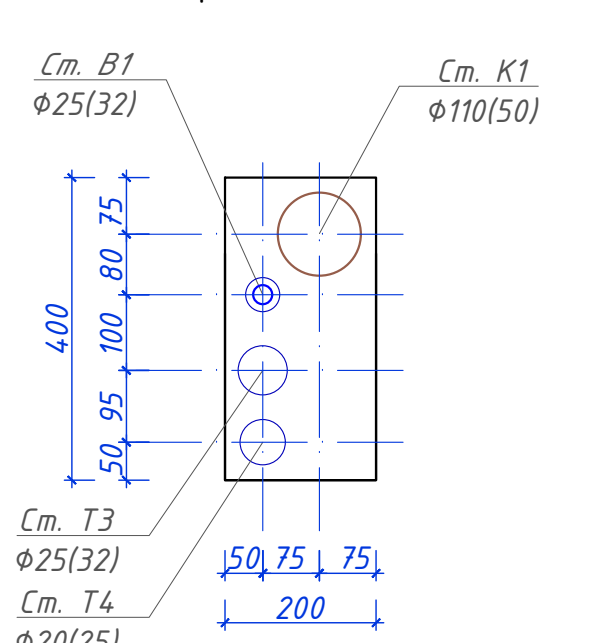


Примечание

- Размер гильз под каждый трубопровод принять на диаметр больше самого трубопровода (трубопровод  $\Phi 20$  гильза  $\Phi 32$ , трубопровод  $\Phi 15$  – гильза  $\Phi 25$ )
- Привязки даны в проектных значениях с сохранением вертикали прокладки инженерных систем. Допускается отклонение от проектных привязок для сохранения вертикали систем по месту.
- Отверстия для вертикальных инженерных систем выполнять без разрушения рабочей арматуры плиты перекрытия.
- Запрещено использовать ручной инструмент, не позволяющий проконтролировать ход выполнения работы, в части сохранения целостности рабочей арматуры плиты перекрытия.

|             |          |        |       |        |   |      |        |
|-------------|----------|--------|-------|--------|---|------|--------|
|             |          |        |       |        | 708/П-24-АНО-АР   |      |        |
|             |          |        |       |        | Капитальный ремонт общеобразовательного учреждения (ГБОУ Школа № 1210) по адресу: г. Москва, ул. Ждановская, д. 32 |      |        |
| Изм. Кол-во | Лист     | № док. | Подп. | Дата   | Страниц   | Лист | Листов |
| Разработчик | Фролова  |        |       | 06.26  | Р   | 3    |        |
| ГАП         | Фролова  |        |       | 06.26  | Архитектурные решения                                                                                              |      |        |
|             |          |        |       |        | План расстановки технологического оборудования и мебели                                                            |      |        |
| Н.Контроль  | Лукашова |        |       | 06.26  |  ООО "АРТИС"                  |      |        |
| ГАП         |          |        | 06.26 | 2 этаж |   |      |        |

План привязки проходок инженерных систем  
(ВК, Отопление, Кондиционирование)  
в плитах перекрытия 3-ого этажа

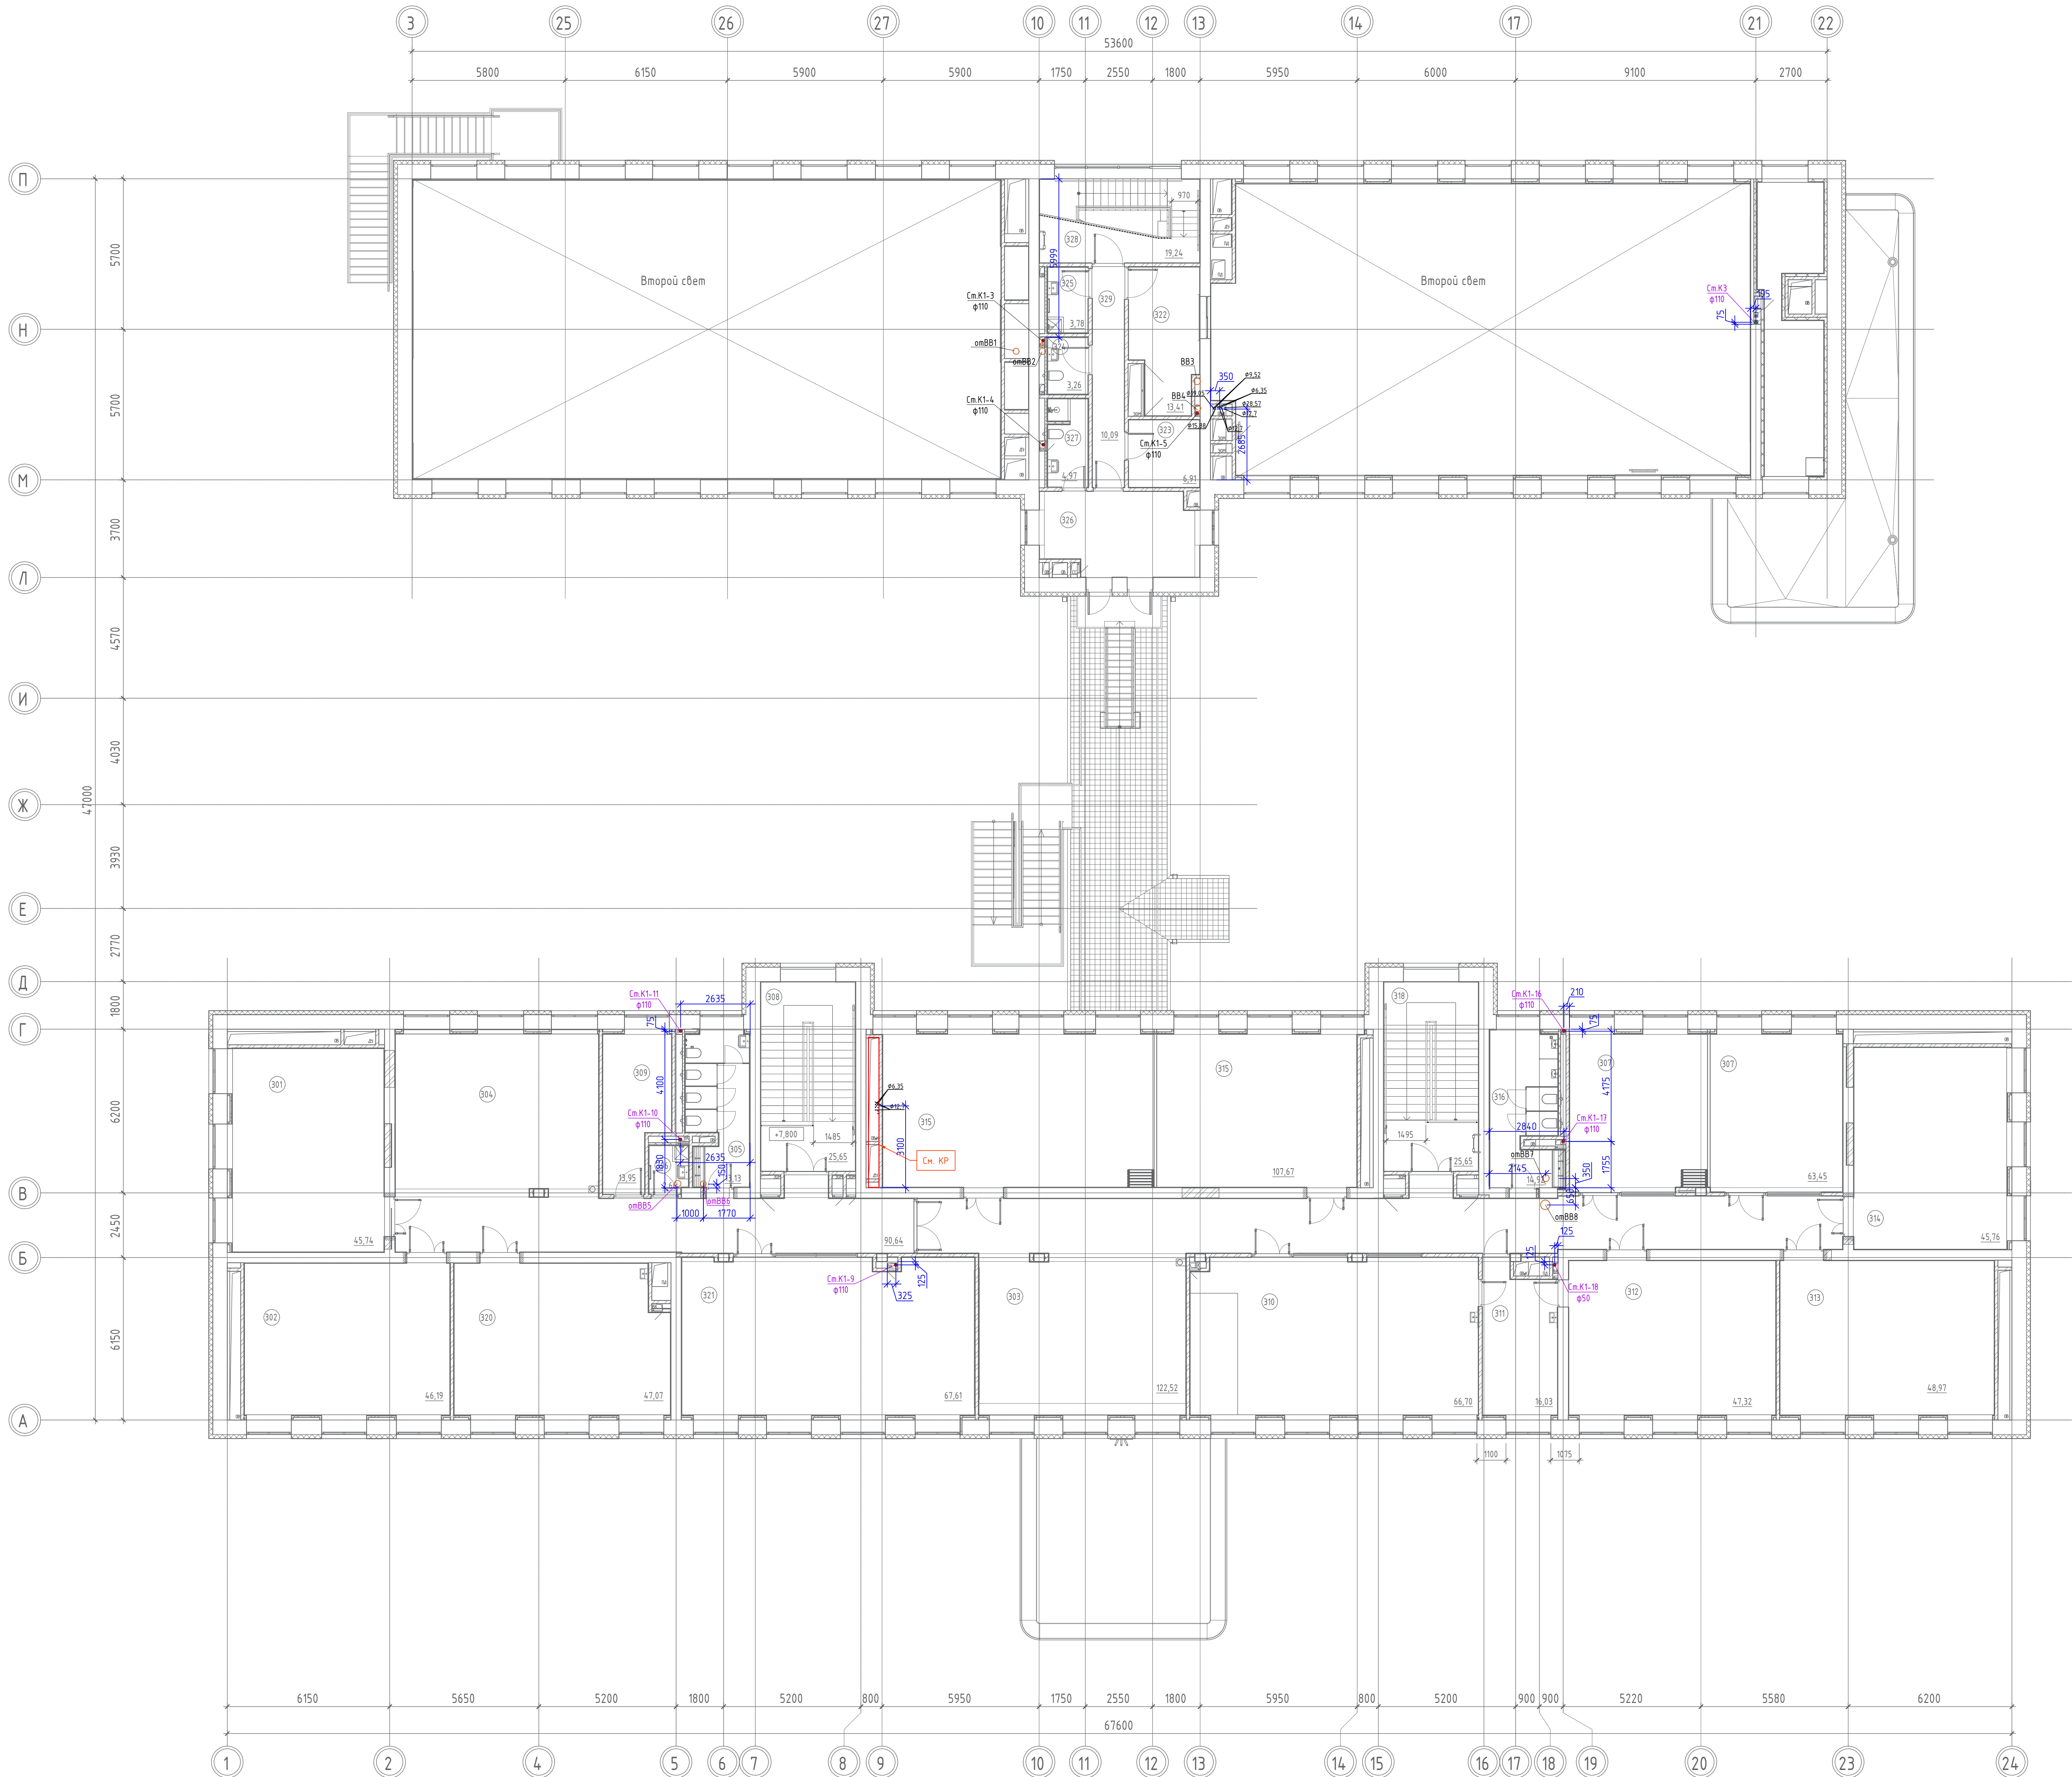

| Экспликация помещений третьего этажа |   |             |                |
|--------------------------------------|---|-------------|----------------|
| Номер помещения                      | Наименование   | Площадь, м² | Кот. помещения |
| 301                                  | Кабинет русского языка и литературы                                                                                   | 45,74       |                |
| 302                                  | Кабинет русского языка и литературы                                                                                   | 46,19       |                |
| 303                                  | Коридор с рекреацией                                                                                                  | 122,52      |                |
| 304                                  | Коридор с рекреацией                                                                                                  | 90,64       |                |
| 305                                  | Санузлы для девочек с комнатой личной гигиены                                                                         | 13,27       |                |
| 306                                  | ПМ   | 2,86        | В4             |
| 307                                  | Учебный кабинетностранного языка с возможностью деления трансформируемой перегородкой на два помещения                | 63,45       |                |
| 308                                  | Лестничная клетка (тип А)                                                                                             | 25,65       |                |
| 309                                  | Административный кабинет                                                                                              | 13,95       |                |
| 310                                  | Учебный кабинет для изучения естественных наук                                                                        | 66,70       |                |
| 311                                  | Лаборатория кабинета физики                                                                                           | 16,03       | В3             |
| 312                                  | Кабинет физики (универсальный)                                                                                        | 47,32       |                |
| 313                                  | Кабинет акварели   | 48,97       |                |
| 314                                  | Кабинет истории Топ1                                                                                                  | 45,76       |                |
| 315                                  | Кабинет информатики и информационных технологий с возможностью деления трансформируемой перегородкой на два помещения | 107,67      |                |
| 316                                  | Санузлы для мальчиков                                                                                                 | 14,89       |                |
| 318                                  | Лестничная клетка (тип А)                                                                                             | 25,65       |                |
| 320                                  | Учебный кабинет   | 47,07       |                |
| 321                                  | Учебный кабинет   | 67,61       |                |
| 322                                  | Технический центр   | 13,41       | В3             |
| 323                                  | Серверная   | 6,91        | В3             |
| 324                                  | Санузел   | 3,36        |                |
| 325                                  | Помещение хранения уборочного инвентаря и приспособления дезинфицирующих растворов                                    | 3,78        | В4             |
| 326                                  | Комната инструктора                                                                                                   | 18,19       |                |
| 327                                  | Туалет инструктора   | 4,88        |                |
| 328                                  | Лестничная клетка (тип А)                                                                                             | 19,24       |                |
| 329                                  | Коридор   | 10,09       |                |
|                                      |   | 991,60      |                |

| Экспликация технических пространств третьего этажа |                          |             |                |
|----------------------------------------------------|--------------------------|-------------|----------------|
| Номер помещения                                    | Наименование             | Площадь, м² | Кот. помещения |
| 330                                                | Техническое пространство | 23,38       |                |
|                                                    |                          | 23,38       |                |


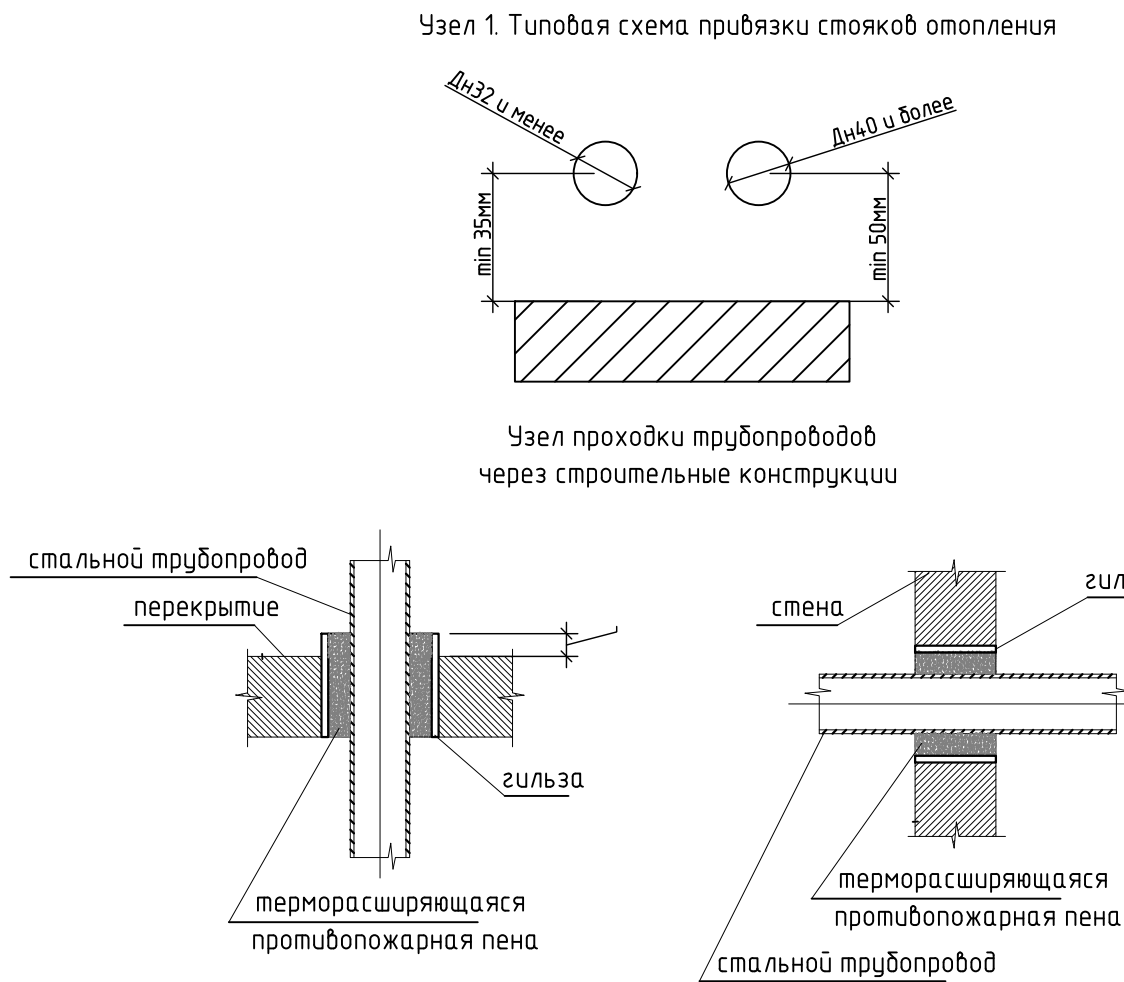


Схема устройства  
отверстий ВК (Схема 1)

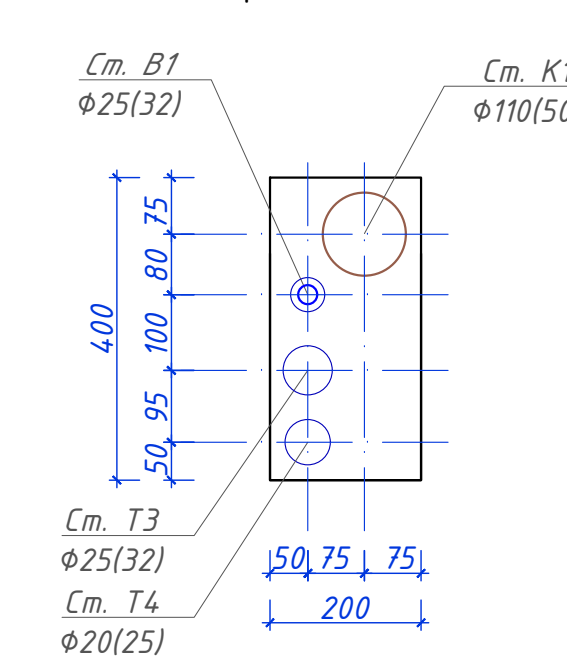

Примечание

- Размер гильз под каждый трубопровод принять на диаметр больше самого трубопровода (трубопровод  $\varnothing 20$  гильза  $\varnothing 32$ , трубопровод  $\varnothing 15$  – гильза  $\varnothing 25$ )
- Привязки даны в проектных значениях с сохранением вертикали прокладки инженерных систем. Допускается отклонение от проектных привязок для сохранения вертикали систем по месту.
- Отверстия для вертикальных инженерных систем выполнять без разрушения рабочей арматуры плиты перекрытия.
- Запрещено использовать ручной инструмент, не позволяющий проконтролировать ход выполнения работы, в части сохранения целостности рабочей арматуры плиты перекрытия.

|             |          |        |     |   |       |        |      |
|-------------|----------|--------|-----|---|-------|--------|------|
|             |          |        |     | 708/П-24-АНО-АР   |       |        |      |
|             |          |        |     | Капитальный ремонт общеобразовательного учреждения (ГБОУ Школа № 1210) по адресу: г. Москва, ул. Животновская, д. 32 |       |        |      |
| Исполн.     | Волков   | Лист № | Вик | Подп.   | Дата  | Статус | Лист |
| Разработчик | Волков   | 06.26  |     |   | 06.26 | Р      | 4    |
| ГАП         | Фролова  |        |     |   |       |        |      |
|             |          |        |     | Архитектурные решения                                                                                                |       |        |      |
|             |          |        |     | План расстановки технологического оборудования в нежил. 3 этаж                                                       |       |        |      |
| Н.Контроль  | Лукашова | 06.26  |     |   | 06.26 |        |      |
| ГВП         |          | 06.26  |     |   |       |        |      |
|             |          |        |     | ООО "АРТИС"   |       |        |      |
|             |          |        |     | Формат А0 В4 х 1189                                                                                                  |       |        |      |