



Общество с ограниченной ответственностью
Проектно-строительная компания

« А З У Р И Т »

Проектирование объектов
капитального строительства

Рег. № члена СРО №0236-19 от 28.03.2019г. СРО АП «АПП»

Экз. №

Заказчик: "АНО «ОЭК Стройтрест»"

**Капитальный ремонт общеобразовательного учреждения (ГБОУ
«Школа № 429»), расположенного по адресу: г. Москва, 5-ая ул.
Соколиной Горы д.14**

1 этап

ПРОЕКТНАЯ ДОКУМЕНТАЦИЯ

«Архитектурно-планировочные решения»

16-25/Г-П-АПР

Изм.	№ док.	Подп.	Дата

Москва, 2025



Общество с ограниченной ответственностью
Проектно-строительная компания

« А З У Р И Т »

Проектирование объектов
капитального строительства

Рег. № члена СРО №0236-19 от 28.03.2019г. СРО АП «АПП»

Экз. №

Заказчик: "АНО «ОЭК Стройтрест»"

**Капитальный ремонт общеобразовательного учреждения (ГБОУ
«Школа № 429»), расположенного по адресу: г. Москва, 5-ая ул.
Соколиной Горы д.14**

1 этап

ПРОЕКТНАЯ ДОКУМЕНТАЦИЯ

«Архитектурно-планировочные решения»

16-25/Г-П-АПР

Технический директор –
главный инженер

Главный инженер проекта



Н.А. Губарев

А.В. Мурашов


Изм.	№ док.	Подп.	Дата

Москва, 2025

Взам. инв. №

Подп. и дата

Инв. № подл.

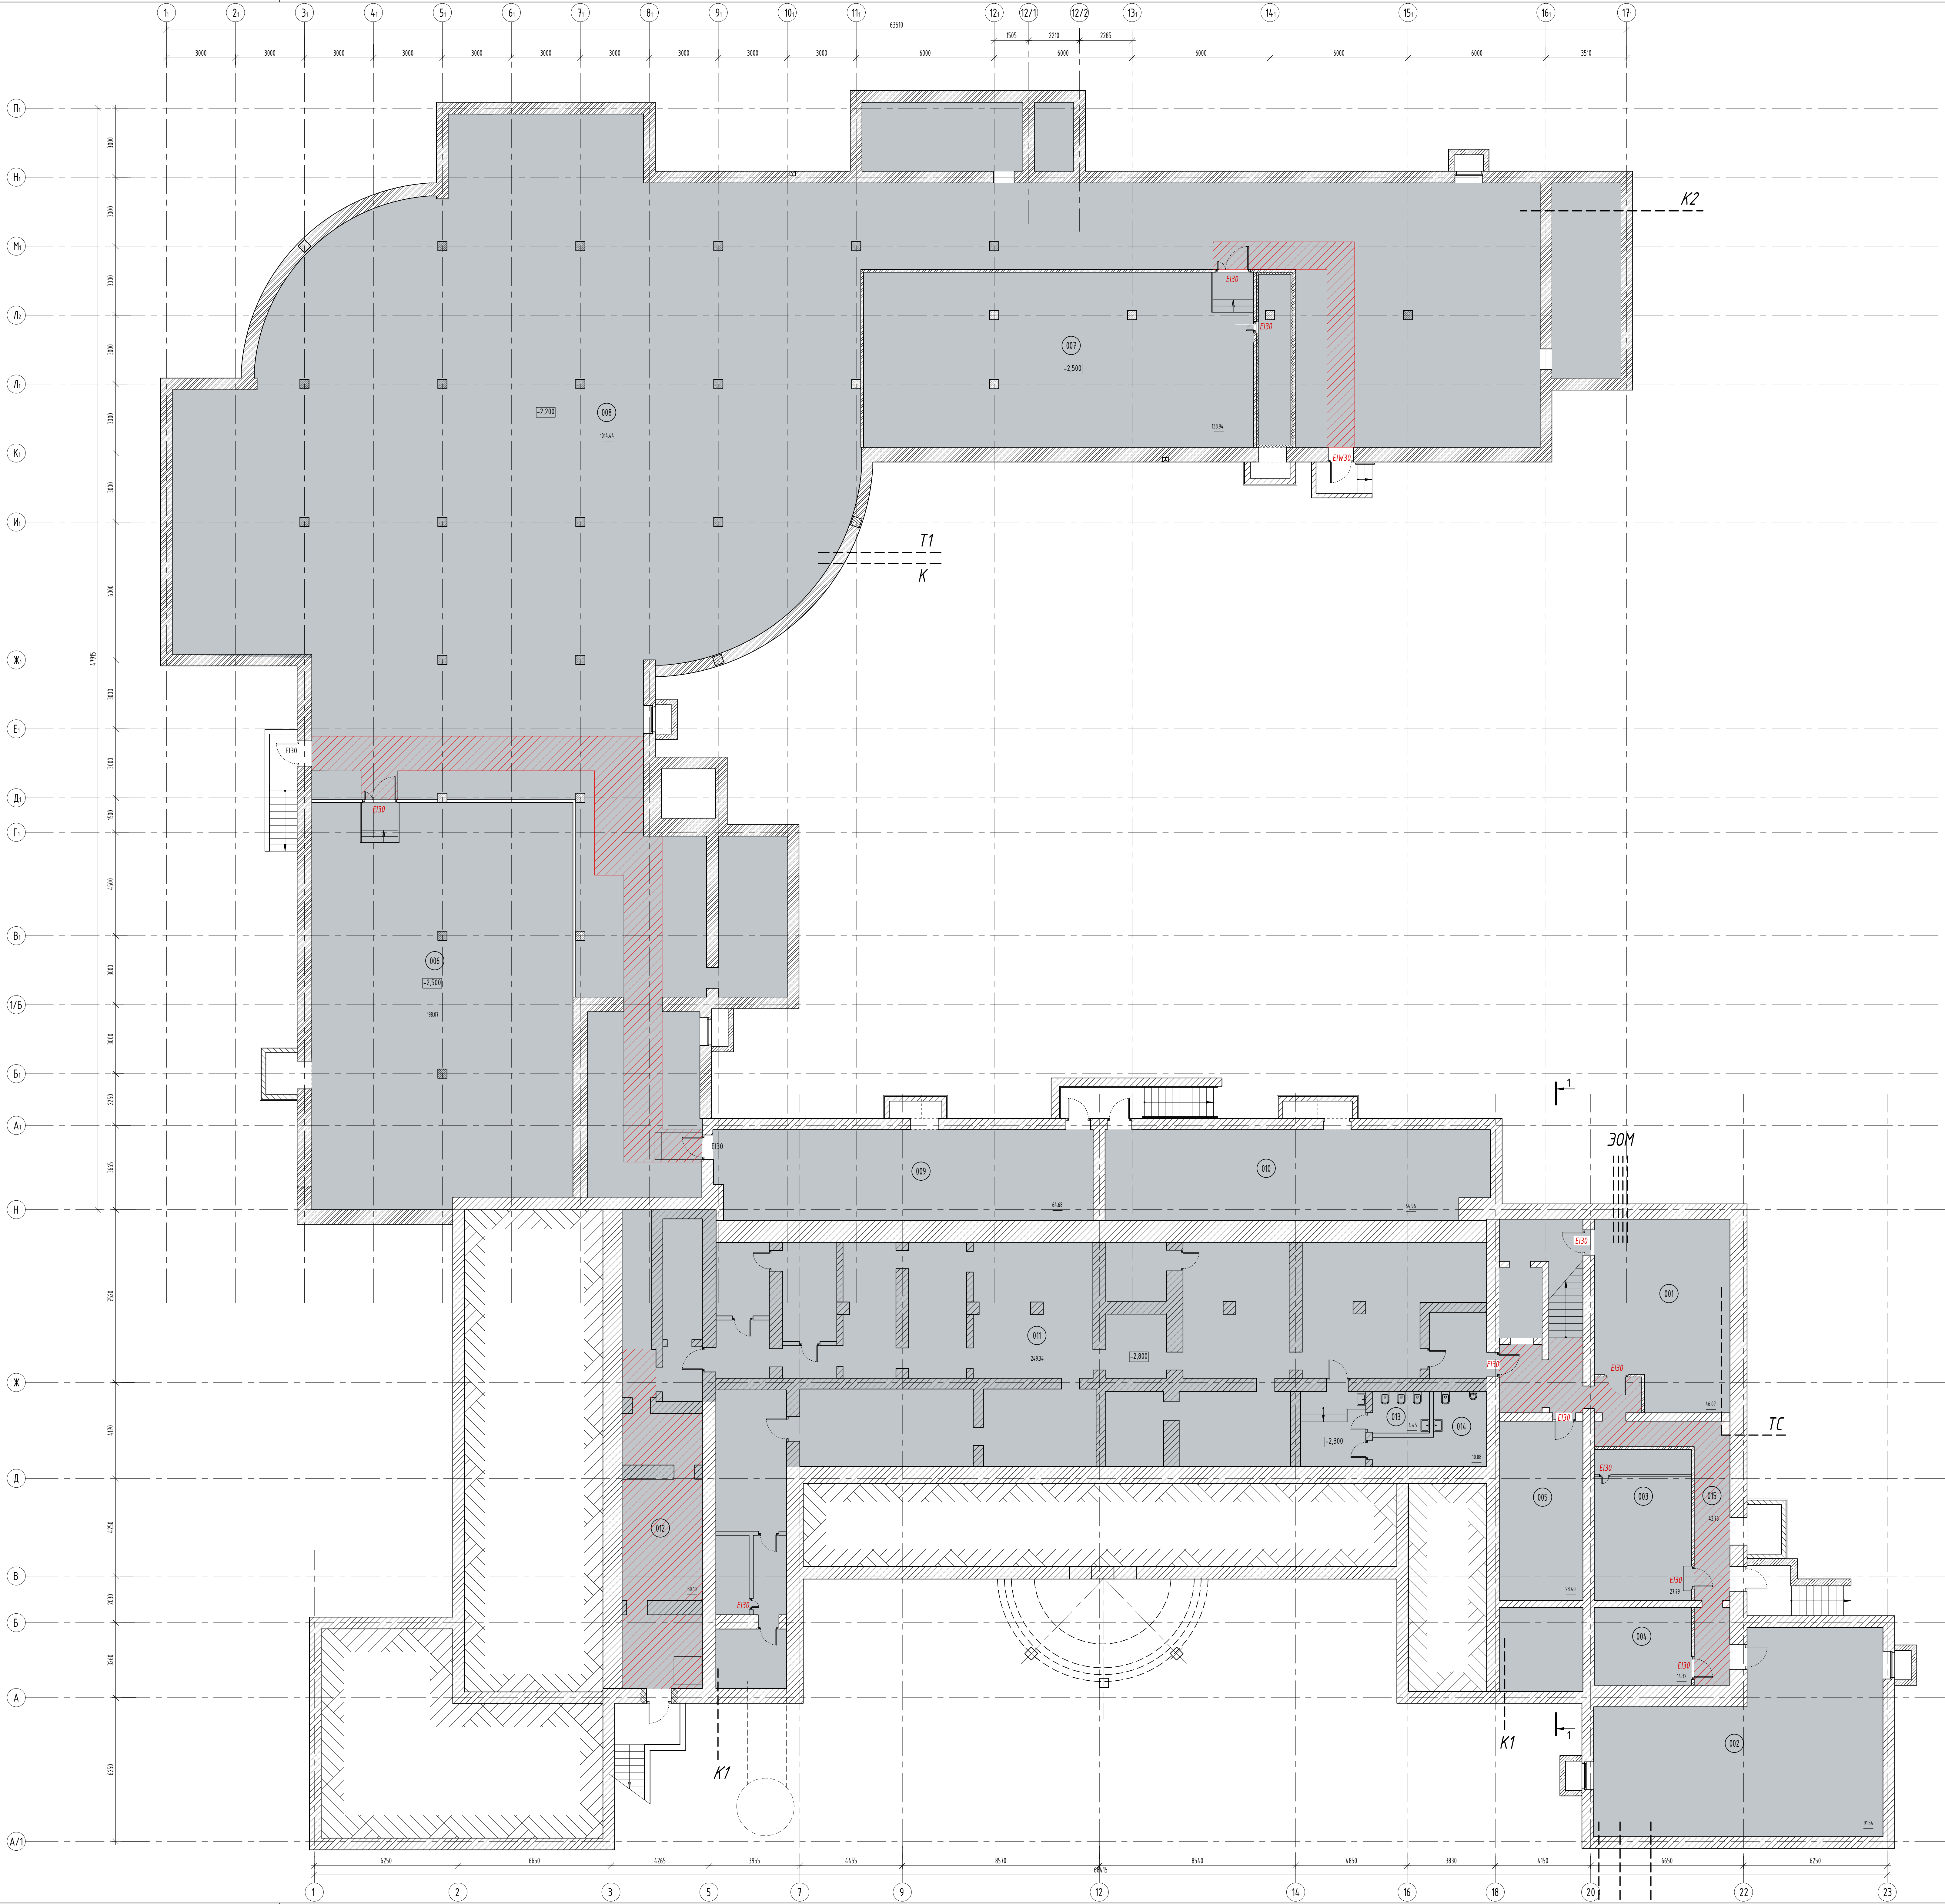

Экспликация помещений			
Номер помещения	Наименование	Площадь м2	Кат. помещ.
001	ИТП	46,07	Д
002	Водяной узел и насосная	915,4	Д
003	Венткамера	27,79	В3
004	Венткамера	14,32	В3
005	Венткамера	28,40	В3
006	Венткамера	198,07	В3
007	Венткамера	138,94	В3
008	Техническое помещение для прокладки инженерных коммуникаций	1014,44	В3
009	Венткамера	64,68	В3
010	Венткамера	64,96	В3
011	Защитное помещение гражданской обороны	243,34	
012	Коридор	50,95	
013	Санузел	10,88	
014	Санузел	4,45	
015	Коридор	43,76	
Итого:			

Условные обозначения:

- Технические помещения
- Пути эвакуации

- Возможность устройства проемов в несущих стенах будет уточняться в проекте.
- Размер и расположение вентиляционных шахт будет уточнен в проекте.
- Шахты предназначены для прокладки инженерных коммуникаций и стояков (ВК, СС, ЗОМ), оборудуются лестницами для обслуживания.
- * катеризирование по взрывопожарной опасности данных помещений выполнить на этапе проектирования.

						-АТР		
						Капитальный ремонт объекта "ГБОУ Школа № 429 "Сокольная гора", расположенного по адресу: г.Москва, ул. Сокольной горы 5-я, д. 14		
Ит.	Кол-во	Лист	№ док.	Подпись	Дата	Архитектурно-планировочные решения		
Разработчик	Кареева	Лист	№ док.	Подпись	Дата	Стадия	Лист	Листов
Разработчик	Липовская	Лист	№ док.	Подпись	Дата	П	1	
Проектировщик	Артемьев	Лист	№ док.	Подпись	Дата	План подвала. М 1:100		
И. контр.	Варфоломеев	Лист	№ док.	Подпись	Дата	000 ЛСК "Аэриум"		
Гип	Артемьев	Лист	№ док.	Подпись	Дата	ФОРМАТ А0		

Формат: А4х1189

1 2 3 4 5 6 7 8 9 10 11 12 12/1 13 14 15 16 17

Пл

Н

М

А

К

И

Ж

Е

Д

Г

В

1/В

Б

1/Б

А

Х

А

В

Б

А

А/1

Граница пожарной зоны

Най развешенной зоны пожарной зоны, защита
аппараты противопожарной системы типа Водостойкий
аппараты системы НГ в 2 слоя с обеих сторон (или
аналог) по методу карману до поверхности отступа нано
защитки на высоте 2 м от пр. ч. н.

Граница пожарной зоны

Граница пожарной зоны

Экспликация помещений


Номер помеще-ния	Наименование	Площадь, м2	Кат. помеще-ния
101	Танбур	35.02	
102	Вестибюль (зона ожидания для посетителей)	278.47	
103	Санузлы для МП	4.90	
104	Административный кабинет тип 1 (начальная школа)	26.21	
106	Санузел для девочек (начальная школа)	23.25	
107	Гардеробная для обучающихся (основная и старшая школа)	97.54	
108	Гардеробная для обучающихся (основная и старшая школа)	35.25	
109	Гардеробная для обучающихся (начальная школа)	72.49	
110	Лестничная клетка (ЛК)	24.50	
111	Коридор	17.66	
112	Санузел для мальчиков (начальная школа)	12.73	
113	Санузел для персонала	2.78	
114	Учебные кабинеты (2-4 классы)	61.23	
115	Учебные кабинеты (2-4 классы)	59.89	
116	Рекреация (начальная школа)	64.22	
117	Учебные кабинеты (2-4 классы)	59.22	
118	ПМ	2.78	Б4
119	Санузел для девочек (начальная школа)	12.73	
120	Коридор с рекреацией (основная и старшая школа)	100.68	
121	Вестибюль	109.33	
122	Комната охраны (с диспетчерским пунктом)	23.43	
123	Гардеробная комната (для учителей)	9.86	
124	Помещение связи	8.84	Б4
125	Санузел для мальчиков (начальная школа)	21.73	
127	Учебные кабинеты (1 класс)	51.26	
128	Учебные кабинеты (1 класс)	53.71	
129	Учебные кабинеты (1 класс)	58.81	
130	Коридор с рекреацией	117.57	
131	Лестничная клетка Тип И2	27.18	
132	Вестибюль	42.02	
133	Электрощитовая	16.16	Б3
134	Туалет мебели с местом для приёма пищи, дежурных работников и хранения уборочного инвентаря, предназначенных для помещений медицинского назначения	16.93	Б3
135	Кабинет врача	27.00	
136	Процедурный (прибытийный) кабинет	20.88	
137	Коридор	23.56	
138	Комната инструктора (с душем и санузлом)	19.16	
139	ПМ	6.79	Б4
140	Санузел для персонала	3.27	
141	Помещение связи	12.01	Б3
142	Помещение для персонала (с душем и санузлом)	17.46	
143	ПМ	6.16	Б4
144	Помещение для хранения хранения пищевых отходов	7.15	Б4
145	Кладовая и моечная обратной тары	6.92	Б4
146	Эксплуатационный цех	7.45	Б4
147	Коридор	32.69	
147.1	Место установки холодильного оборудования	19.19	Б3
148	Кладовая сухих продуктов	7.54	Б4
149	Досмотровый цех	15.16	Б3
150	Горючий цех	39.81	Б3
151	Моечная для кухонной посуды	11.04	Д
152	Моечная для столовой посуды	32.87	Д
152.1	Предмоечная	7.54	Д
153	Холодный цех	16.12	Б3
154	Обеденный зал	181.69	
155	Раздевальня	12.49	
156	Санузел	2.40	
157	Санузел	2.48	
158	Душевые	4.15	
159	Душевые	4.12	
160	Санузел для мальчиков	8.71	
161	Санузел для девочек	10.00	
162	Раздевальня	16.58	
163	Лестничная клетка (ЛК)	21.00	
164	Техническое помещение	4.16	Б4
165	Спортивная	21.81	Б3
166	ПМ	4.30	Б4
167	Универсальный спортивный зал	270.82	
168	Лестничная клетка (ЛК)	25.50	
169	Коридор и рекреация (основная и старшая школа)	281.24	
171	Электрощитовая	2.89	Б4
172	Лестничная клетка (ЛК)	21.00	
Итого:		0.00	

Условные обозначения:

- Помещение общего пользования
- Административные и служебно-бытовые помещения
- Гардеробные
- Технические помещения
- Сантехнические помещения
- Учебные кабинеты начальной школы
- Спортивные помещения
- Лестничная
- Медицинские помещения
- 101 Номер помещения по экспликации
- EW30 Маркировка огнезащиты дверей, перегородок

- Возможность устройства проемов в несущих стенах будет уточняться в проекте.
- Размер и расположение вентиляционных шахт будет уточнен в проекте.
- Шахты предназначены для прокладки инженерных коммуникаций и стояков (ВК, СС, ЗОМ), оборудуются люками для обслуживания.
- ★ классификация по взрывопожарной опасности данных помещений выполняется на этапе проектирования.

					-АТР		
					Капитальный ремонт объекта "ГБОУ Школа № 429 "Соколовая гора", расположенного по адресу: г.Москва, ул. Соколовой горы 5-я, в. 14		
Ит	Кол-во	Лист	М.П.	Подпись	Дата	Архитектура-планировочные решения	Лист
Разраб	Кареева	2025.11				Л	2
Разраб	Липовская	2025.11					
Проектир	Артемьев	2025.11					
Н. комп.	Ворожоб	2025.11				План 1 этажа. М 1:100	000 ПК "Аэриум"
Гип	Артемьев	2025.11					ФОРМАТ А0

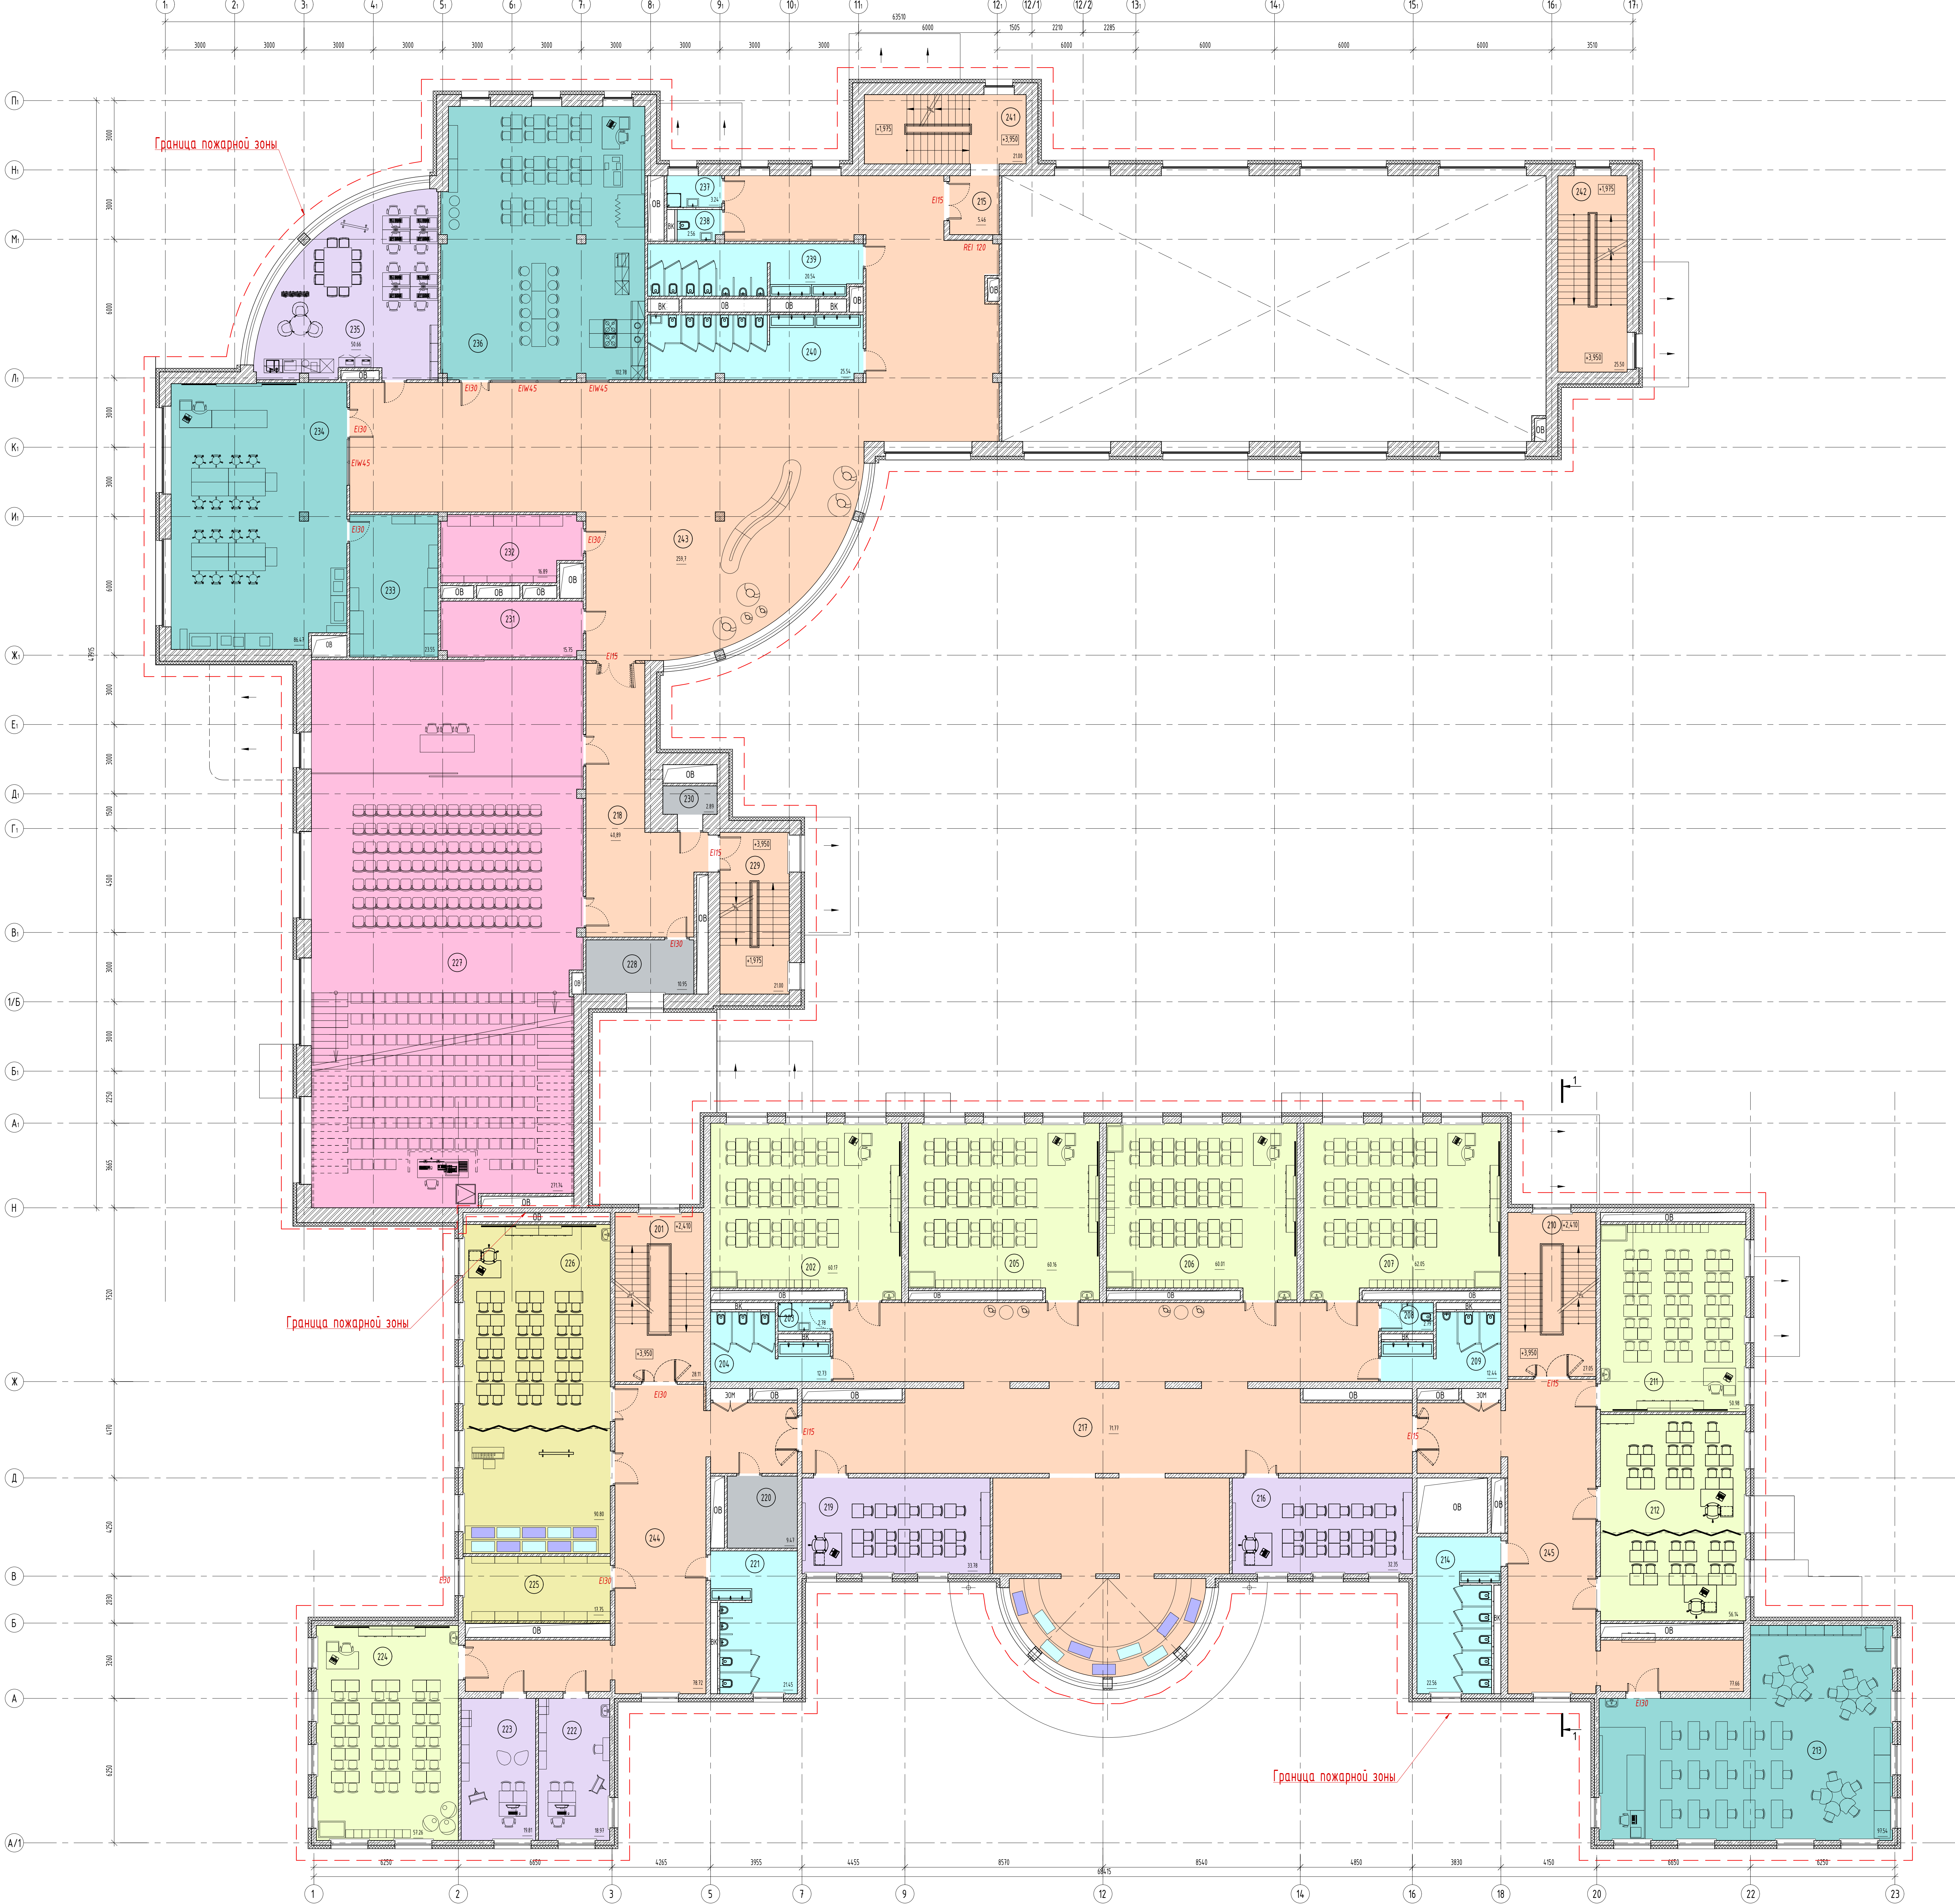


Экспликация помещений			
Номер помеще-ния	Наименование	Площадь, м2	Кат. помеще-ния
201	Лестничная клетка Тип И2	28.82	
202	Учебные кабинеты (2-4 классы)	60.17	
203	ПМ	2.78	Б4
204	Санузлы для девочек (начальная школа)	12.73	
205	Учебные кабинеты (2-4 классы)	60.16	
206	Учебные кабинеты (2-4 классы)	60.01	
207	Учебные кабинеты (2-4 классы)	62.05	
208	Санузел для персонала	2.79	
209	Санузел для мальчиков (начальная школа)	12.44	
210	Лестничная клетка (И1)	27.05	
211	Учебные кабинеты (2-4 классы)	50.98	
212	Кабинет иностранного языка с возможностью деления трансформируемой перегородкой на два помещения (начальная школа)	56.14	
213	Лаборатория-исследовательский комплекс для изучения естественных наук	97.02	Б3
214	Санузел для девочек (начальная школа)	23.25	
215	Танц-зал	5.46	
216	Кабинет для индивидуальных занятий с малой группой	32.35	
217	Коридор с рекреацией (начальная школа)	246.95	
218	Коридор	40.89	
219	Кабинет для индивидуальных занятий с малой группой	33.78	
220	Помещение (взв.)	9.94	Б3
221	Санузел для мальчиков (начальная школа)	21.45	
222	Кабинет для индивидуальных занятий, в т.ч. с учителями-наставниками	18.97	
223	Кабинет для индивидуальных занятий, в т.ч. с коррекционными педагогами	19.22	
224	Учебные кабинеты (2-4 классы)	57.26	
225	Кабинет кабинета творческой мастерской	17.75	Б3
226	Творческая мастерская с возможностью разделения трансформируемой перегородкой на два помещения	90.80	
227	Многофункциональное пространство с функцией актового зала (с эстрадой в угловой части)	271.74	
228	Помещение (взв.)	10.95	Б3
229	Лестничная клетка (И1)	21.00	
230	Электрощитовая	2.89	Б4
231	Архитектурная	15.75	
232	Кабинет кабинета	16.89	Б3
233	Кабинет кабинета материальной технологии	23.55	Б3
234	Кабинет материальной технологии тип 2	66.47	Б3
235	Кабинет с рабочим пространством для учителей тип 1 (начальная школа)	50.66	
236	Кабинет материальной технологии тип 1	102.78	Б3
237	ПМ	3.24	Б4
238	Санузел для персонала	2.56	
239	Санузел для мальчиков (основная и старшая школа)	20.54	
240	Санузел для девочек с комнатой личной гигиены (основная и старшая школа)	23.54	
241	Лестничная клетка (И1)	21.00	
242	Лестничная клетка (И1)	25.50	
243	Коридор и рекреация (основная и старшая школа)	259.70	
244	Коридор	78.72	
245	Коридор	77.66	
Итого:		0.00	

- Условные обозначения:
- Помещение общего пользования
 - Административные и служебно-бытовые помещения
 - Специализированные помещения
 - Технические помещения
 - Группа зрительного зала
 - Учебные кабинеты начальной школы
 - Специализированные кабинеты
 - Универсальные студии
 - 201 Номер помещения по экспликации
 - EW30 Маркировка генетической значимости дверей, перегородок

- Возможность устройства проемов в несущих стенах будет уточняться в проекте.
- Размер и расположение вентиляционных шахт будет уточнен в проекте.
- Шахты предназначены для прокладки инженерных коммуникаций и стояков (ВК, СС, ЗОМ), оборудуются люками для обслуживания.
- ★ классификация по взрывопожарной опасности данных помещений выполнить на этапе проектирования.

				-АТР		
				Капитальный ремонт объекта "ГБОУ Школа № 429 "Соколовая гора", расположенного по адресу: г.Москва, ул. Соколовой горы 5-я, д. 14		
				Архитектурно-планировочные решения		
				Стадия	Лист	Листов
				П	3	
				Лист 2 этажа. М 1:100		
				000 ПК "Аэриум"		
				ФОРМАТ А0		

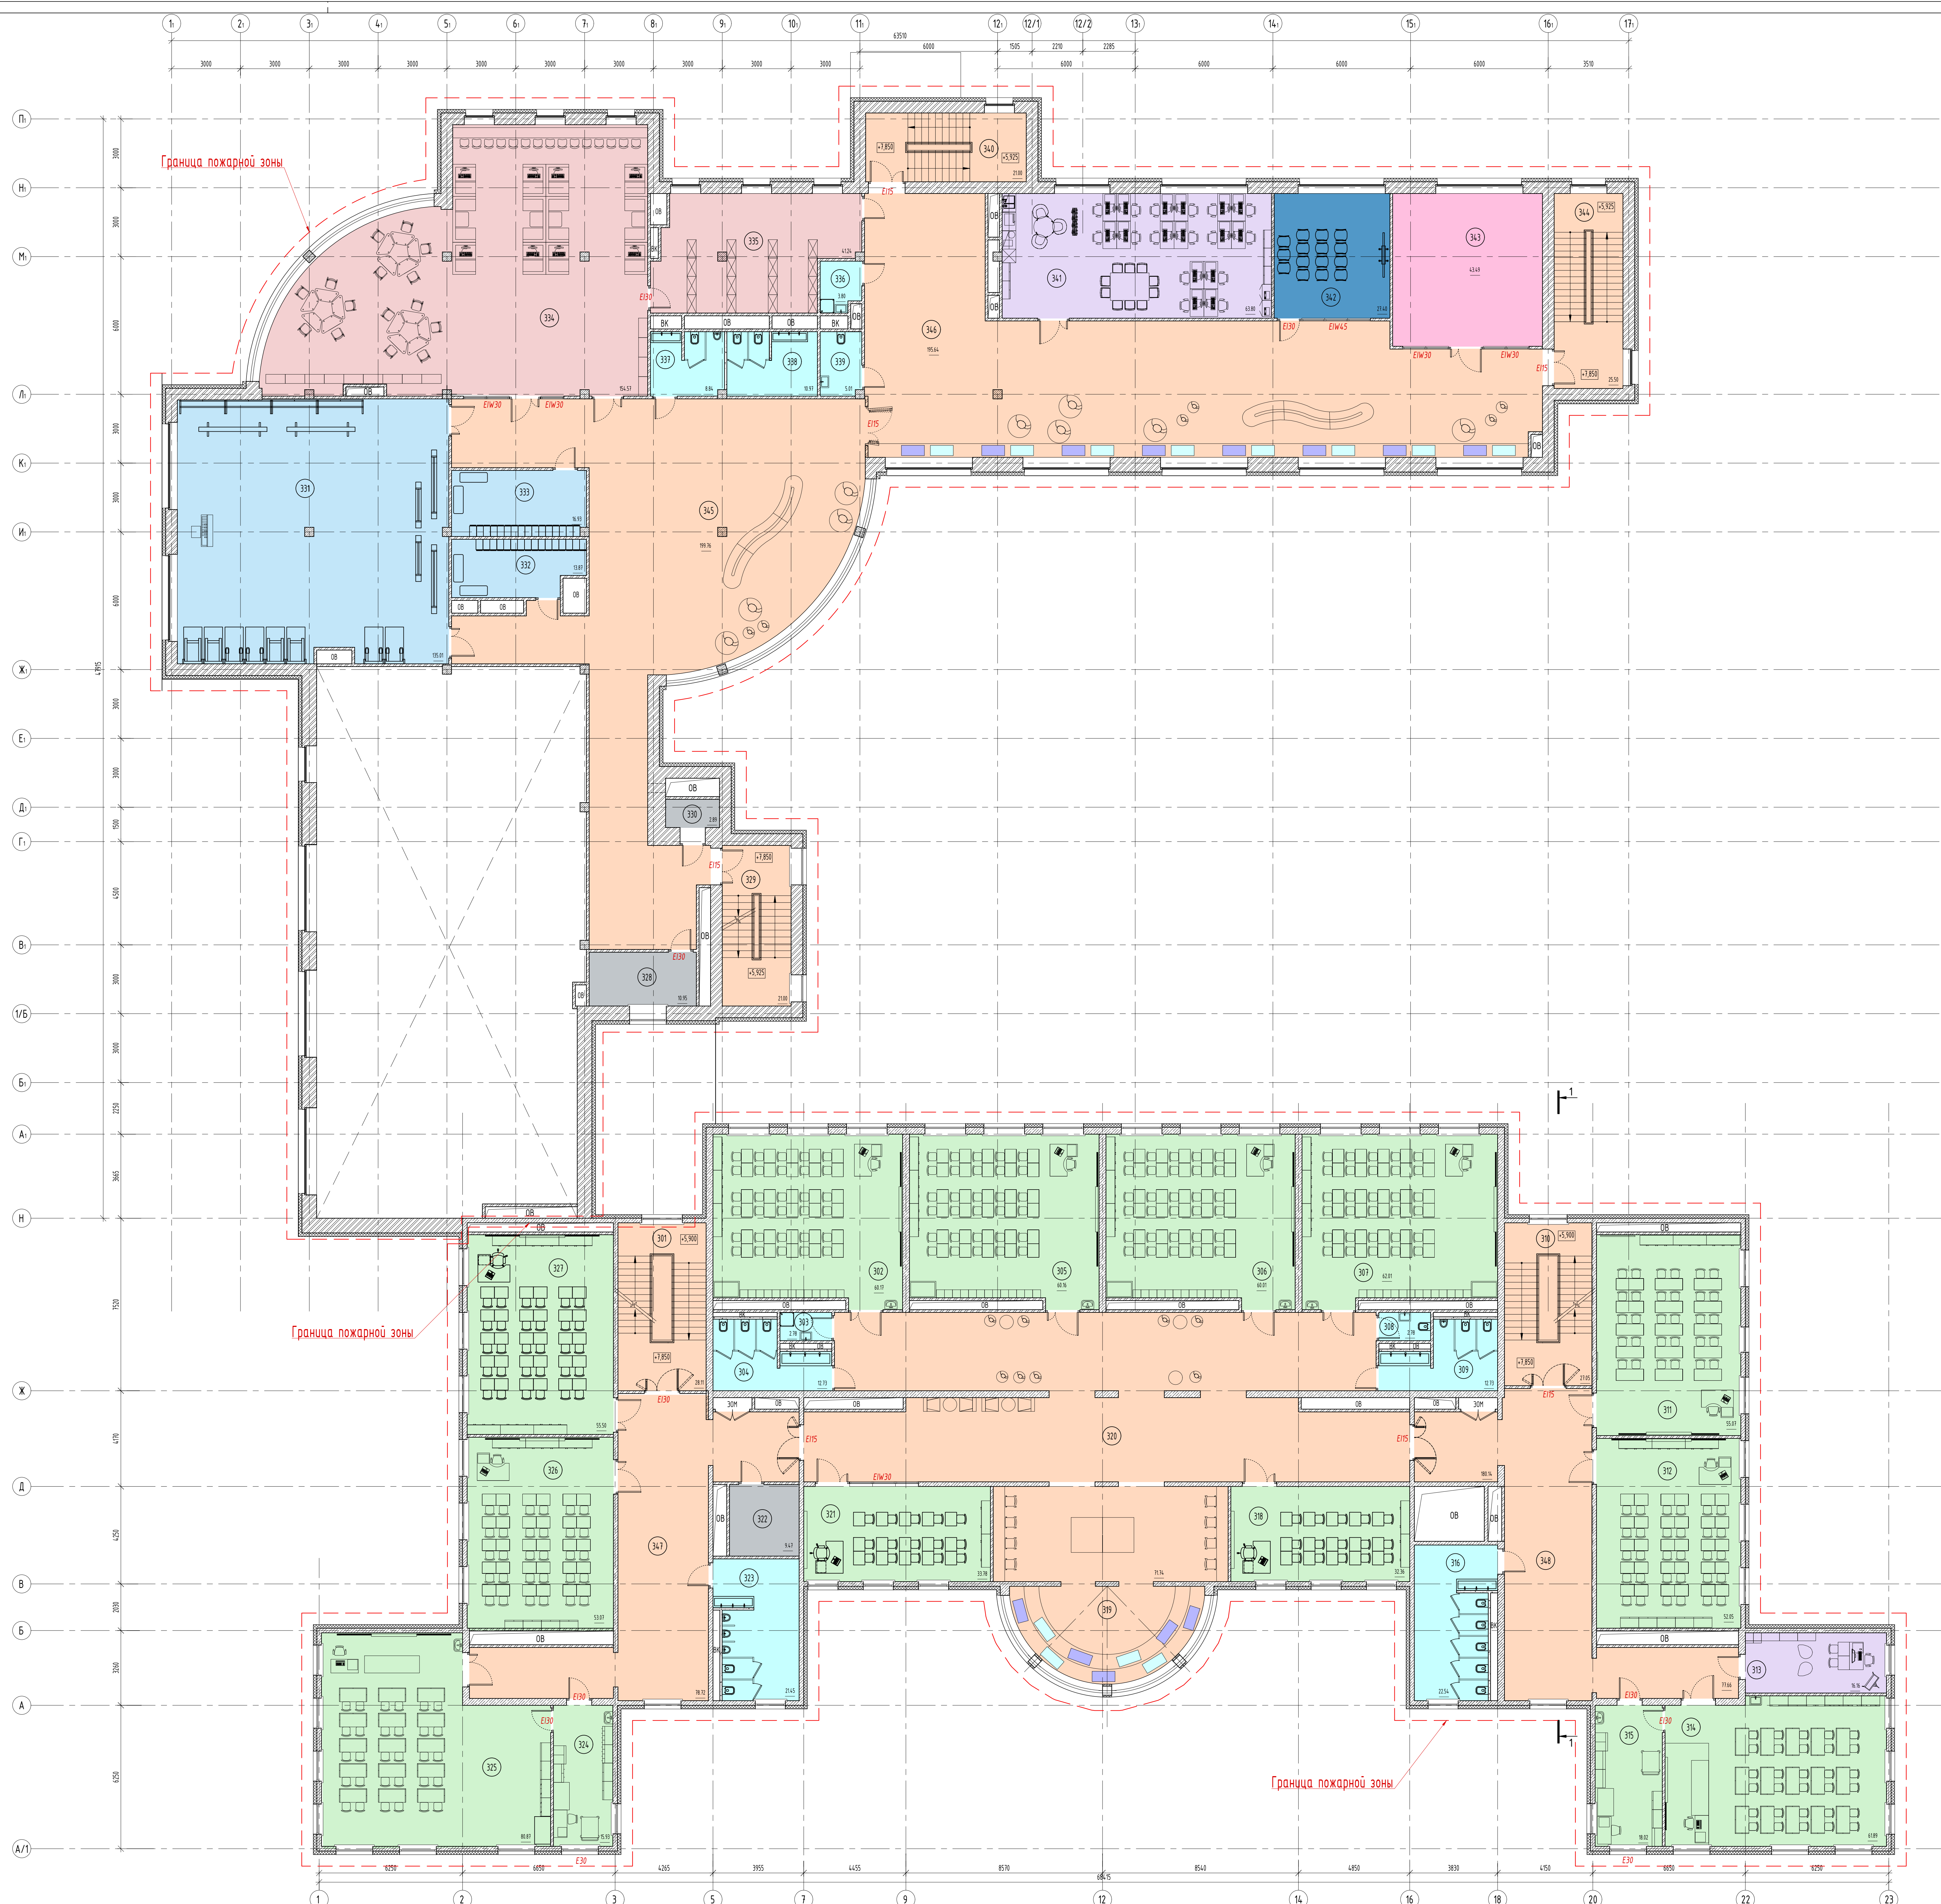

Экспликация помещений			
Номер помещения	Наименование	Площадь	Кл. помещения
301	Лесничья клетка Тип М2	28,82	
302	Кабинет русского языка и литературы	69,17	
303	ПМ1	2,78	84
304	Снижение для девочек (основная и старшая школа)	12,73	
305	Кабинет русского языка и литературы	69,16	
306	Кабинет математики	60,01	
307	Кабинет математики	62,01	
308	Снижение для парсиско	2,75	
309	Снижение для мальчиков (основная и старшая школа)	12,73	
310	Лесничья клетка (П1)	21,05	
311	Кабинет географии	55,07	
312	Универсальный учебный кабинет	56,05	
313	Кабинет для индивидуальных занятий; 6 п.ч. с педагогом-психологом	16,16	
314	Учебный кабинет для изучения естественных наук: физика	61,36	
315	Лабаратория кабинета физики	18,02	83
316	Снижение для девочек с компьютерной техникой (основная и старшая школа)	23,25	
317	Подсобное помещение	6,64	84
318	Кабинет иностранного языка (основная и старшая школа)	32,36	
319	Рекреация (основная и старшая школа)	71,74	
320	Коридор	179,36	
321	Кабинет иностранного языка (основная и старшая школа)	33,78	
322	Помещение спорт	9,94	84
323	Снижение для мальчиков (основная и старшая школа)	21,73	
324	Лабаратория кабинета биологии	15,53	83
325	Учебный кабинет для изучения естественных наук: биология и ГСР	80,87	
326	Универсальный учебный кабинет	53,07	
327	Кабинет истории тип 1	55,50	
328	Помещение спорт	10,95	83
329	Лесничья клетка (П1)	21,05	
330	Электрощитовая	2,89	84
331	Универсальное помещение с возможностью организации компьютерного зала (переворот)	135,01	
332	Раздевальня	16,87	
333	Раздевальня	13,93	
334	Интегрированный информационный библиотечный центр с точки для индивидуальных занятий	154,57	
335	Интегрированный информационный библиотечный центр (принятие (экспертный фонд) и выдача книг)	41,24	83
336	ПМ1	2,88	84
337	Снижение для мальчиков (основная и старшая школа)	10,84	
338	Снижение для девочек (основная и старшая школа)	8,97	
339	Снижение для парсиско	5,01	
340	Лесничья клетка (П1)	21,05	
341	Кабинет с рабочим пространством для учителей Тип 1 (основная и старшая школа)	62,92	
342	Универсальное помещение с возможностью организации Недоступности	27,02	83
343	Помещение музея	43,49	
344	Лесничья клетка (П1)	25,56	
345	Коридор с рекреацией (основная и старшая школа)	199,70	
346	Коридор с рекреацией (основная и старшая школа)	195,64	
347	Коридор	78,72	
348	Коридор	77,66	
Итого:		0,00	


Помещения общего пользования
 Синтетические помещения
 Учебные кабинеты и старшие школы
 Административные и служебно-бытовые помещения
 Спортивные помещения
 Технические помещения
 Библиотека-медiateка
 Музеи
 Медиацентр

301 Номер помещения по экспозиции

ЕКЭС Маркировка огнестойкости элементов дверей, перегородок

1. Возможность устройства проемов в несущих стенах будет уточняться в проекте. Размер и расположение вентиляционных шахт будет уточнен в проекте.
2. Шахты предназначение для прокладки инженерных коммуникаций и стоек (ВК, оборудуются лючками для обслуживания).
3. ★ категорирование по взрывопожарной опасности данных помещений выполнить проектирования.

								-АПР
								Капитальный ремонт объекта "БОУ Школа № 429 "Секанная гора", расположенного по адресу: г Москва, ул. Секанной горы 5-я, 8, 9.
								Архитектурно-планировочные решения
Изм.	Кол-во	Листы	№ док	Подпись	Дата	Страниц	Лист	Листов
Разработчик				Арсентьев	2026.05			
Проверенный				Арсентьев	2026.05		П	4
								Планы 3 этажа М 1:100
Н. компет.				Варохов	2026.05		ООО ПСК "Архрум"	
Гит				Труфанова	2026.05			

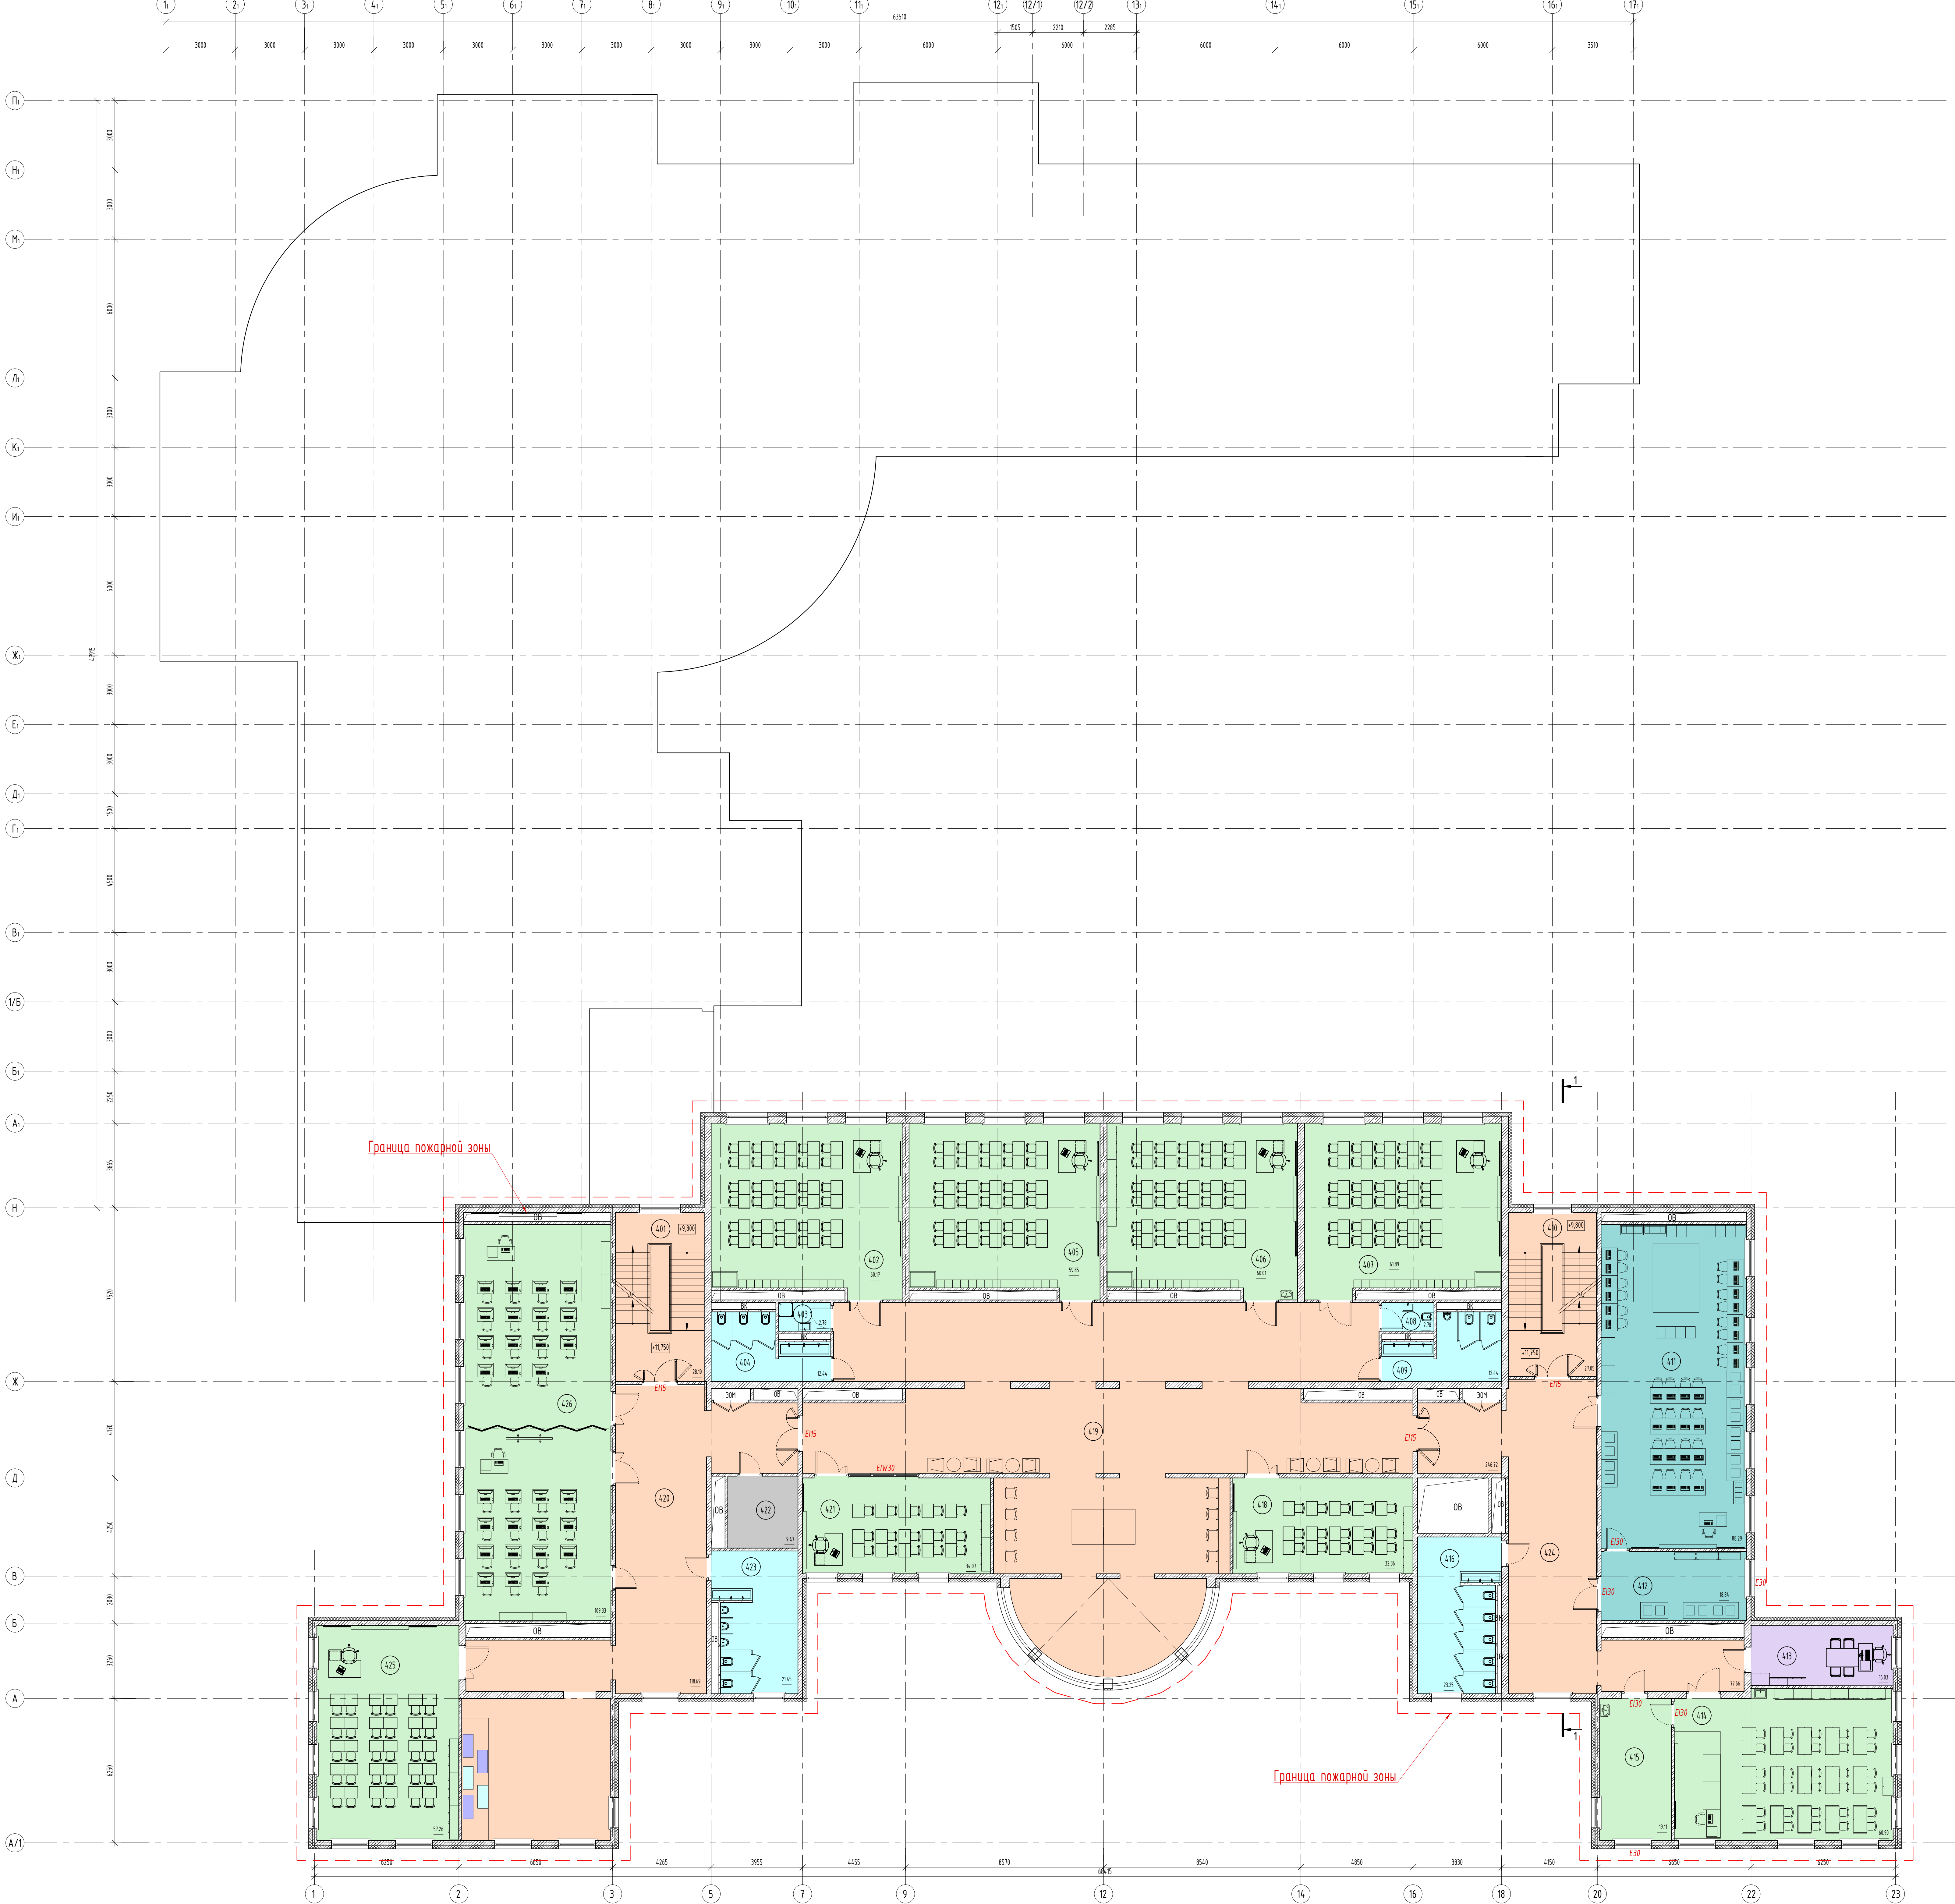

Экспликация помещений

Номер помещения	Наименование	Площадь, м2	Кол. помещ.
401	Лестничная клетка Тип Н2	28.81	
402	Кабинет русского языка и литературы	60.17	
403	ПРИ	2.78	В4
404	Санузел для девочек (основная и старшая школа)	12.73	
405	Кабинет русского языка и литературы	59.85	
406	Кабинет математики	60.01	
407	Кабинет математики	61.89	
408	Санузел для персонала	2.78	
409	Санузел для мальчиков (основная и старшая школа)	12.44	
410	Лестничная клетка (П1)	26.98	
411	Кабинет информационных технологий	88.29	
412	Лаборантская при кабинете информационных технологий	18.84	Б3
413	Административный кабинет тип 1 (основная и старшая школа)	16.03	
414	Учебные кабинеты для изучения естественных наук	60.90	
415	Лаборантская кабинета химии	19.11	Б3
416	Санузел для девочек с комнатой личной гигиены (основная и старшая школа)	23.25	
417	Подсобная помещения	7.30	В4
418	Кабинет иностранного языка (основная и старшая школа)	32.36	
419	Коридор с зоной рекреации	246.72	
420	Коридор с зоной рекреации	118.69	
421	Кабинет иностранного языка (основная и старшая школа)	34.07	
422	Помещение с/жиз.	9.47	В4
423	Санузел для мальчиков (основная и старшая школа)	21.45	
424	Коридор	17.66	
425	Кабинет истории Тип 1	57.26	
426	Кабинет информатики с возможностью деления/трансформирования перегородкой на два помещения	109.33	
ИТОГО:			

- Условные обозначения:
- Помещения общего пользования
 - Административные и служебно-бытовые помещения
 - Специализированные помещения
 - Технические помещения
 - Учебные кабинеты основной и старшей школы
 - Специализированные кабинеты
 - 401 Номер помещения по экспликации
 - EW30 Наружная огнестойкости закрываемых дверей, перегородок

- Возможность устройства проемов в несущих стенах будет уточняться в проекте.
- Размер и расположение вентиляционных шахт будет уточнен в проекте.
- Шахты предназначены для прокладки инженерных коммуникаций и стояков (ВК, СС, ЗОМ), оборудуются люками для обслуживания.
- ★ калевозирование по взрывопожарной опасности данных помещений выполнить на этапе проектирования.

				-АТР		
				Капитальный ремонт объекта "ГБОУ Школа № 429 "Сокольная гора", расположенного по адресу: г.Москва, ул. Сокольной горы 5-я, д. 14		
Им.	Кол.дт	Лист	№ док.	Подпись	Дата	
Разработчик	Корнеева				2025.11	
Разработчик	Липовская				2025.11	
Проектировщик	Арсеньев				2025.11	
И. номер	Вариант	Итого	Листов	Подпись	Дата	
Гип	Арсеньев				2025.11	
				План 4 этажа. М 1:100		
				000 ПК "Азбука"		
				ФОРМАТ А0		

Капитальный ремонт здания Государственного бюджетного общеобразовательного учреждения города Москвы Школа № 429,
расположенная по адресу: г.Москва, ул. Соколиной горы 5-я, д. 14

Схема планировочной организации земельного участка. м 1:500



						-АПР			
						Капитальный ремонт объекта "ГБОУ Школа № 429 "Соколиная гора", расположенного по адресу: г.Москва, ул. Соколиной горы 5-я, д. 14			
Изм	Кол.уч	Лист	№ док	Подпись	Дата	Архитектурно-планировочные решения	Стадия	Лист	Листов
Разраб.		Корнеева			2025.11		П	6	
Разраб.		Липавская			2025.11				
Проверил		Арсентьев			2025.11	Схема планировочной организации земельного участка. м 1:500	ООО ПСК "Азурит" 		
Н. контр.		Воробьев			2025.11				
ГИП		Арсентьев			2025.11				